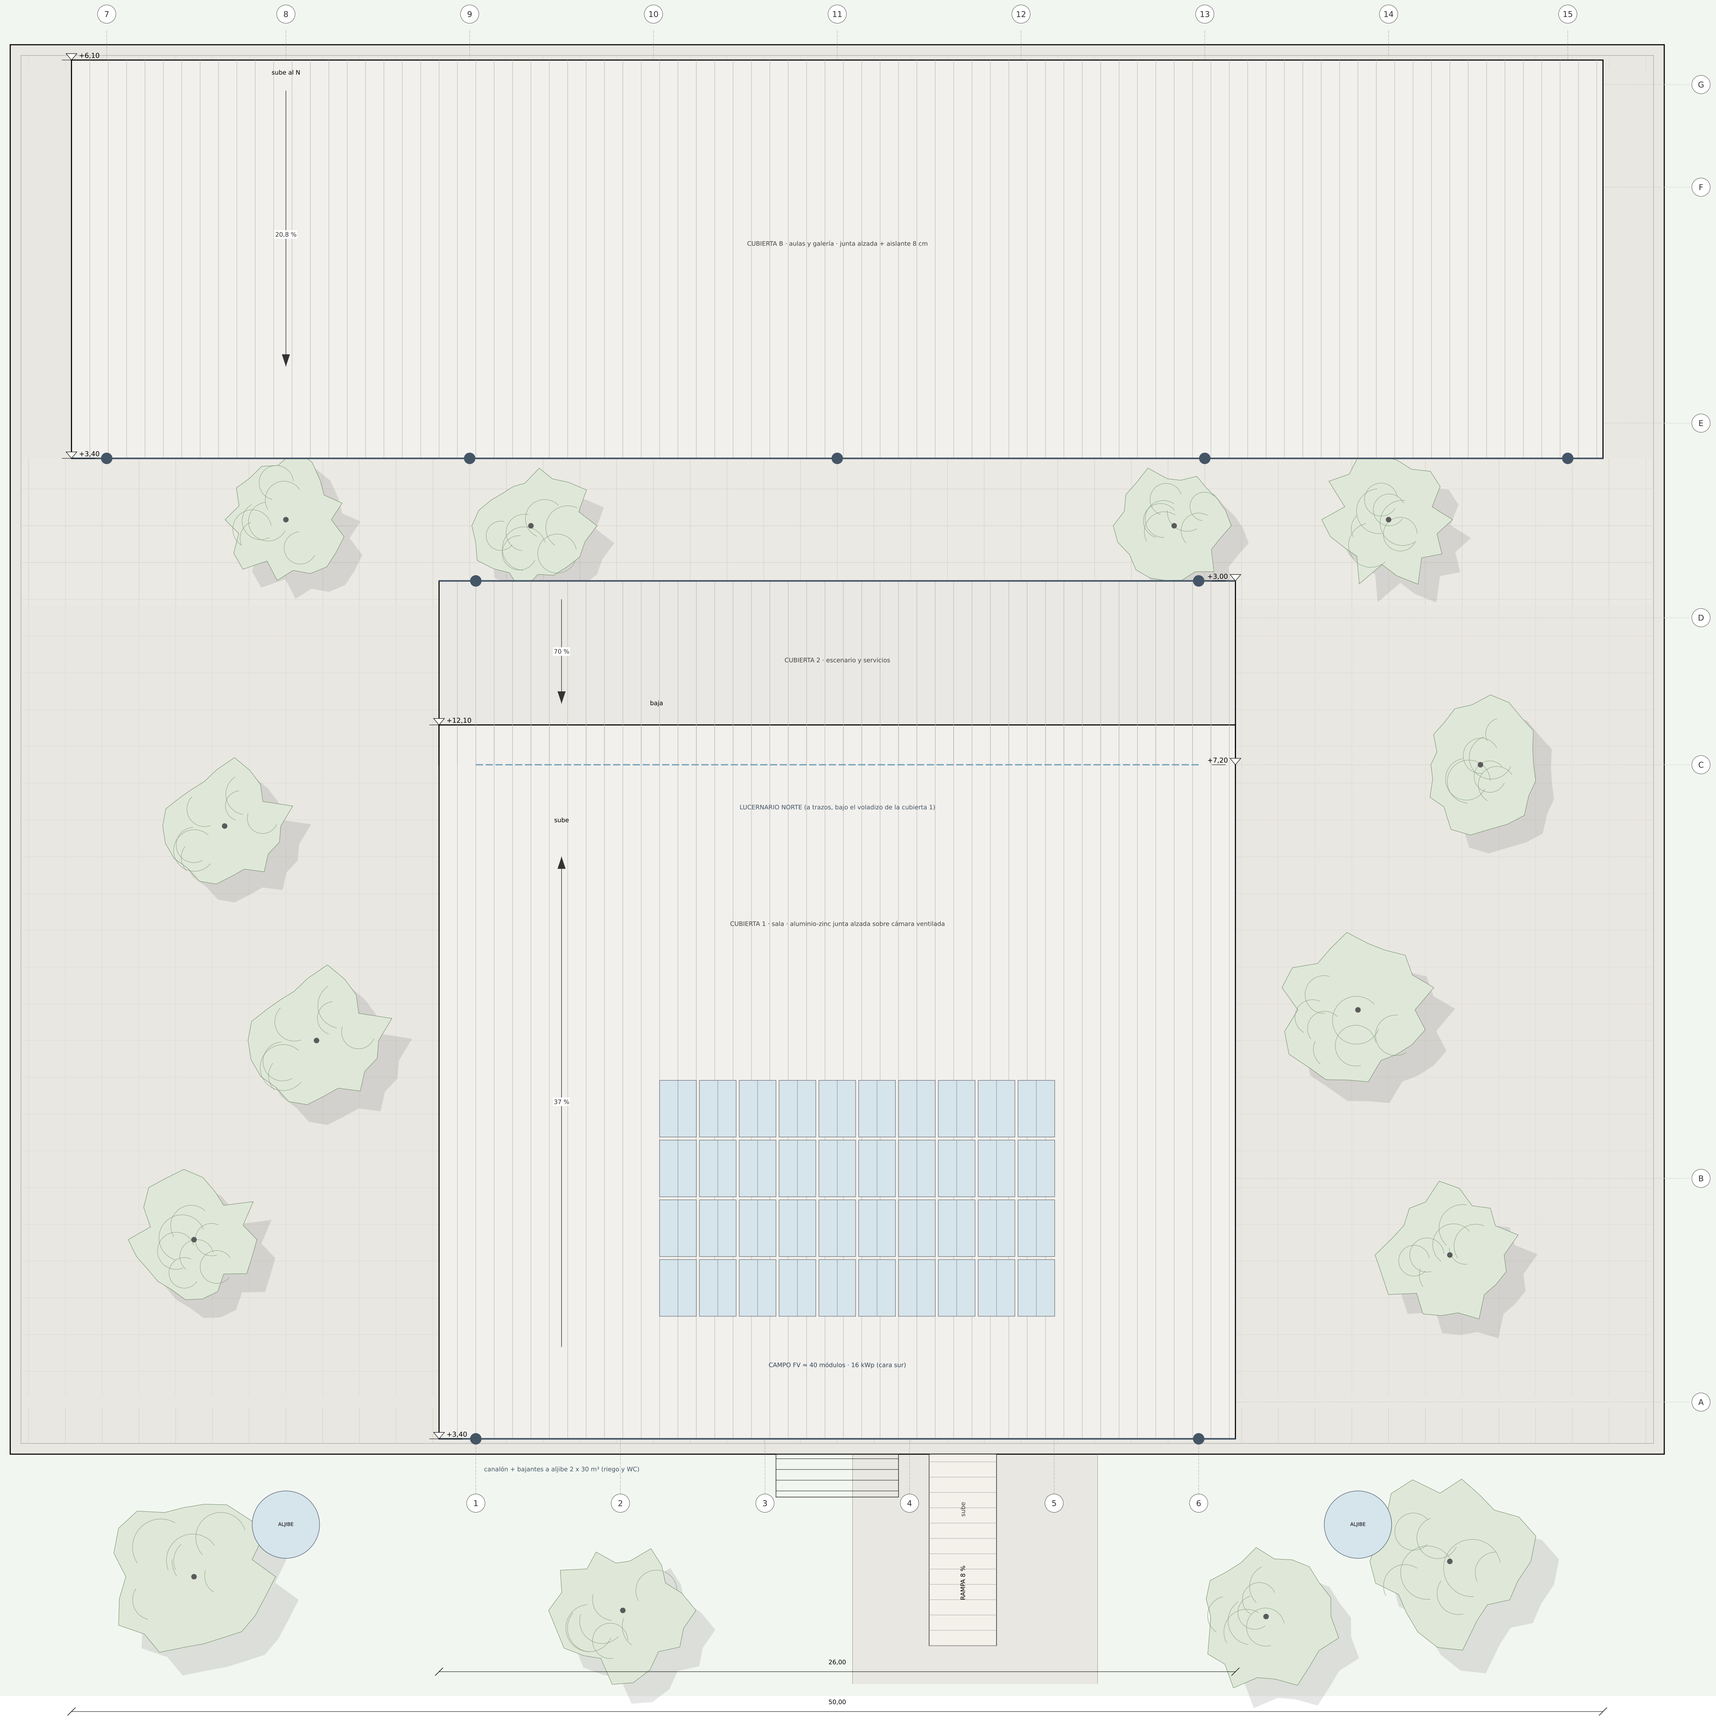


PLANTA DE CUBIERTAS E 1:100

N

0 1 2 5 10 m

LEYENDA DE CUBIERTAS

- Cubierta de chapa de aluminio-zinc, junta alzada
- Módulos fotovoltaicos (cara sur de la cubierta 1)
- Lucernario norte (vidrio + lamas de madera)
- Canalón y bajante
- Aljibe de aguas pluviales
- Muros por debajo (a trazos)

CUADRO DE CUBIERTAS

Cubierta	Pend.	Alero (m)	Cumbrera (m)
1 · Sala (cara sur)	37 %	+3,40	+12,10
2 · Escenario (cara norte)	70 %	+3,00	+7,20
B · Aulas y galería	20,8 %	+3,40	+6,10

Lucernario: 24 m x 3,3 m orientado al norte, bajo el voladizo de 1,3 m de la cubierta 1: luz difusa, sin sol directo, y salida del aire caliente por efecto chimenea.
Recogida pluvial: ≈ 1.800 mm/año x 1.250 m² de cubierta ≈ 2.250 m³/año; aljibes 2 x 30 m³ + rebose al cauce filtrado.

CASO_012 · PROPUESTA B Anteproyecto · Equipamiento comunitario musical	ESCALA **1:100**	LÁMINA **P02**
Planta de cubiertas	Anteproyecto	A1 · horizontal