CONDICIONES DE DISEÑO DEL DETALLE

Clima tropical húmedo: lluvia > 1.800 mm/año, máximas de 40 °C, humedad alta.

Muro de tierra (BTC) de 40 cm: inercia térmica y desfase de la onda de calor;

la lluvia se aleja con aleros de 2,0 m y zócalo de hormigón de 1,30 m sobre el

terreno, con barrera anticapilar. Sin aislante en muros: el aislante va en cubierta.

La cubierta es ligera y ventilada (cámara de 8 cm bajo la chapa) para que el calor


no pase a la sala; el aire caliente sale por la banda entre cubiertas (F2).

Plataforma a +0,80 m sobre el terreno por la posible inundación del cauce

(cota provisional, pendiente de estudio hidrológico). Cotas en metros.


F1 · SECCIÓN DE FACHADA OESTE DE LA SALA (CIMENTACIÓN A CUBIERTA)

E 1:20

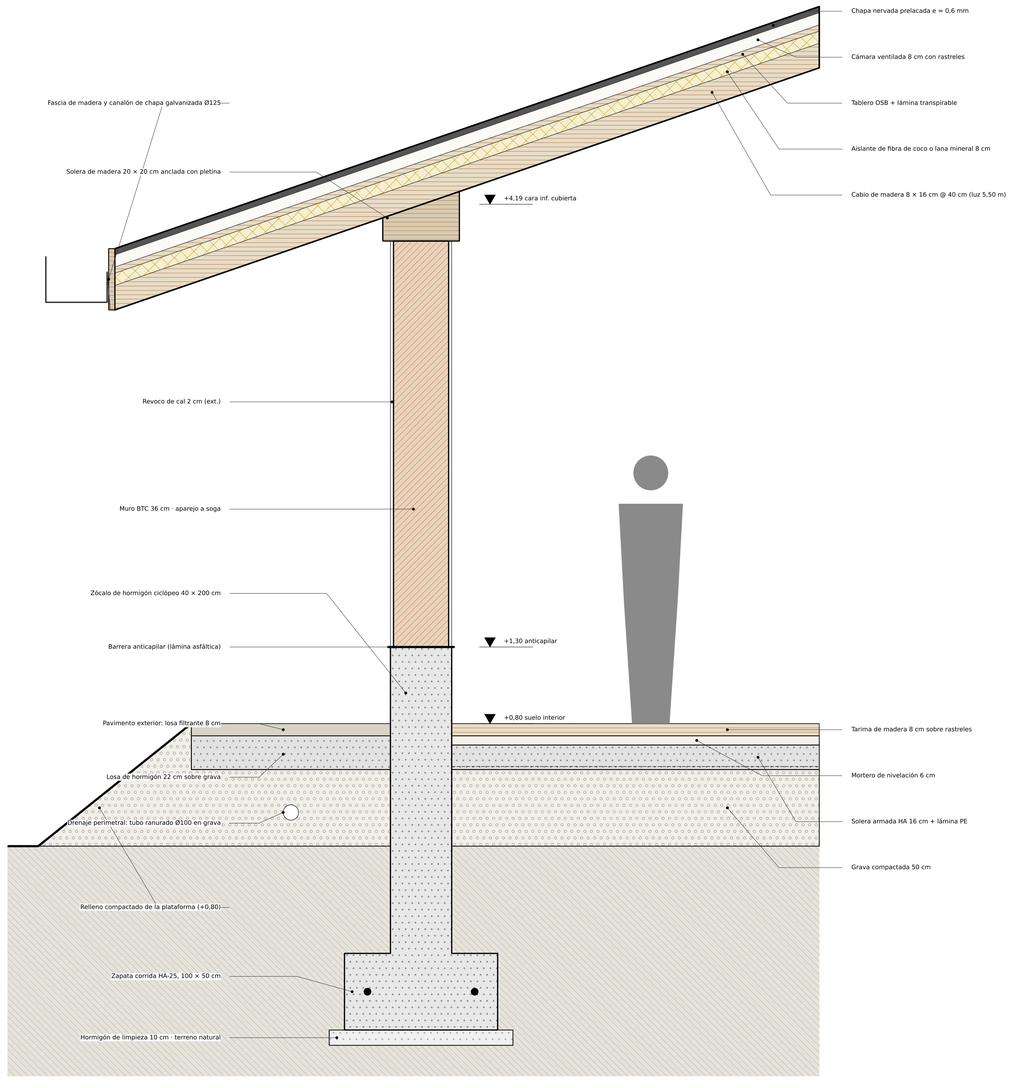

F2 · ENCUENTRO ENTRE CUBIERTAS (BANDA DE EXTRACCIÓN)

E 1:20

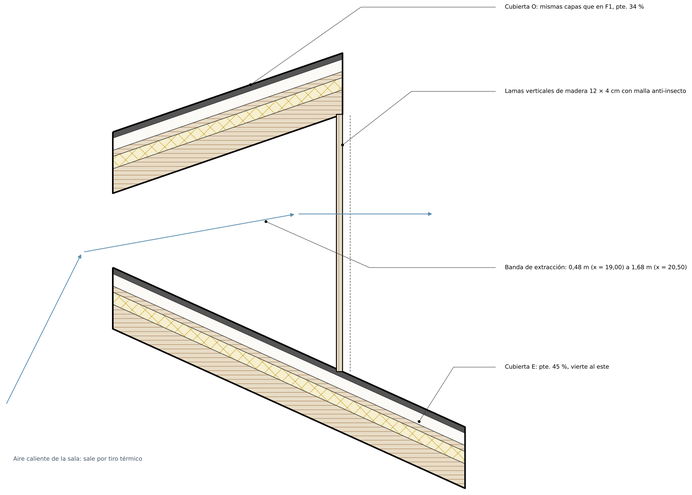

CASO_012 · PROPUESTA C — Anteproyecto

Detalle constructivo: sección de fachada oeste de la sala

Escala 1:20

D01