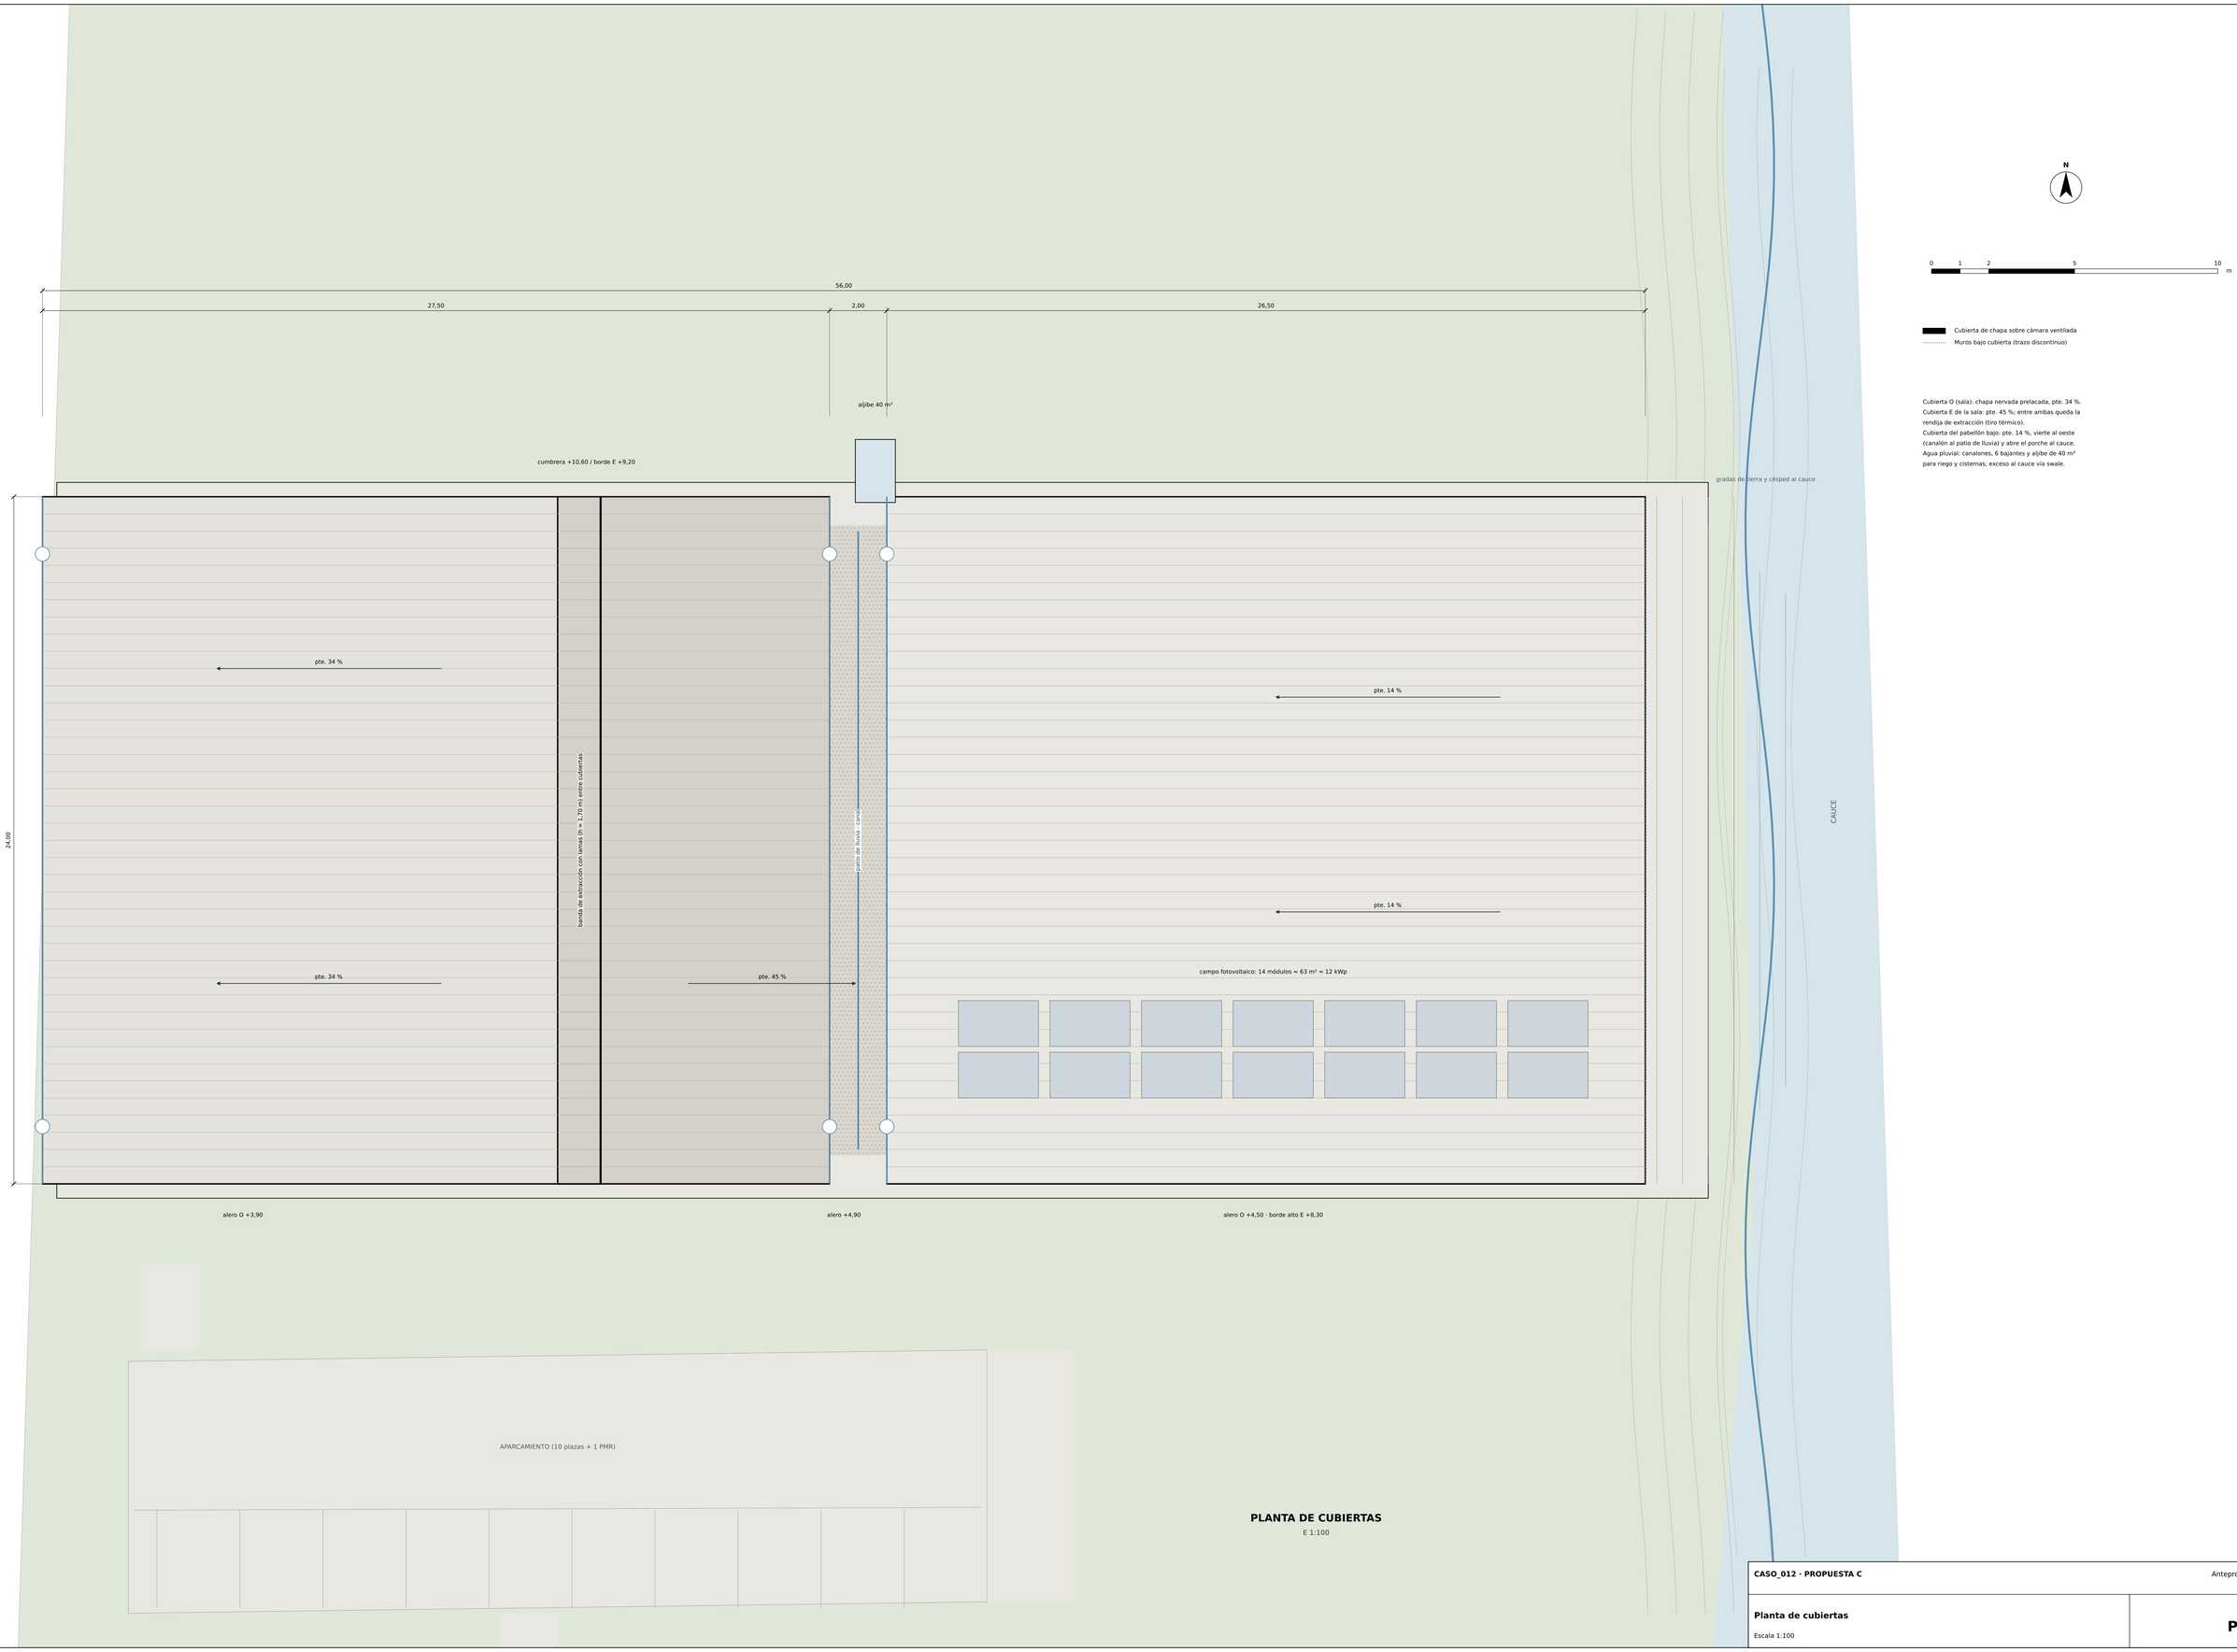


Cubierta O (sala): chapa nervada prelacada, pte. 34 %.
Cubierta E de la sala: pte. 45 %; entre ambas queda la rendija de extracción (tiro térmico).
Cubierta del pabellón bajo: pte. 14 %, vierte al oeste (canalón al patio de lluvia) y abre el porche al cauce.
Agua pluvial: canalones, 6 bajantes y aljibe de 40 m³ para riego y cisternas; exceso al cauce vía swale.

PLANTA DE CUBIERTAS
E 1:100

CASO_012 · PROPUESTA C — Anteproyecto

Planta de cubiertas
Escala 1:100

P02