
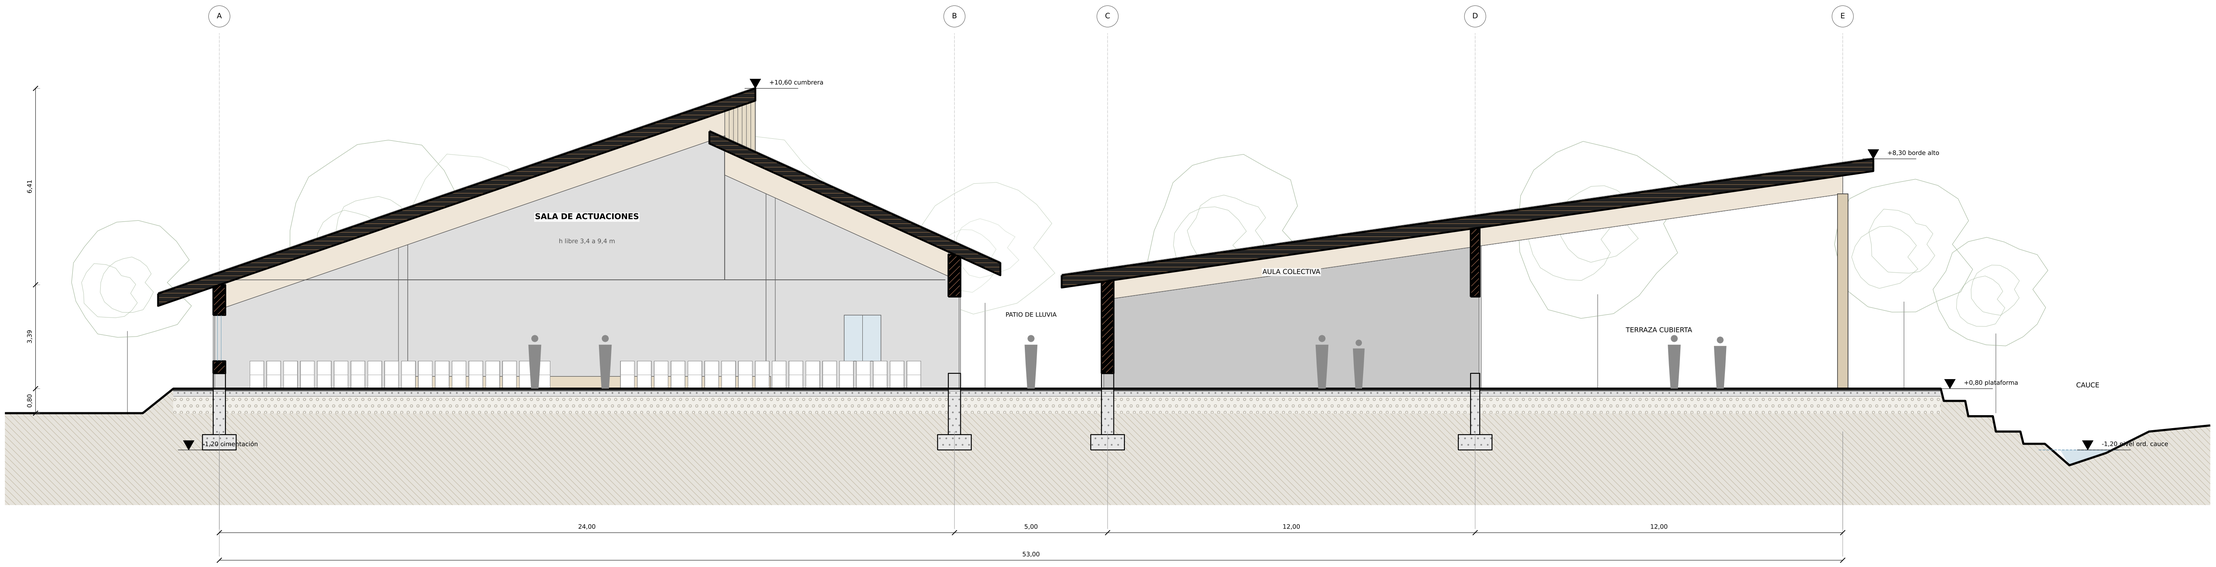


SECCIÓN A-A'

E 1:100

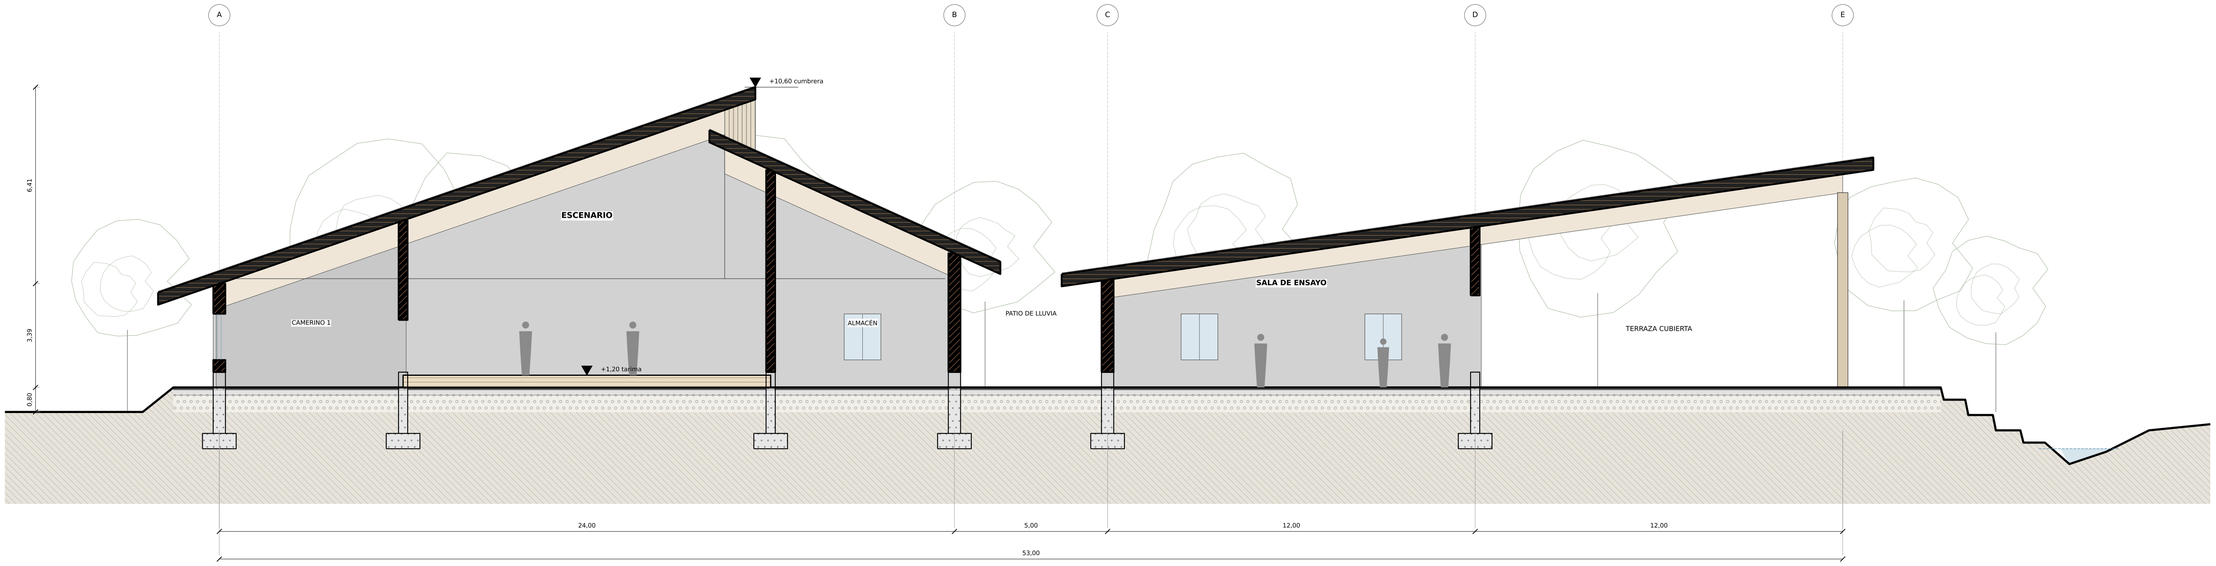

SECCIÓN B-B'

E 1:100

LEYENDA DE MATERIALES EN CORTE

- Muro de bloque de tierra comprimida (BTC) estabilizada, e=40 cm
- Hormigón ciclópeo / armado (zapata y zócalo)
- Relleno compactado de grava (plataforma)
- Madera laminada y tarima; cubierta de cabios sobre cámara ventilada
- Terreno natural
- Lamas de madera (banda de extracción)
- Agua / nivel ordinario del cauce

Plataforma de grava compactada y solera a +0,80 sobre el terreno (±0,00): cota provisional, pendiente del estudio de inundabilidad. Zapatas corridas a -1,20; zócalo de hormigón hasta +1,30. Cubiertas de chapa sobre cámara ventilada, e = 0,40 m. Entre la cubierta O (34 %) y la E (45 %) queda una banda de lamas de 1,70 m para extracción por tiro térmico. Cerchas de madera laminada cada 5,50 m (en proyección), con tirante de acero a +4,35. Las cotas se dan en metros. Secciones por y = 31,00 (A-A') y y = 40,00 (B-B'), mirando al norte.

CASO_012 · PROPUESTA C — Anteproyecto

Secciones longitudinales A-A' y B-B'

Escala 1:100

S01