
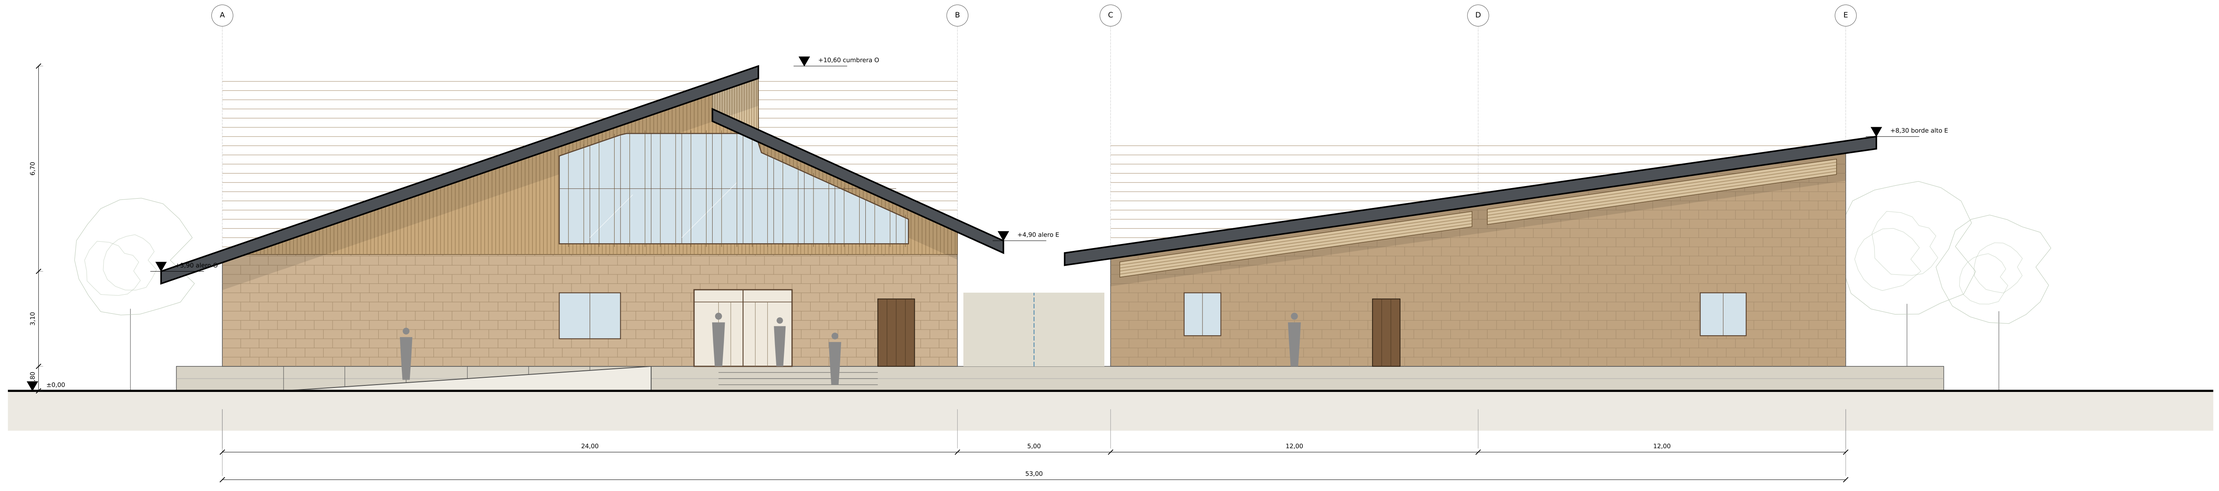



ALZADO SUR

E 1:100

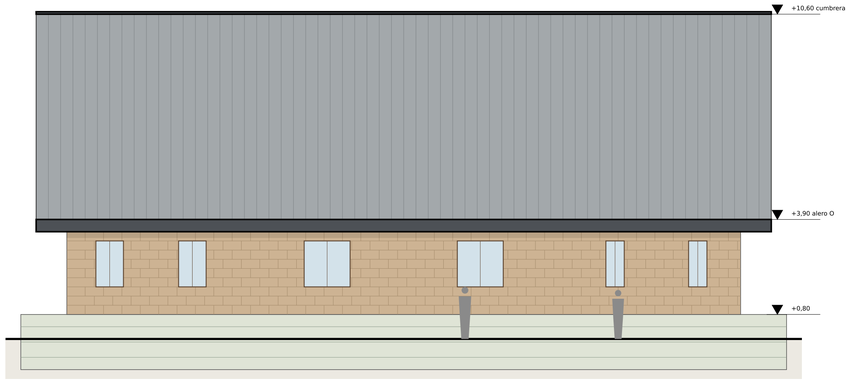

ALZADO OESTE

E 1:100

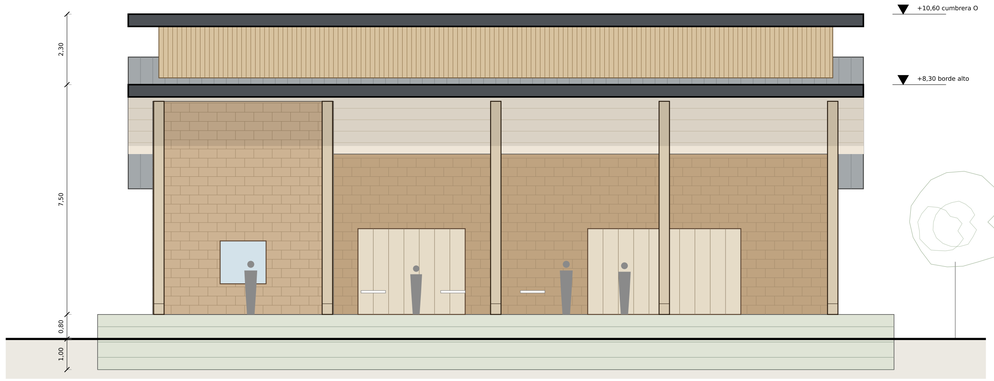

ALZADO ESTE (HACIA EL CAUCE)

E 1:100

MATERIALES Y ACABADOS DE FACHADA

- Muro de bloque de tierra comprimida (BTC) con 6 % de cal-cemento, aparejo a soga, color natural de la tierra del lugar
- Lamas verticales de madera tratada (12 × 4 cm, separación 4 cm) en los gabletes: filtran el sol y dejan pasar el aire
- Carpintería de madera con vidrio; en el gablete sur, brise-soleil de lamas verticales delante del acristalamiento
- Cubierta de chapa nervada prelacada gris grafito sobre cámara ventilada; fascia de 40 cm
- Pilares de madera laminada 35 × 35 cm en el porche hacia el cauce
- Zócalo de hormigón visto y plataforma elevada a +0,80; gradas de tierra y césped hacia el cauce

Estrategia de envolvente: macizo de tierra con poco hueco y fuerte inercia en los lados sur, oeste y norte; gablete sur acristalado y protegido por lamas; lado este (cauce) abierto bajo el porche, con plegables de lamas que se abren al paisaje. Sin edificación vecina: contexto en gris claro.

CASO_012 · PROPUESTA C	Anteproyecto
Alzados sur, este y oeste Escala 1:100	**S03**