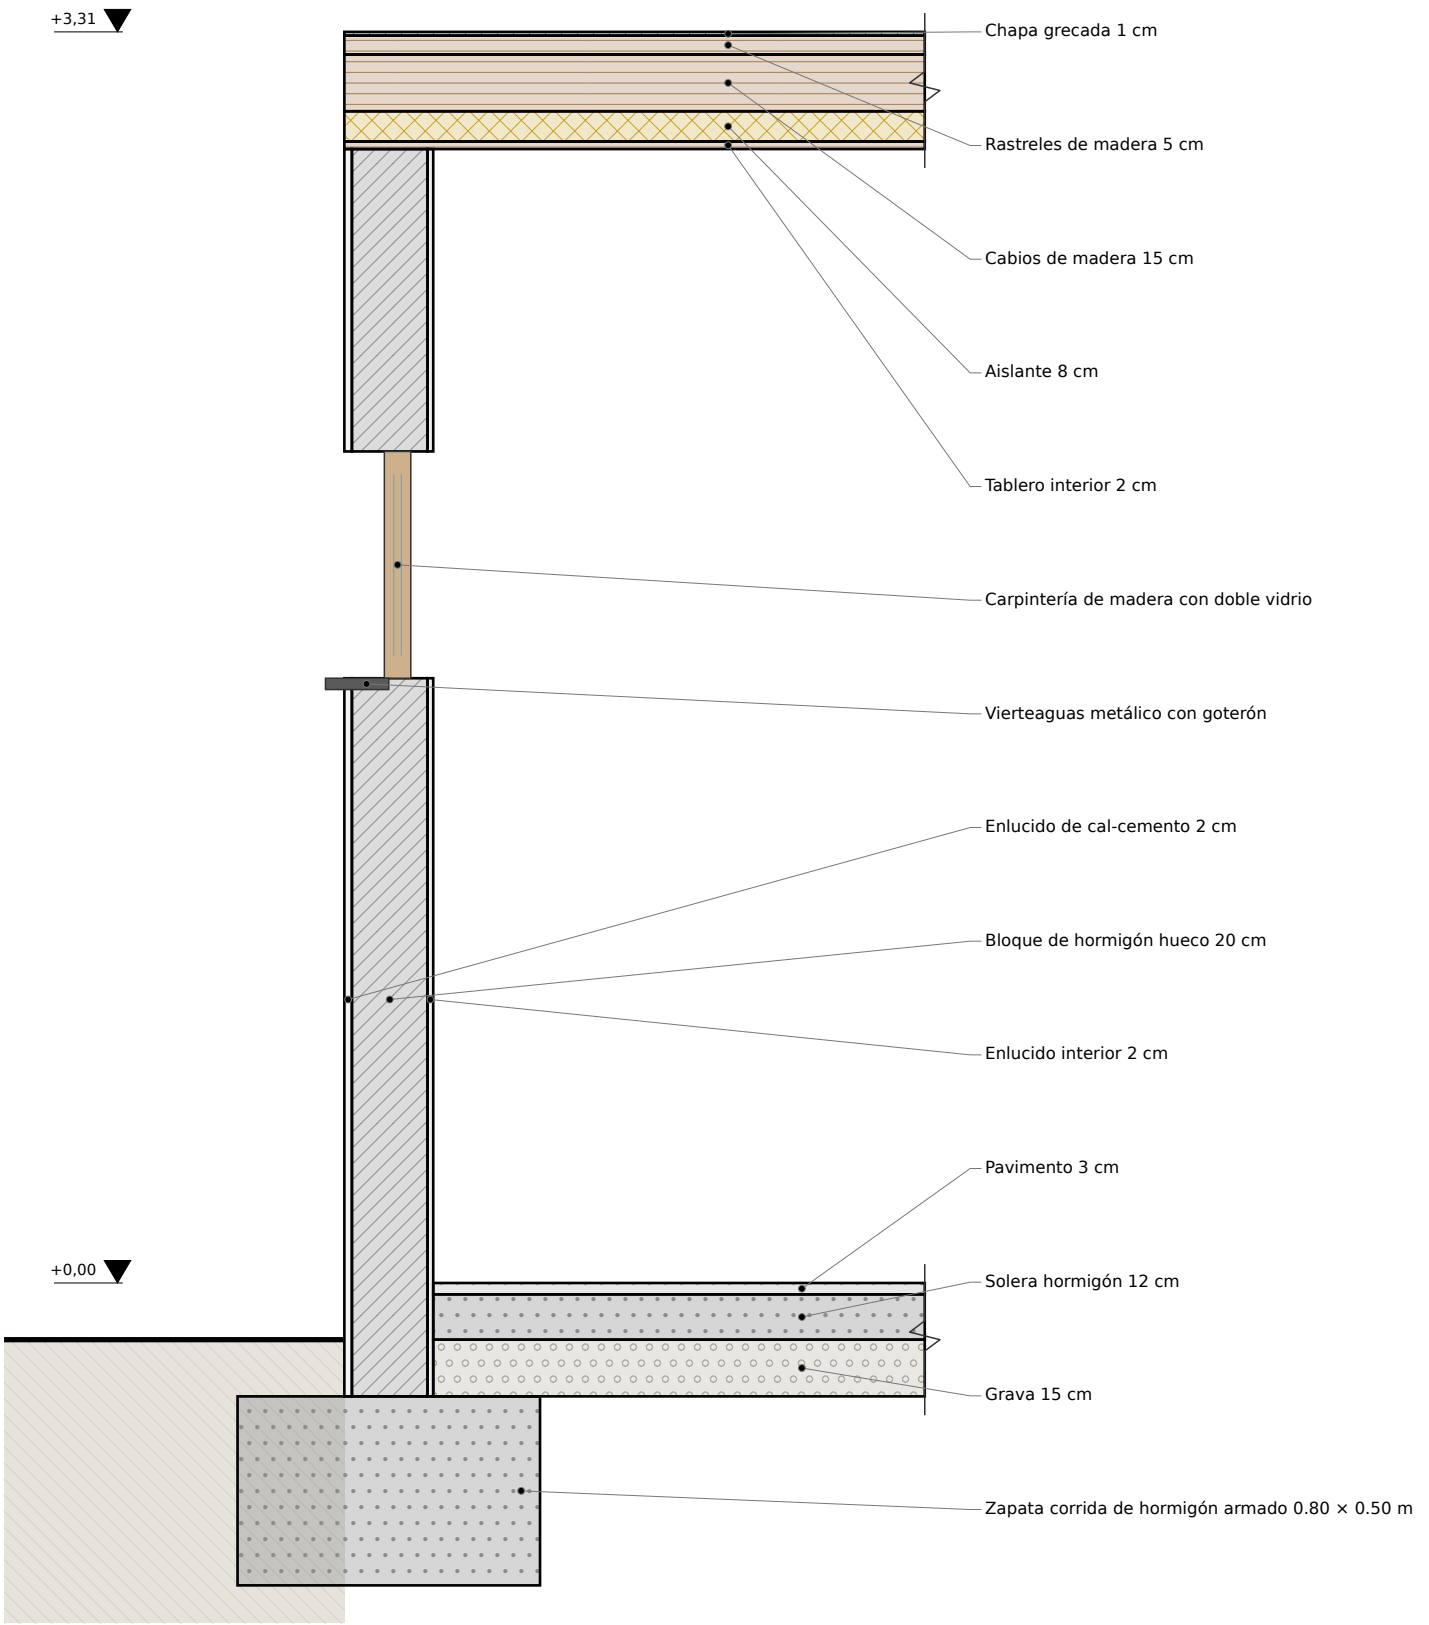


DETALLE CONSTRUCTIVO

E 1:20

CASO_013 · PROPUESTA B	E 1:20	**D01**
SECCIÓN CONSTRUCTIVA	Anteproyecto	