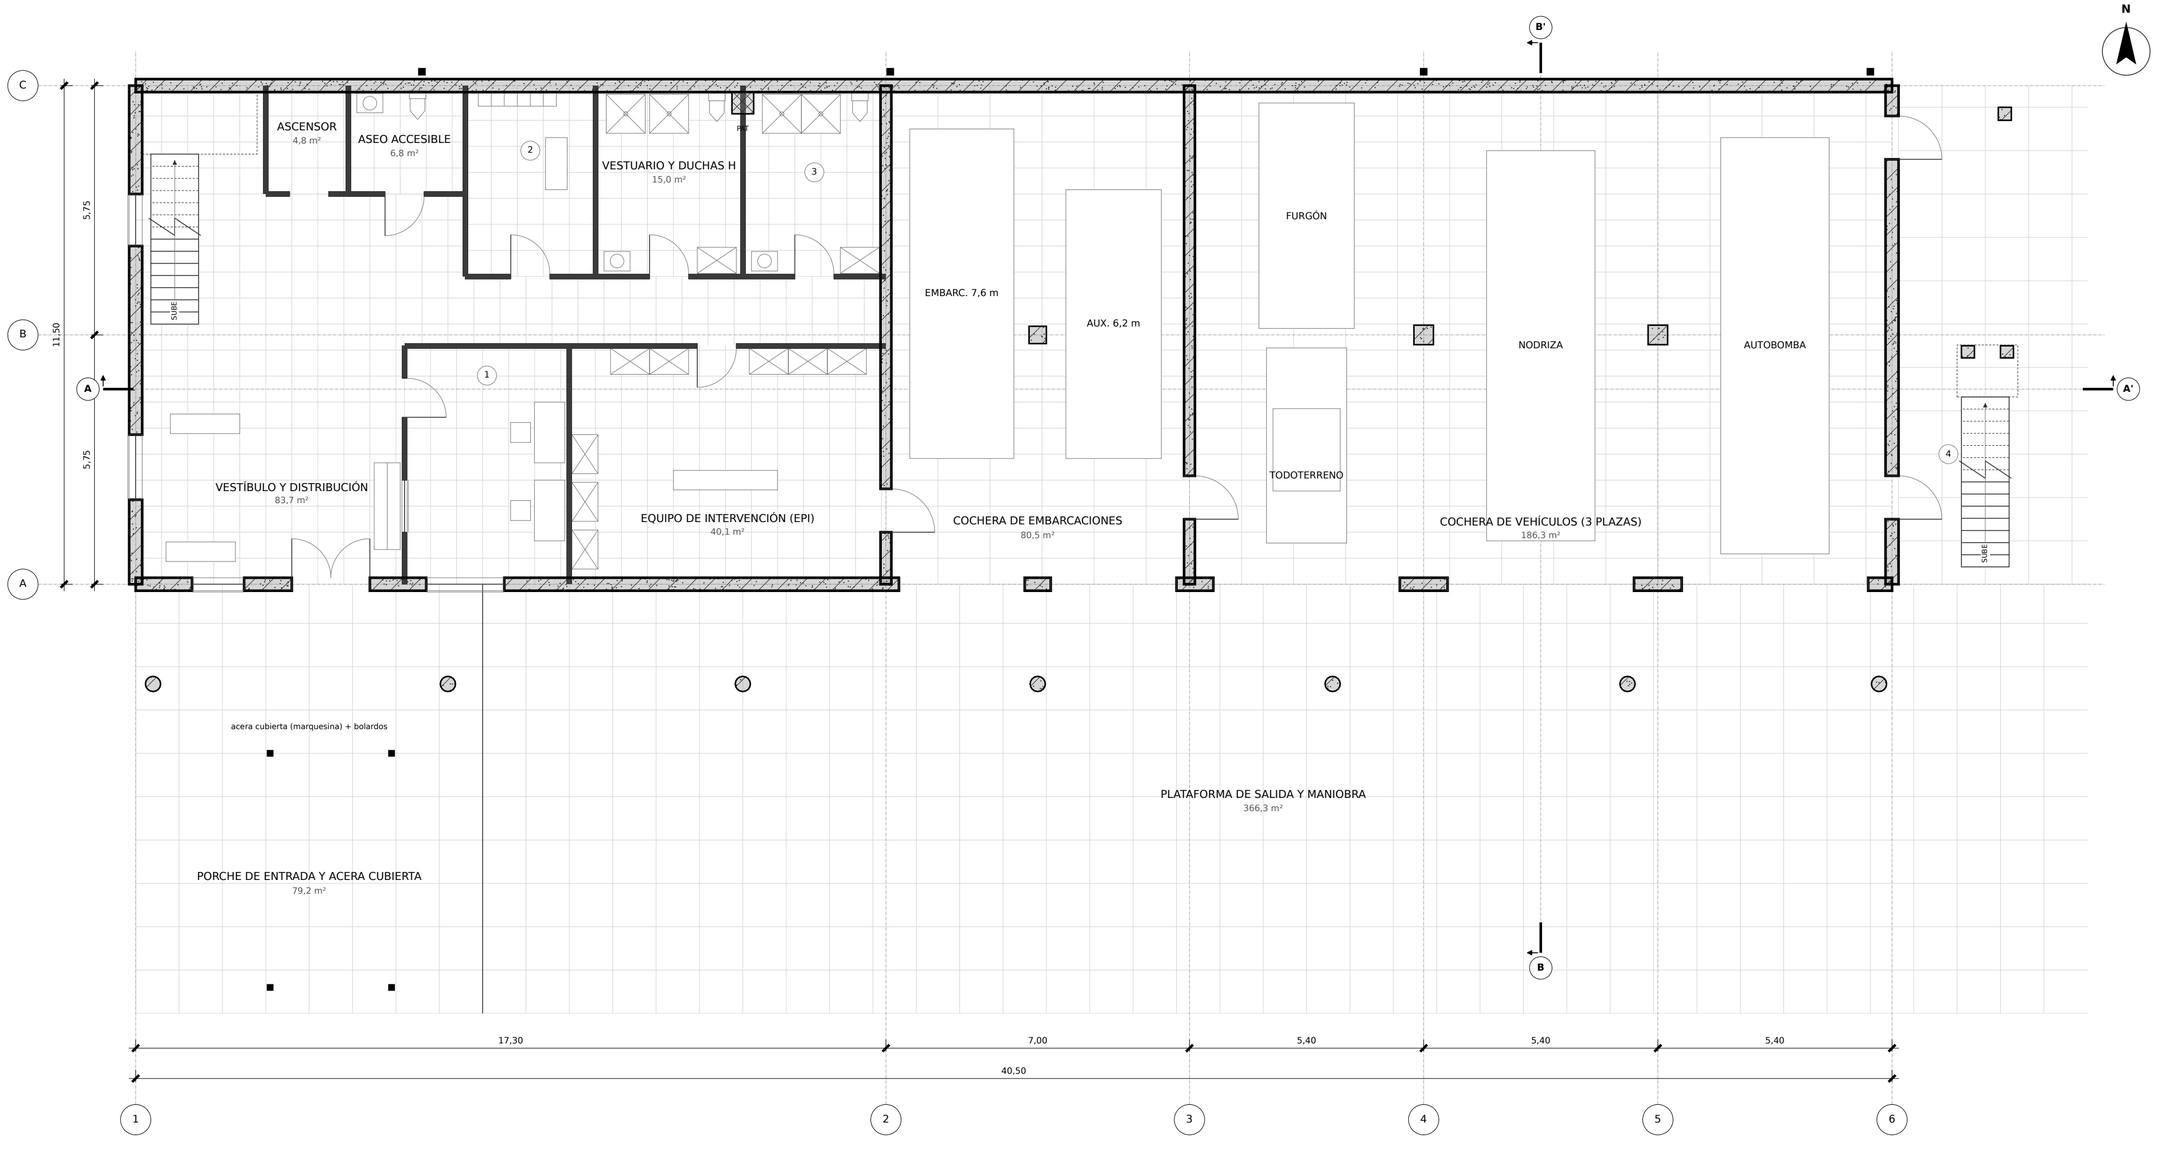


PLANTA BAJA

E 1:100

m
0 1 2 5 10

1 Control y comunicaciones · 20,9 m²
2 Limpieza e instalaciones · 13,2 m²
3 Vestuario y duchas M · 14,5 m²
4 Patio este y escalera exterior de evacuación · 50,0 m²

CASO_014 · PROPUESTA A	E 1:100	**P01**
PLANTA BAJA	Anteproyecto	