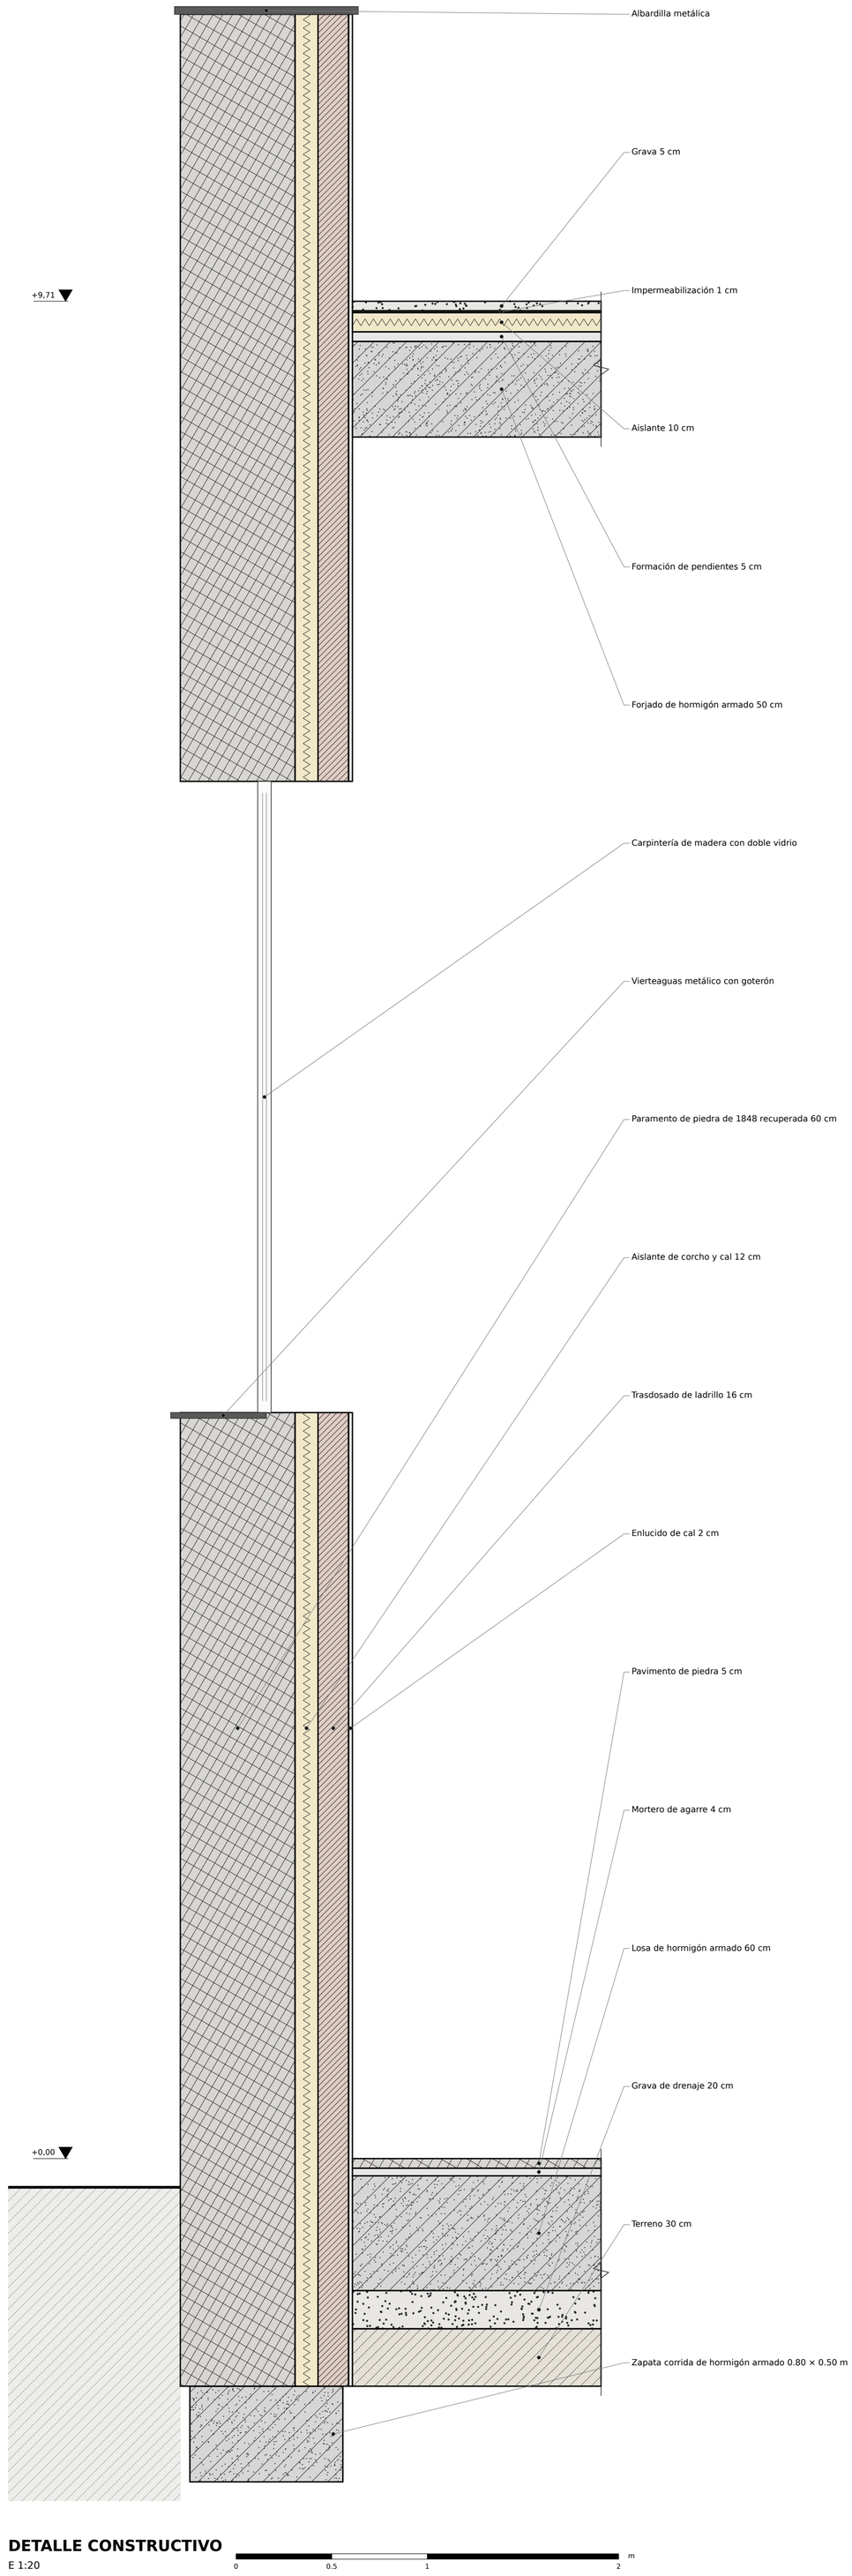


DETALLE CONSTRUCTIVO

E 1:20

0 0.5 1 2 m

CASO_019 · PROPUESTA A	E 1:20	**D01**
SECCIÓN CONSTRUCTIVA DE FACHADA DEL CINTURÓN	Anteproyecto	