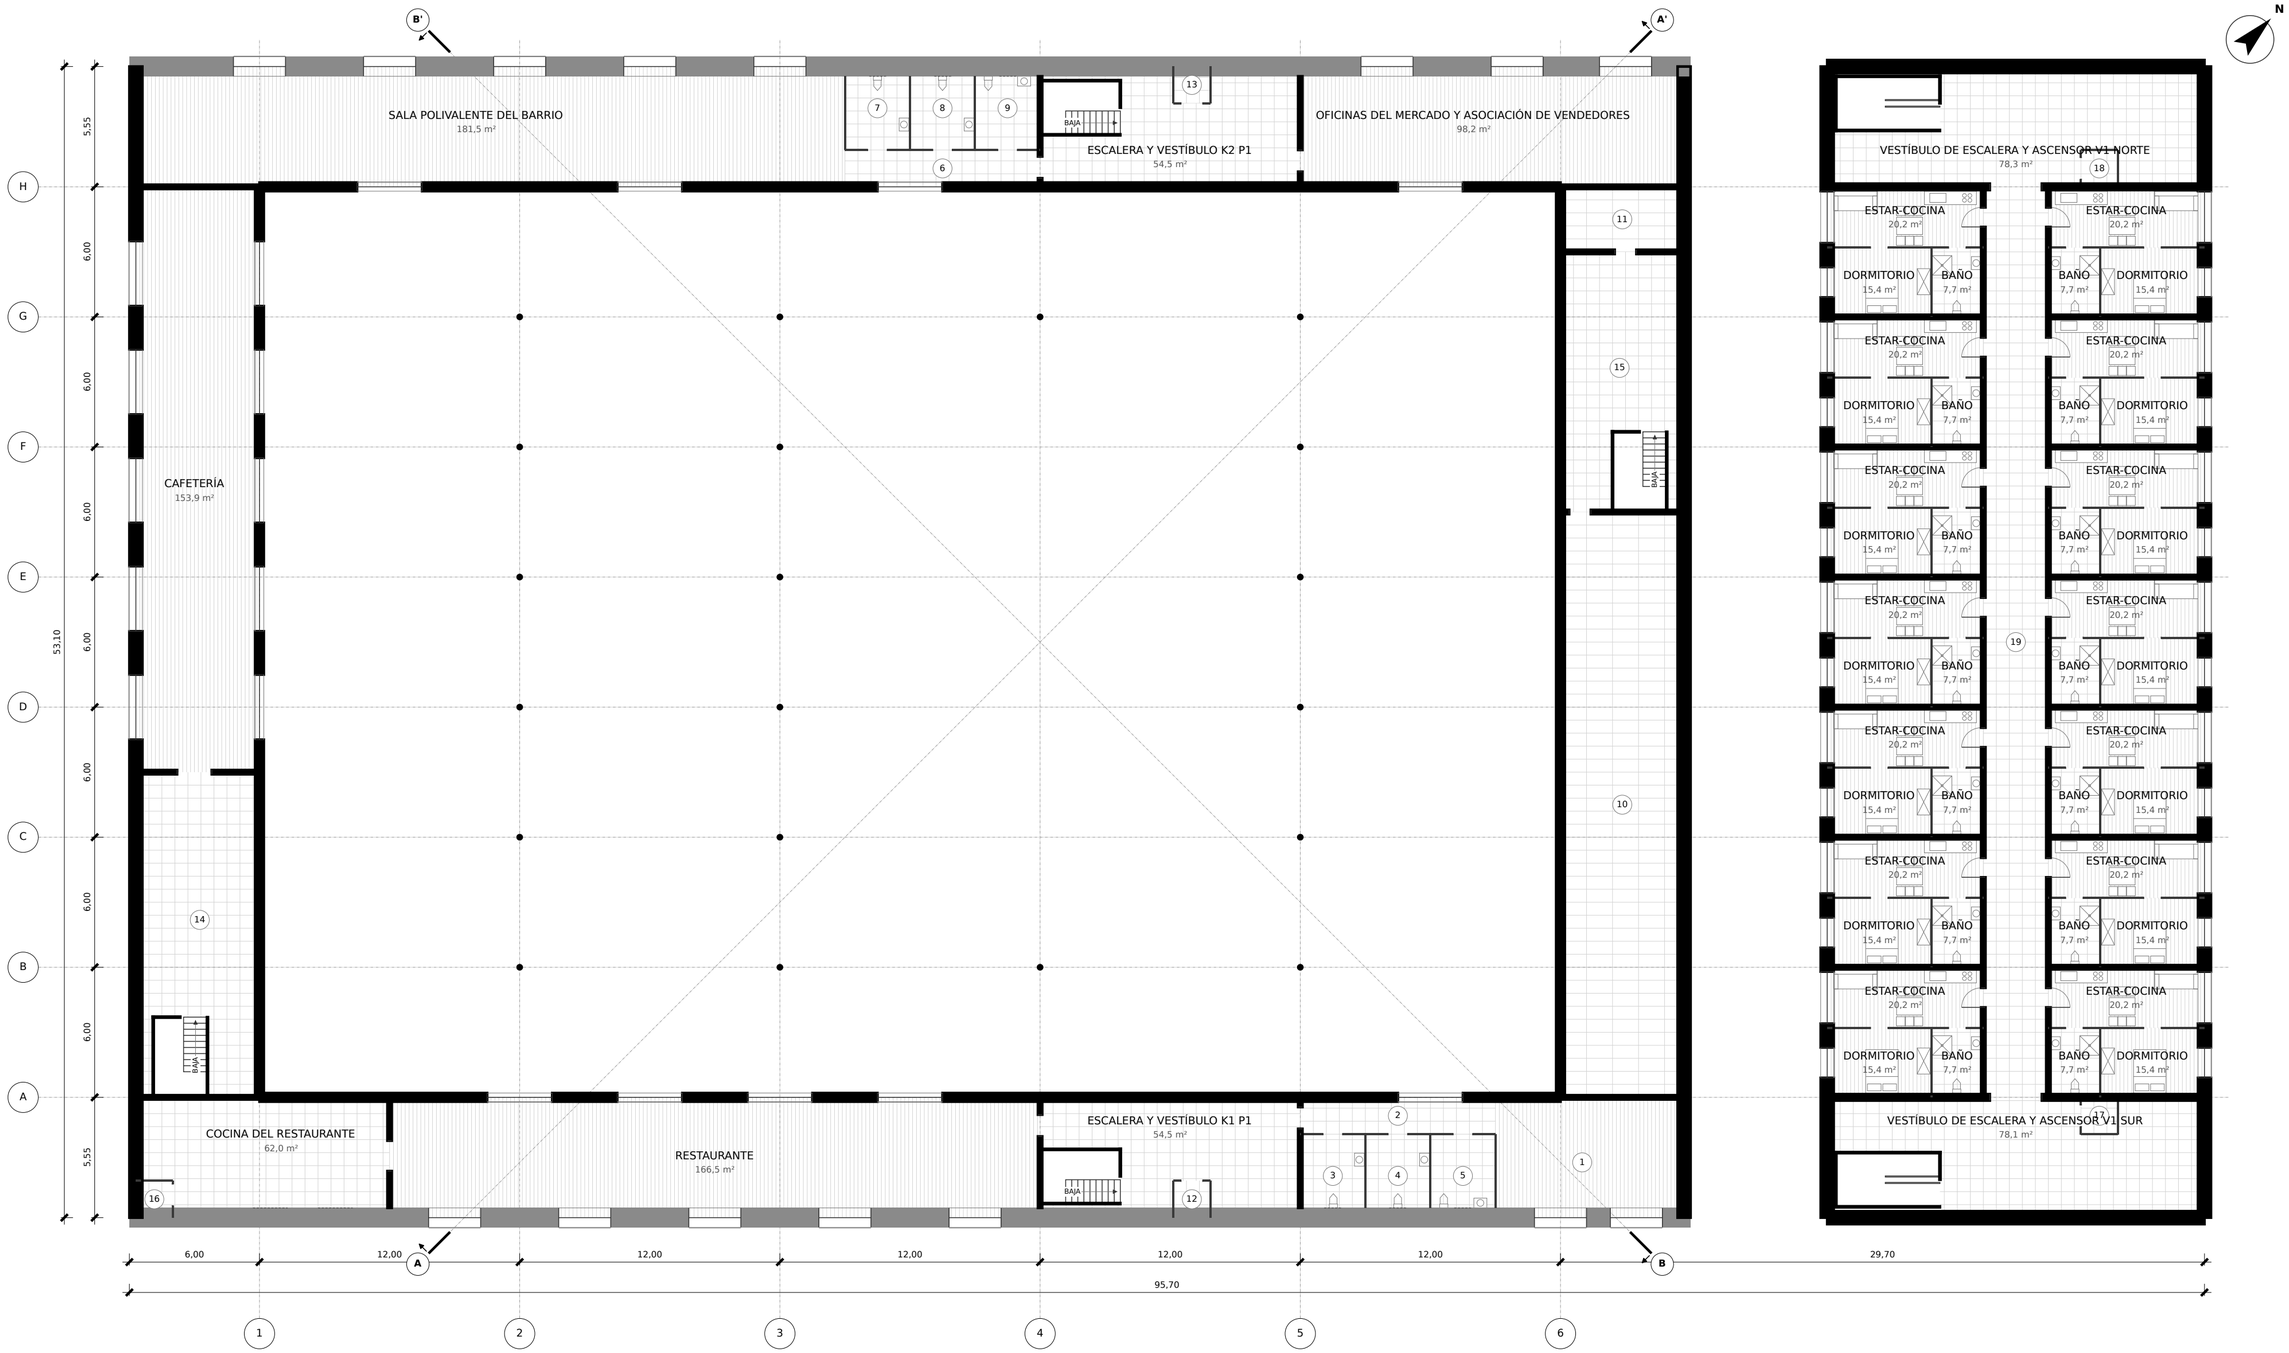


PLANTA PRIMERA

E 1:200

0 2 5 10 20 m

Obra nueva
Existente que se conserva
Existente que se demuele

1 Comedor privado del restaurante · 48,3 m²
2 Vestíbulo de servicios P1 sur · 15,3 m²
3 Aseo P1 sur 1 · 11,6 m²
4 Aseo P1 sur 2 · 11,6 m²
5 Aseo accesible P1 sur · 11,5 m²
6 Vestíbulo de servicios P1 norte · 15,3 m²
7 Aseo P1 norte 1 · 11,6 m²
8 Aseo P1 norte 2 · 11,5 m²
9 Aseo accesible P1 norte · 11,6 m²
10 Instalaciones de climatización · 153,9 m²
11 Instalaciones eléctricas y comunicaciones · 17,1 m²
12 Ascensor K1 · 2,9 m²
13 Ascensor K2 · 2,9 m²
14 Escalera y vestíbulo K3 P1 · 76,2 m²
15 Escalera y vestíbulo K4 P1 · 59,2 m²
16 Ascensor montacargas · 2,9 m²
17 Ascensor viviendas sur · 2,9 m²
18 Ascensor viviendas norte · 2,9 m²
19 Pasillo de acceso a viviendas · 126,0 m²

CASO_019 · PROPUESTA A

PLANTA PRIMERA · RESTAURANTE, CAFETERÍA, OFICINAS Y VIVIENDAS

E 1:200

Anteproyecto

P04