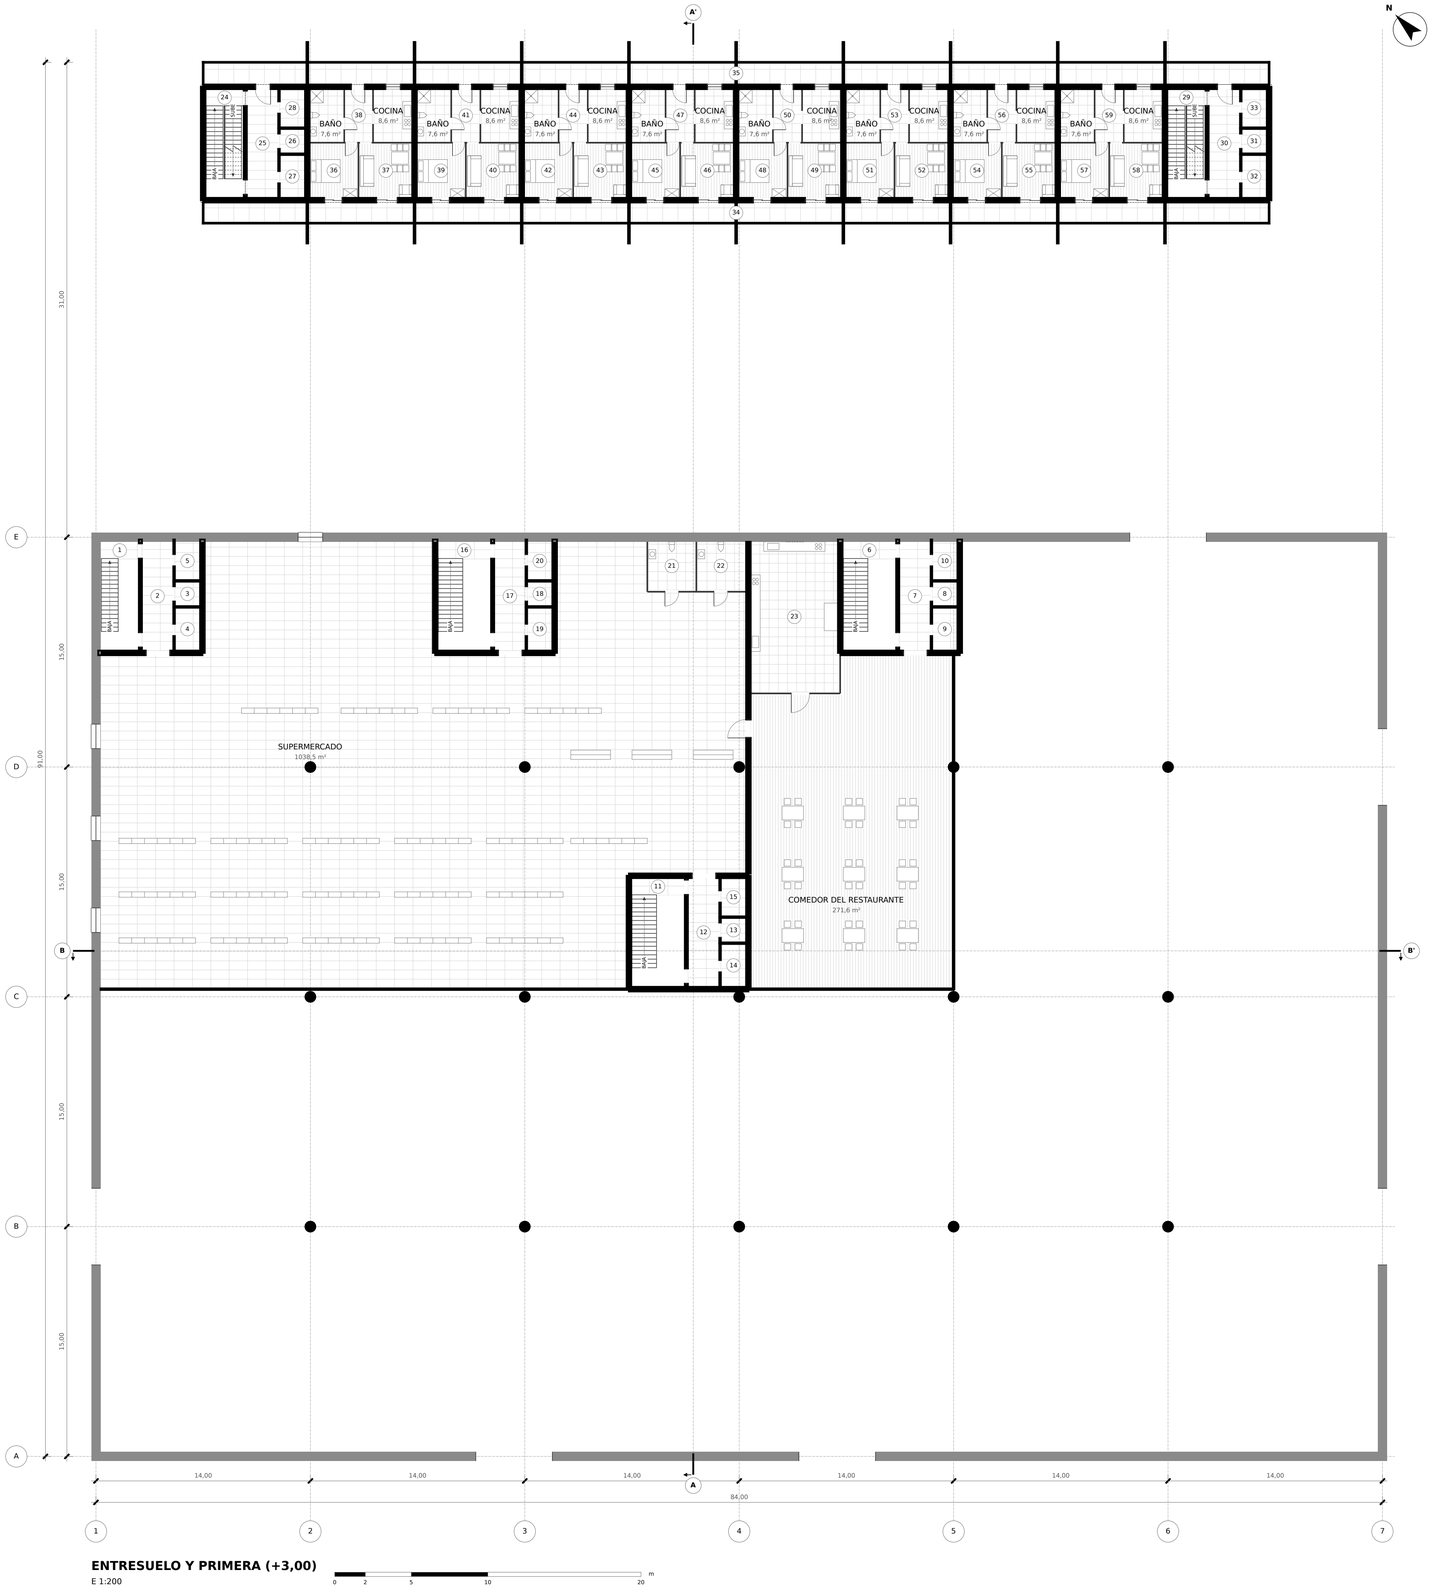


ENTRESUELO Y PRIMERA (+3,00)

E 1:200

0 2 5 10 20 m

- Obra nueva
- Existente que se conserva
- Existente que se demuele

1 Escalera · 2,8 m²
2 Vestíbulo · 14,6 m²
3 Ascensor · 2,6 m²
4 Patinillo de instalaciones · 4,6 m²
5 Patinillo de instalaciones · 4,1 m²
6 Escalera · 3,9 m²
7 Vestíbulo · 14,6 m²
8 Ascensor · 2,6 m²
9 Patinillo de instalaciones · 4,6 m²
10 Patinillo de instalaciones · 4,1 m²
11 Escalera · 3,9 m²
12 Vestíbulo · 14,6 m²
13 Ascensor · 2,6 m²
14 Patinillo de instalaciones · 4,6 m²
15 Patinillo de instalaciones · 4,1 m²
16 Escalera · 3,9 m²
17 Vestíbulo · 14,6 m²
18 Ascensor · 2,6 m²
19 Patinillo de instalaciones · 4,6 m²
20 Patinillo de instalaciones · 4,1 m²
21 Aseo accesible · 9,4 m²
22 Aseo accesible · 9,4 m²
23 Cocina del restaurante · 55,9 m²
24 Escalera · 2,8 m²
25 Vestíbulo · 14,6 m²
26 Ascensor · 2,6 m²
27 Patinillo de instalaciones · 4,6 m²
28 Patinillo de instalaciones · 4,1 m²
29 Escalera · 2,8 m²
30 Vestíbulo · 14,6 m²
31 Ascensor · 2,6 m²
32 Patinillo de instalaciones · 4,6 m²
33 Patinillo de instalaciones · 4,1 m²
34 Logia · 94,0 m²
35 Galería · 100,9 m²
36 Dormitorio · 11,2 m²
37 Estar-comedor · 12,2 m²
38 Vestíbulo · 6,2 m²
39 Dormitorio · 11,2 m²
40 Estar-comedor · 12,2 m²
41 Vestíbulo · 6,2 m²
42 Dormitorio · 11,2 m²
43 Estar-comedor · 12,2 m²
44 Vestíbulo · 6,2 m²
45 Dormitorio · 11,2 m²
46 Estar-comedor · 12,2 m²
47 Vestíbulo · 6,2 m²
48 Dormitorio · 11,2 m²
49 Estar-comedor · 12,2 m²
50 Vestíbulo · 6,2 m²
51 Dormitorio · 11,2 m²
52 Estar-comedor · 12,2 m²
53 Vestíbulo · 6,2 m²
54 Dormitorio · 11,2 m²
55 Estar-comedor · 12,2 m²
56 Vestíbulo · 6,2 m²
57 Dormitorio · 11,2 m²

CASO_019 · PROPUESTA B

PLANTA PRIMERA Y ENTRESUELO

E 1:200

Anteproyecto

P04