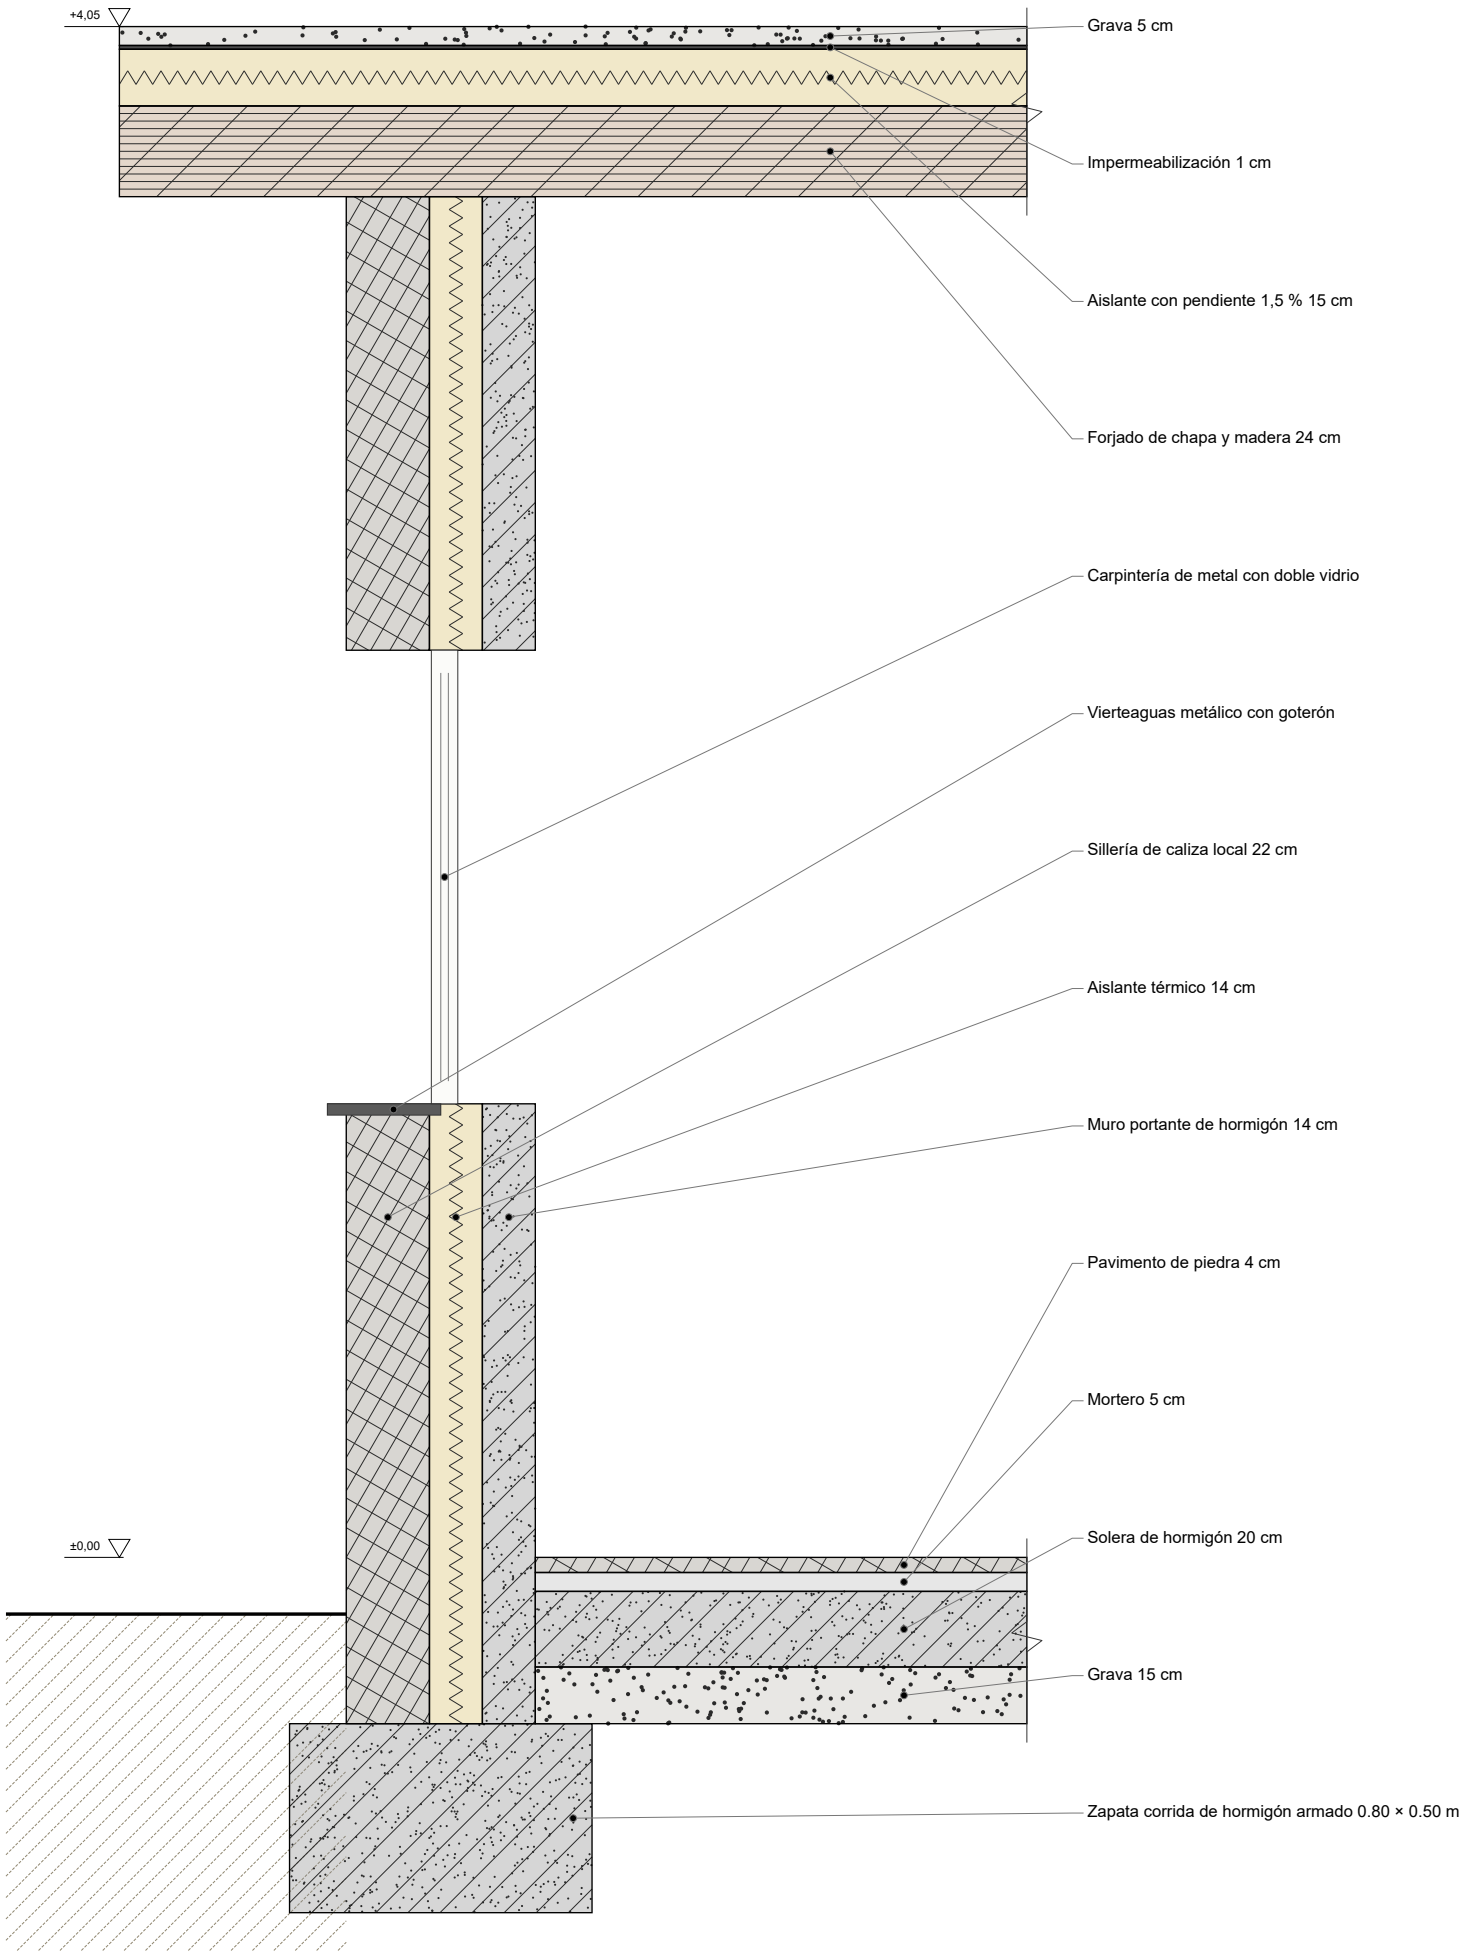


DETALLE CONSTRUCTIVO E 1:20