
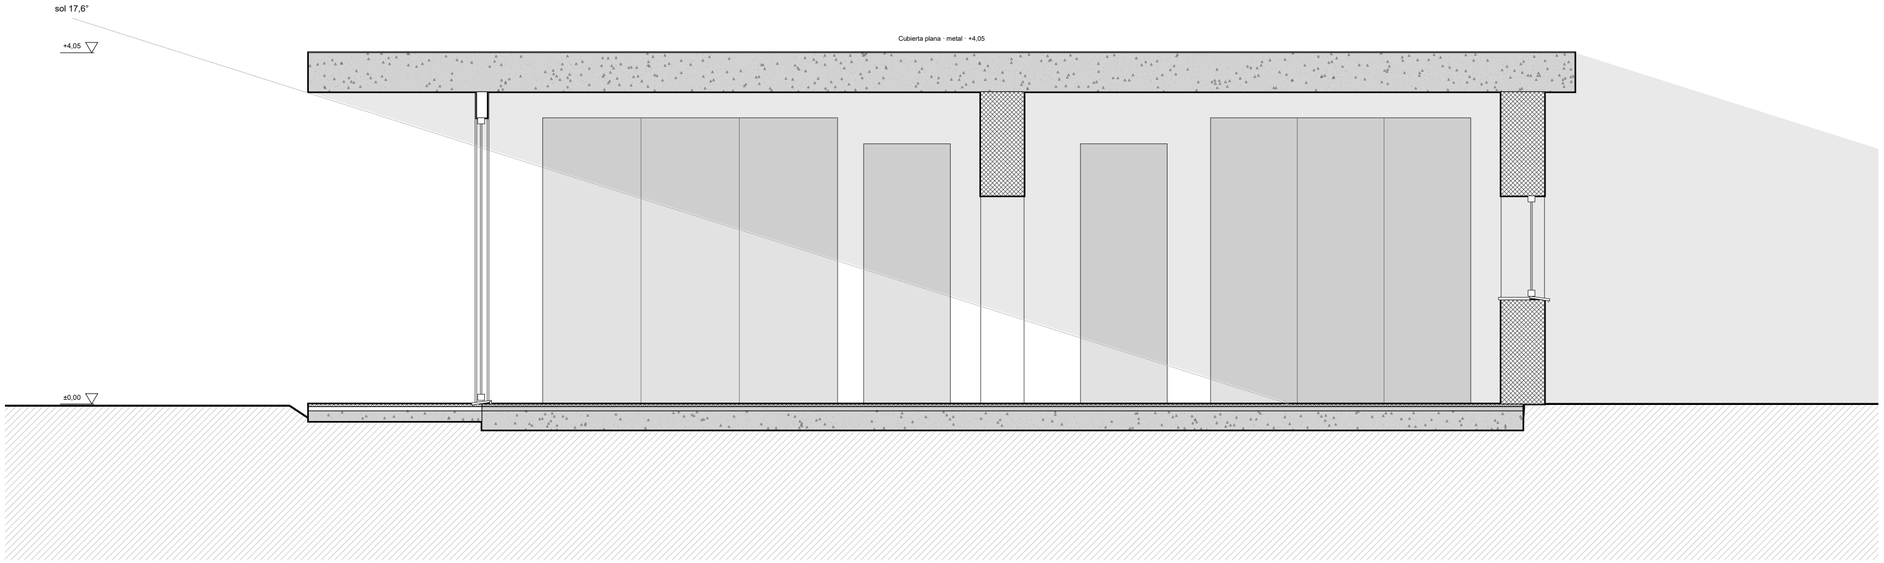


SECCIÓN A-A' E 1:50

0 2,5 5 m

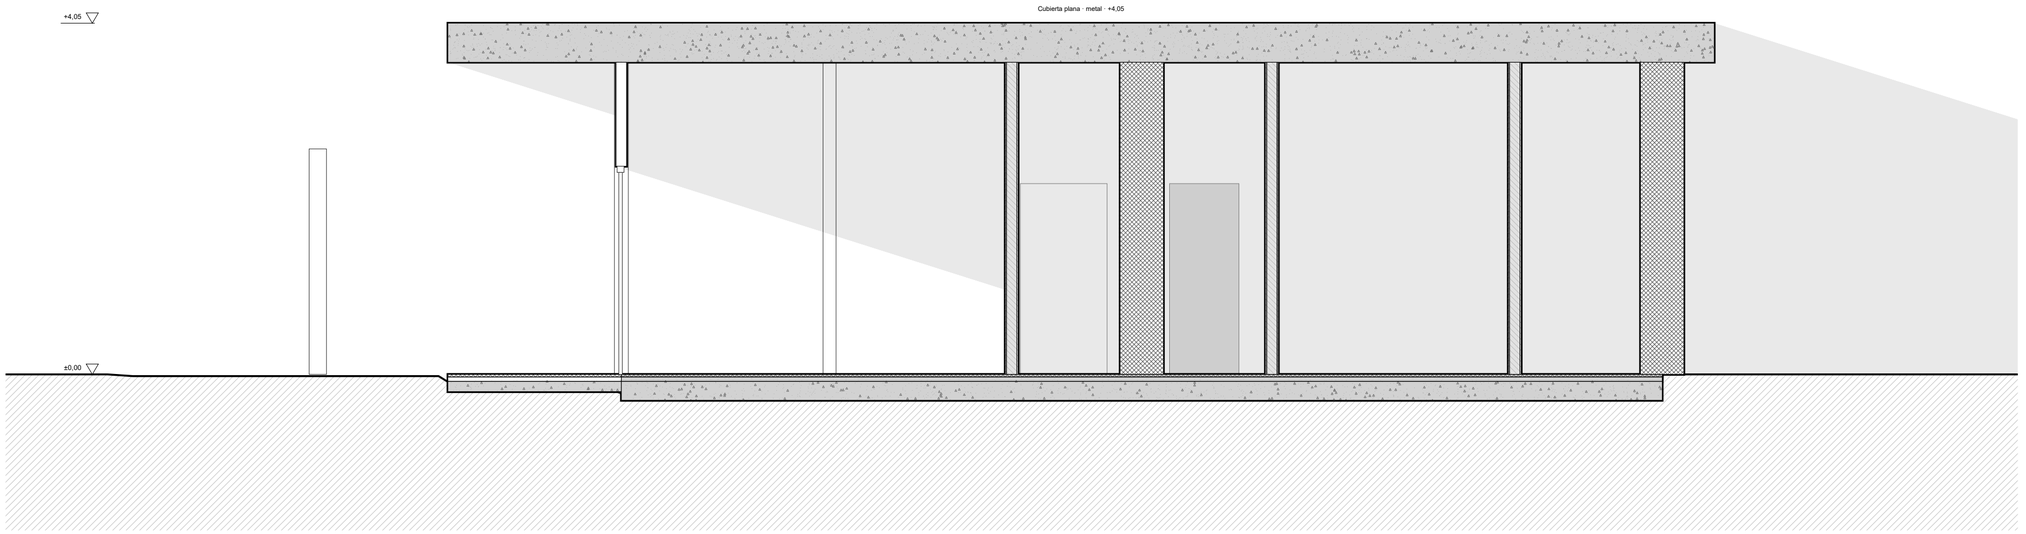

SECCIÓN B-B' E 1:50

0 2,5 5 m

En gris, la sombra con el sol a 17,6° (17,6° en este corte)

- - Rayo de sol: sol 17,6°

En gris, la sombra con el sol a 17,6° (17,6° en este corte)