



SECCIÓN A-A'. SOL DEL 21 DE JUNIO, 16:30 (31,8°)

E 1:100

0 5 10 m

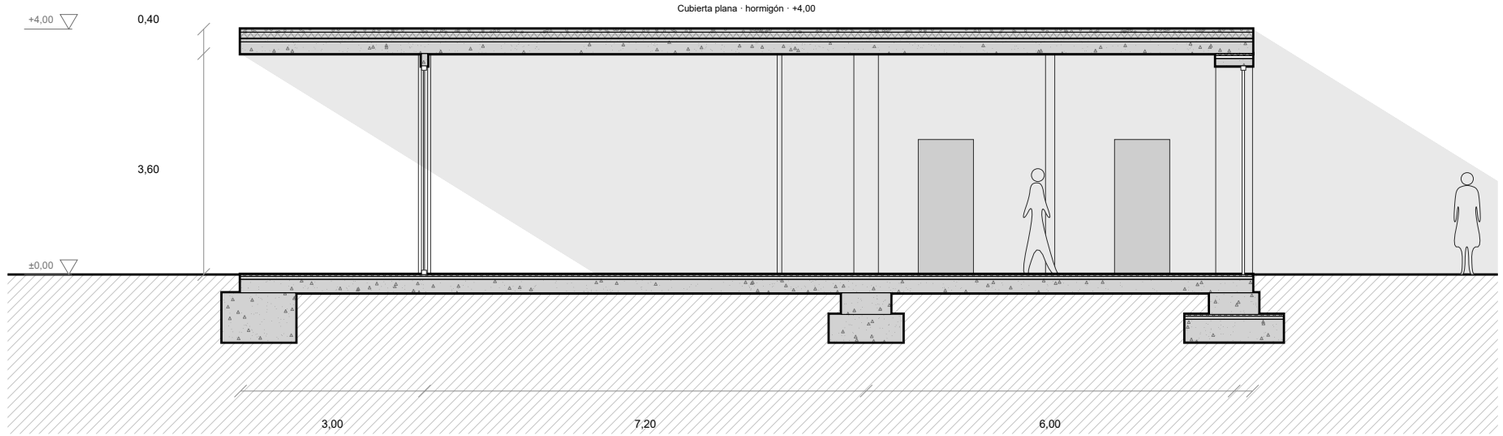

CORTE A-A'

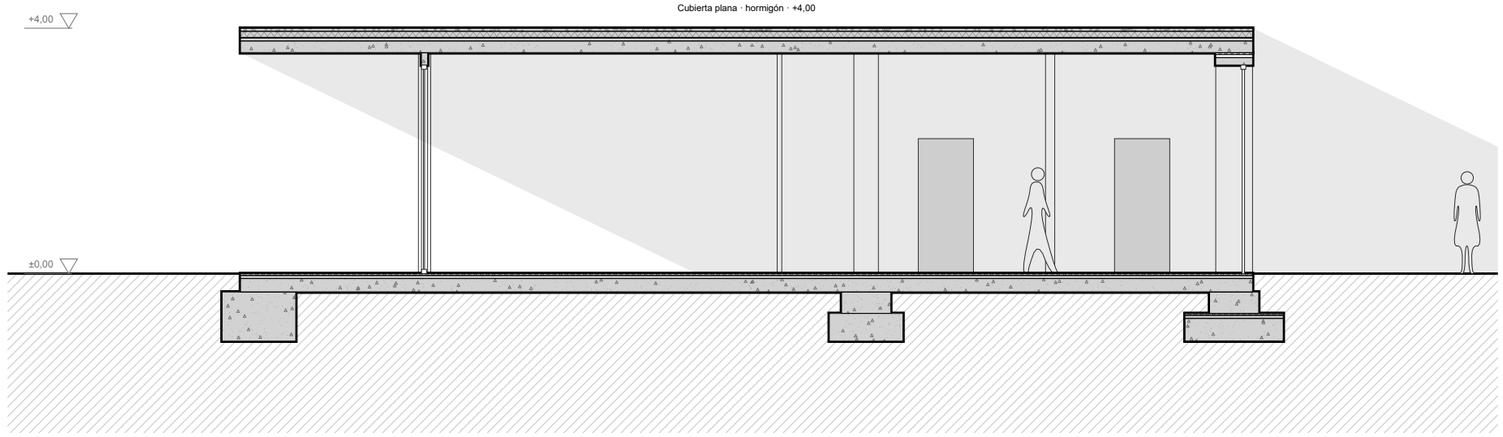

SECCIÓN A-A'. SOL DEL 21 DE DICIEMBRE, 14:00 (12,8°)

E 1:100

0 5 10 m



CORTE A-A'