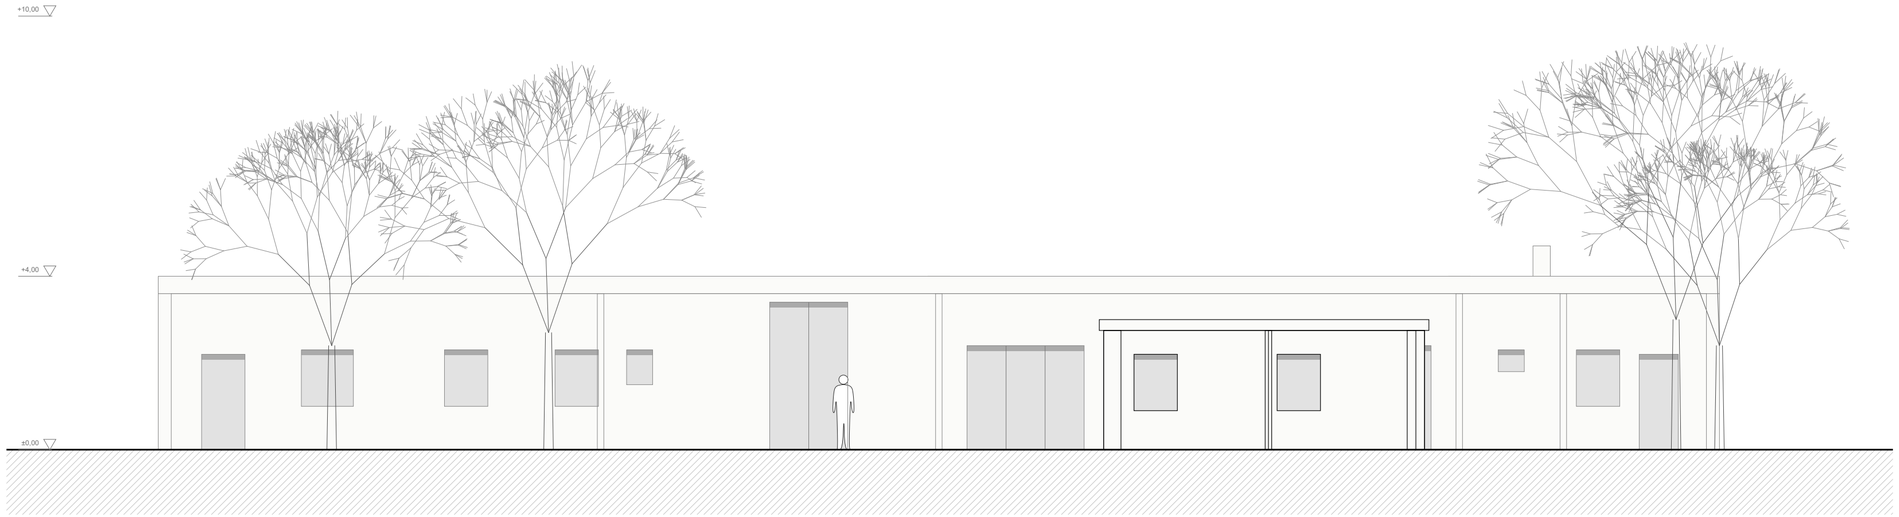



◄ SUR


NORTE ►

ALZADO ESTE, HACIA EL PATIO DE LLEGADA Y LA RUE DE VILLIERS. DELANTE, EL PABELLÓN DEL JARDINERO

E 1:100

0 5 10 m

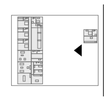

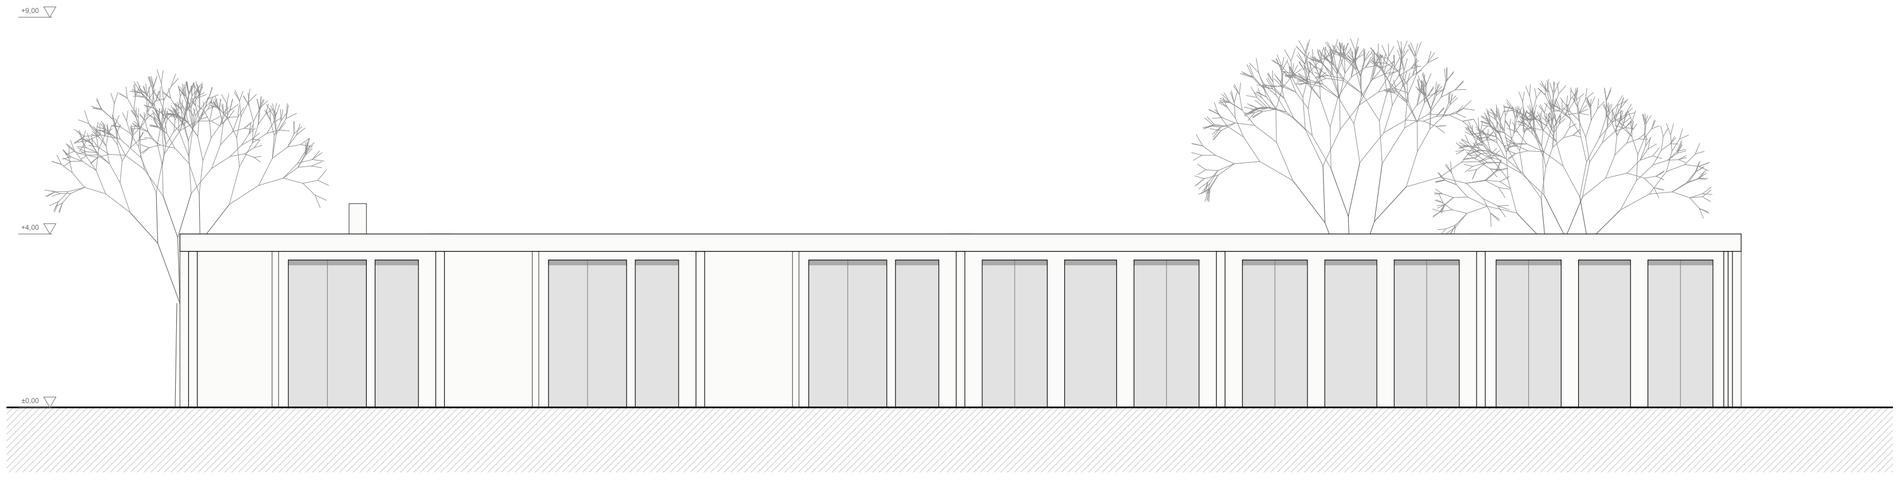

◄ NORTE

SUR ►

ALZADO OESTE, HACIA EL VALLE DEL SENA

E 1:100

0 5 10 m



En gris, la sombra con el sol a 25,0° (53,7° en este corte)