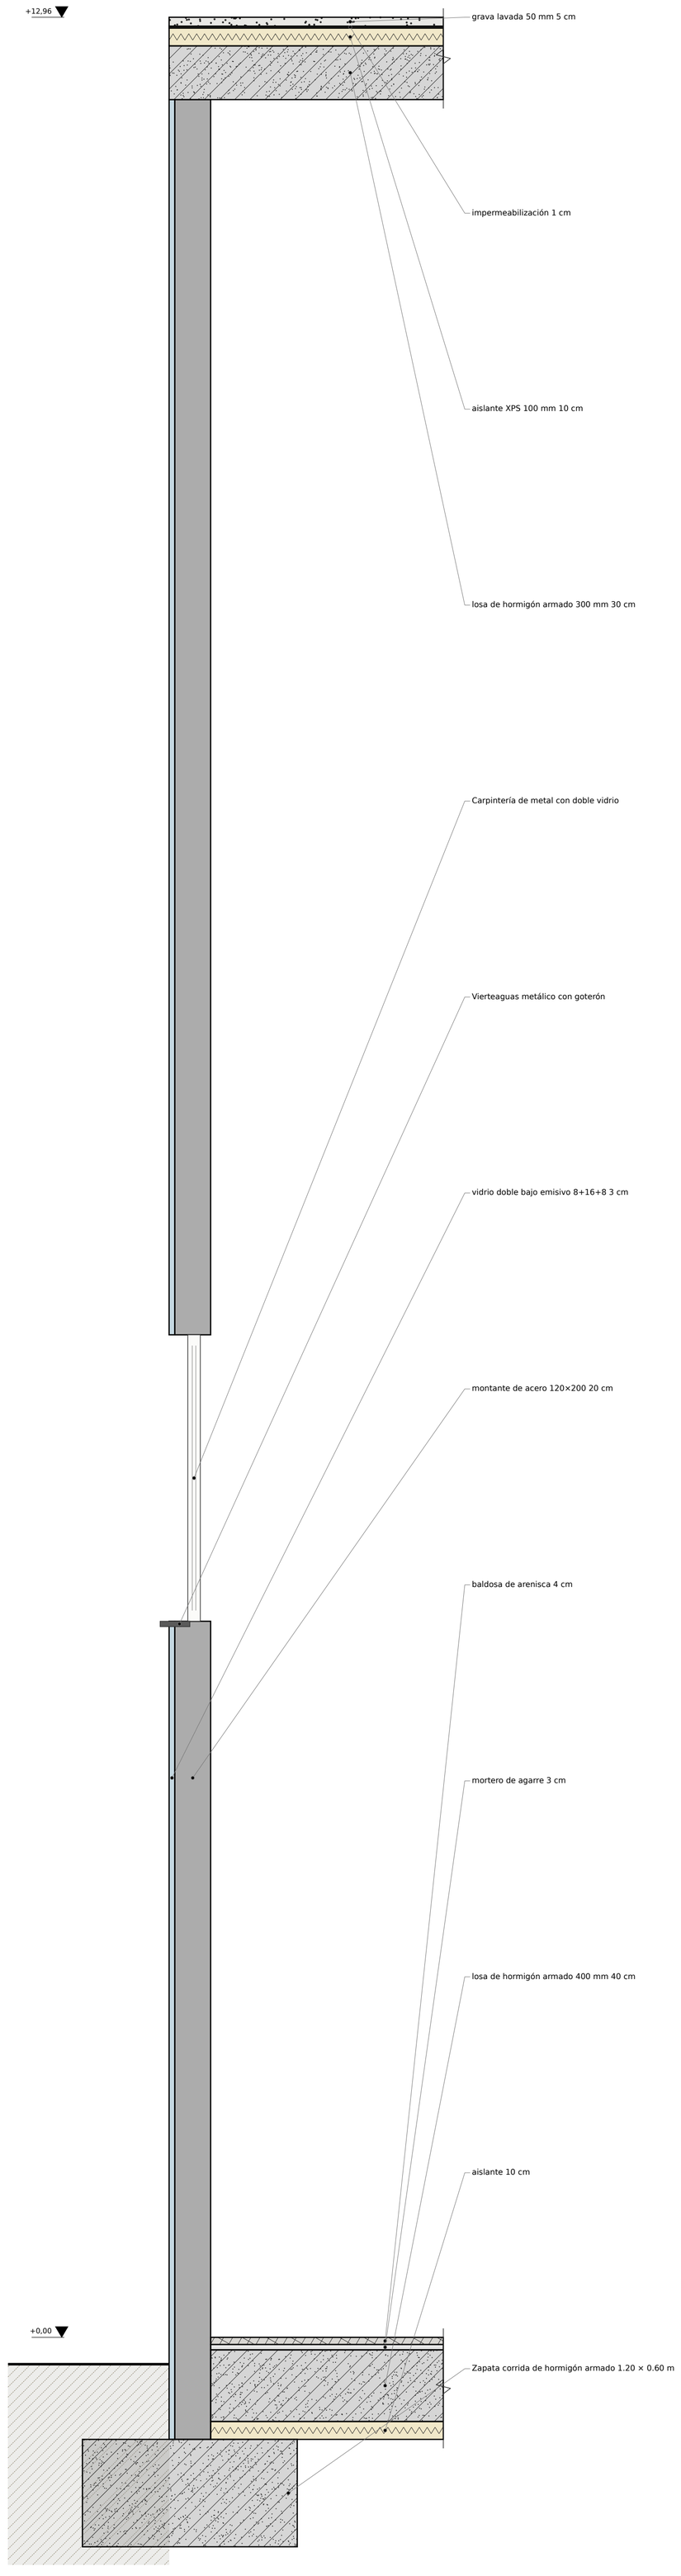


FACHADA NORTE DEL RESTAURANTE · VIDRIO Y ACERO BAJO EL PLANO

E 1:20

0 0.5 1 2 m

CASO_022 · PROPUESTA A	E 1:20	**D01**
SECCIÓN CONSTRUCTIVA DE LA FACHADA NORTE DEL RESTAURANTE, BAJO EL PLANO, 1:20	Anteproyecto	