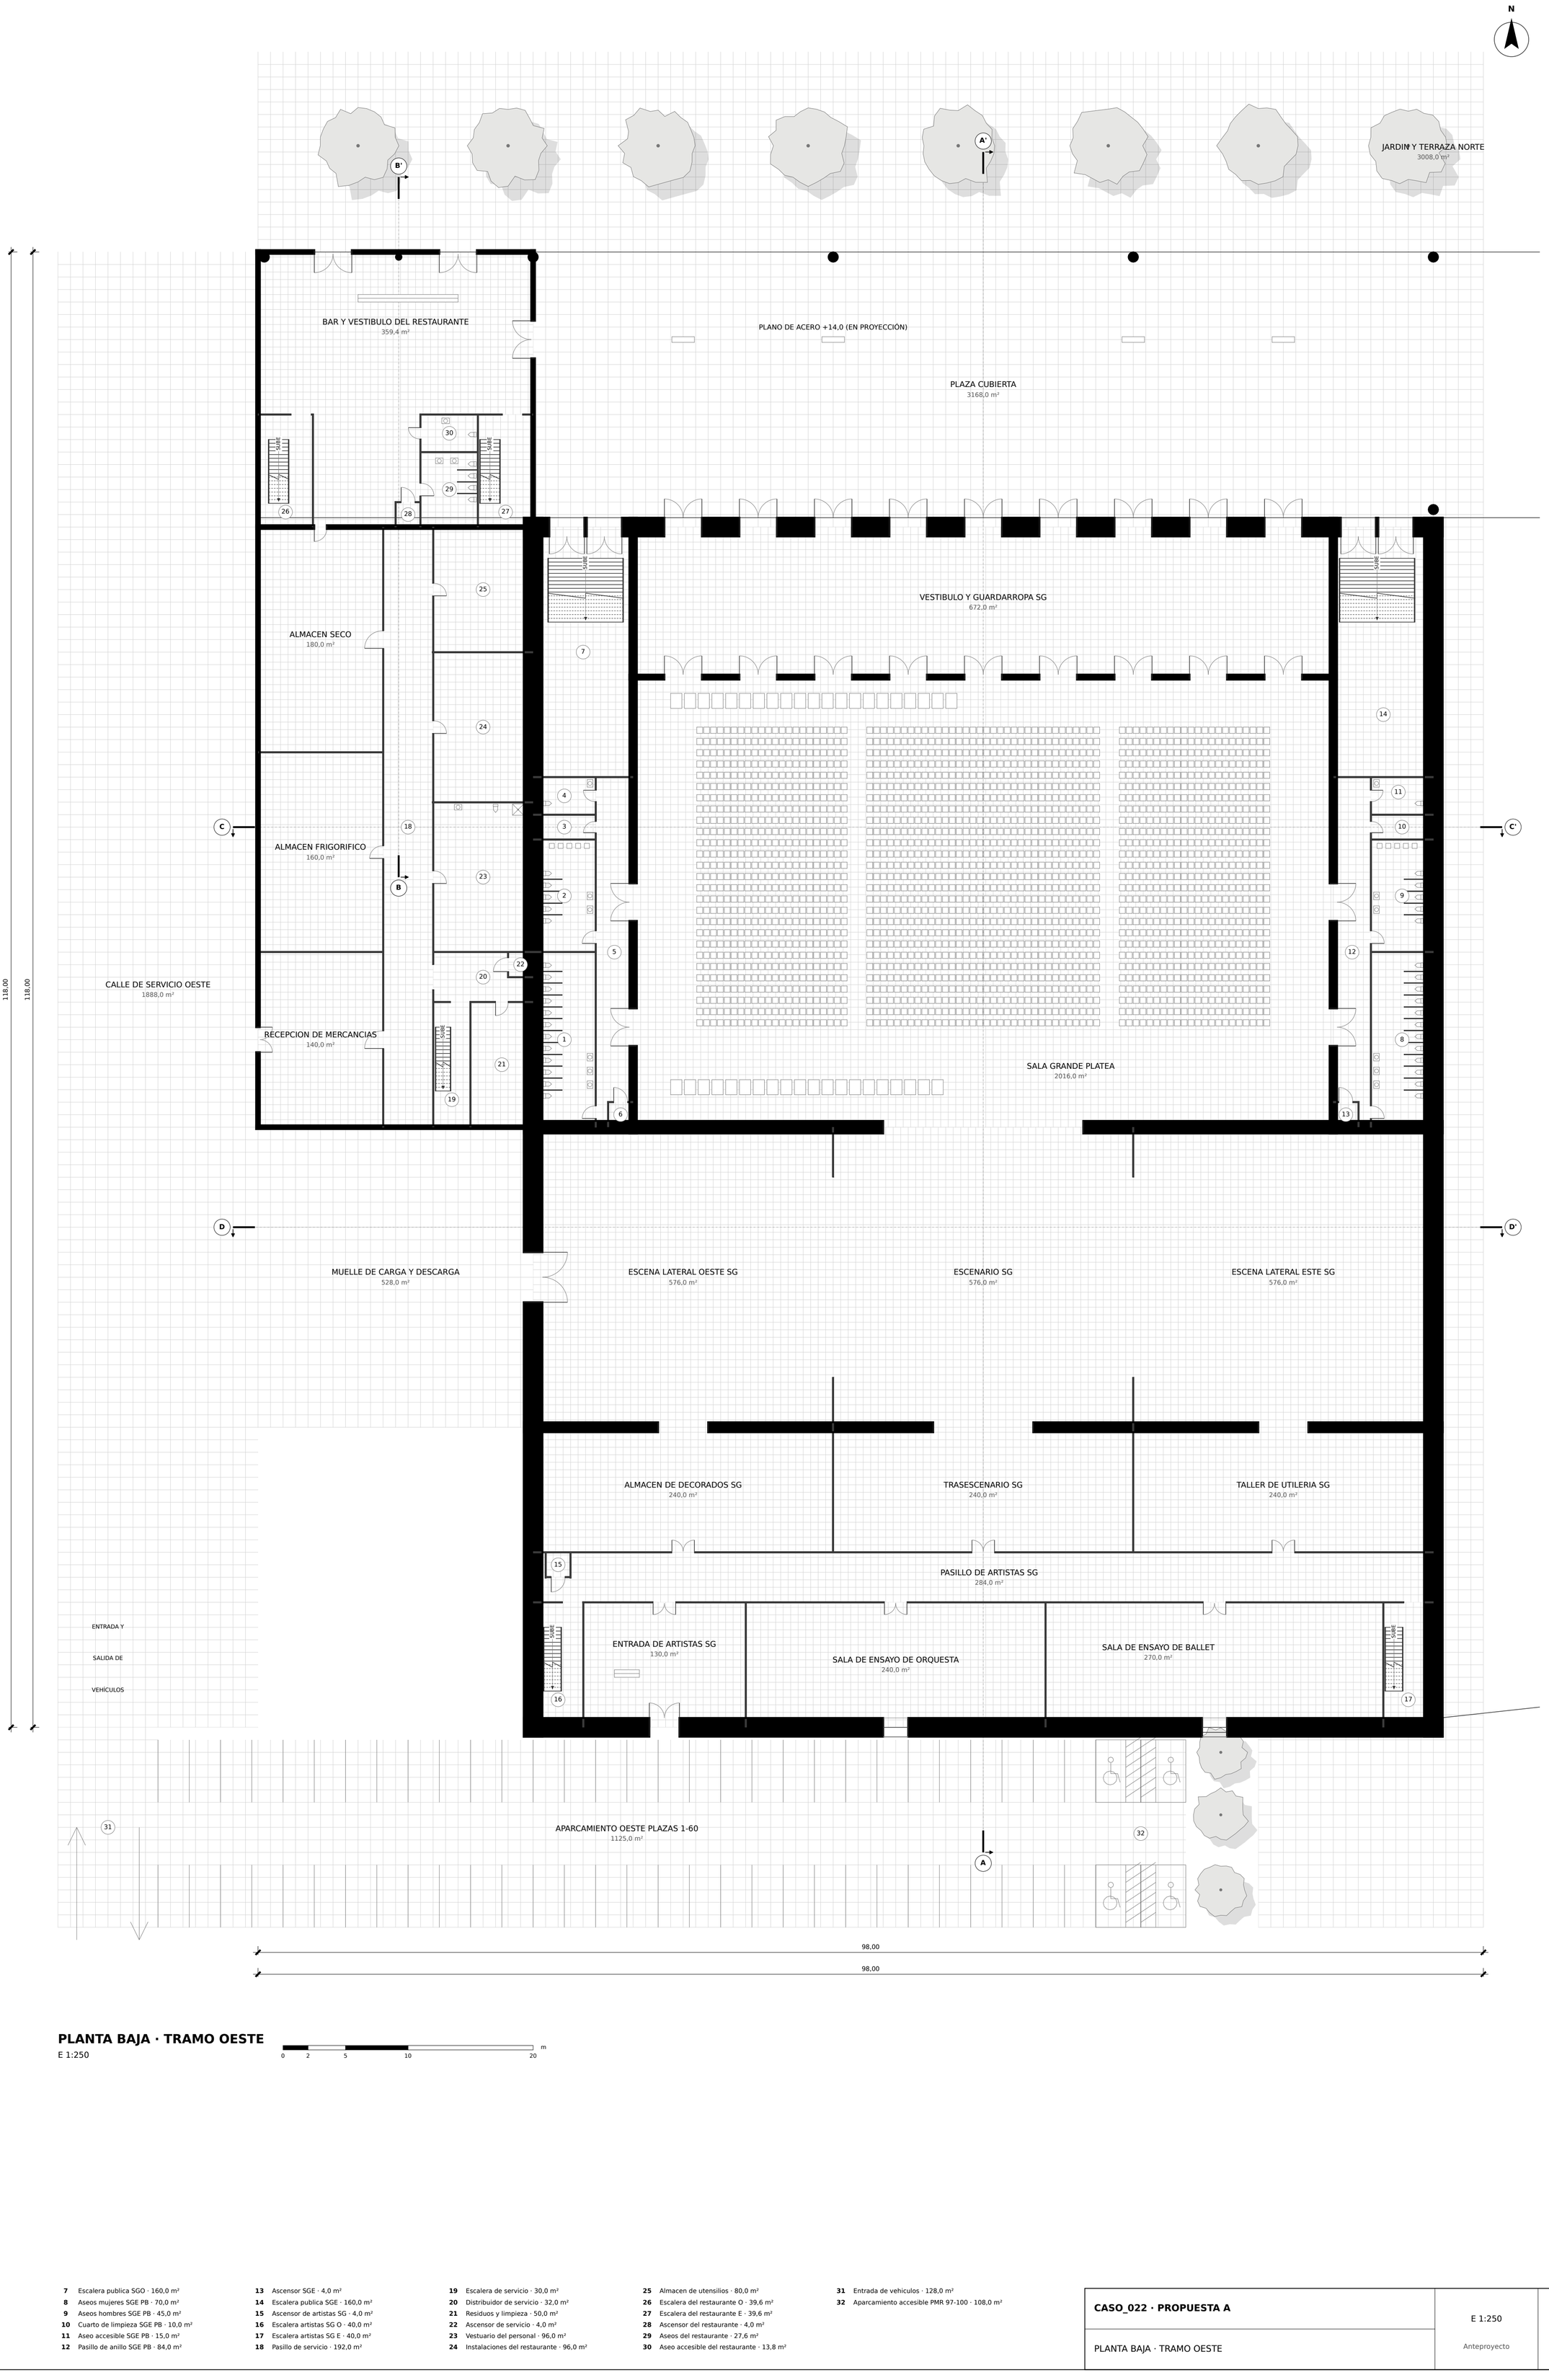


PLANTA BAJA · TRAMO OESTE

E 1:250

0 2 5 10 20 m

1 Aseos mujeres SGO PB · 70,0 m²
2 Aseos hombres SGO PB · 45,0 m²
3 Cuarto de limpieza SGO PB · 10,0 m²
4 Aseo accesible SGO PB · 15,0 m²
5 Pasillo de anillo SGO PB · 84,0 m²
6 Ascensor SGO · 4,0 m²
7 Escalera publica SGO · 160,0 m²
8 Aseos mujeres SGE PB · 70,0 m²
9 Aseos hombres SGE PB · 45,0 m²
10 Cuarto de limpieza SGE PB · 10,0 m²
11 Aseo accesible SGE PB · 15,0 m²
12 Pasillo de anillo SGE PB · 84,0 m²
13 Ascensor SGE · 4,0 m²
14 Escalera publica SGE · 160,0 m²
15 Ascensor de artistas SG · 4,0 m²
16 Escalera artistas SG O · 40,0 m²
17 Escalera artistas SG E · 40,0 m²
18 Pasillo de servicio · 192,0 m²
19 Escalera de servicio · 30,0 m²
20 Distribuidor de servicio · 32,0 m²
21 Residuos y limpieza · 50,0 m²
22 Ascensor de servicio · 4,0 m²
23 Vestuario del personal · 96,0 m²
24 Instalaciones del restaurante · 96,0 m²
25 Almacen de utensilios · 80,0 m²
26 Escalera del restaurante O · 39,6 m²
27 Escalera del restaurante E · 39,6 m²
28 Ascensor del restaurante · 4,0 m²
29 Aseos del restaurante · 27,6 m²
30 Aseo accesible del restaurante · 13,8 m²
31 Entrada de vehiculos · 128,0 m²
32 Aparcamiento accesible PMR 97-100 · 108,0 m²

CASO_022 · PROPUESTA A	E 1:250	**P01a**
PLANTA BAJA · TRAMO OESTE	Anteproyecto	