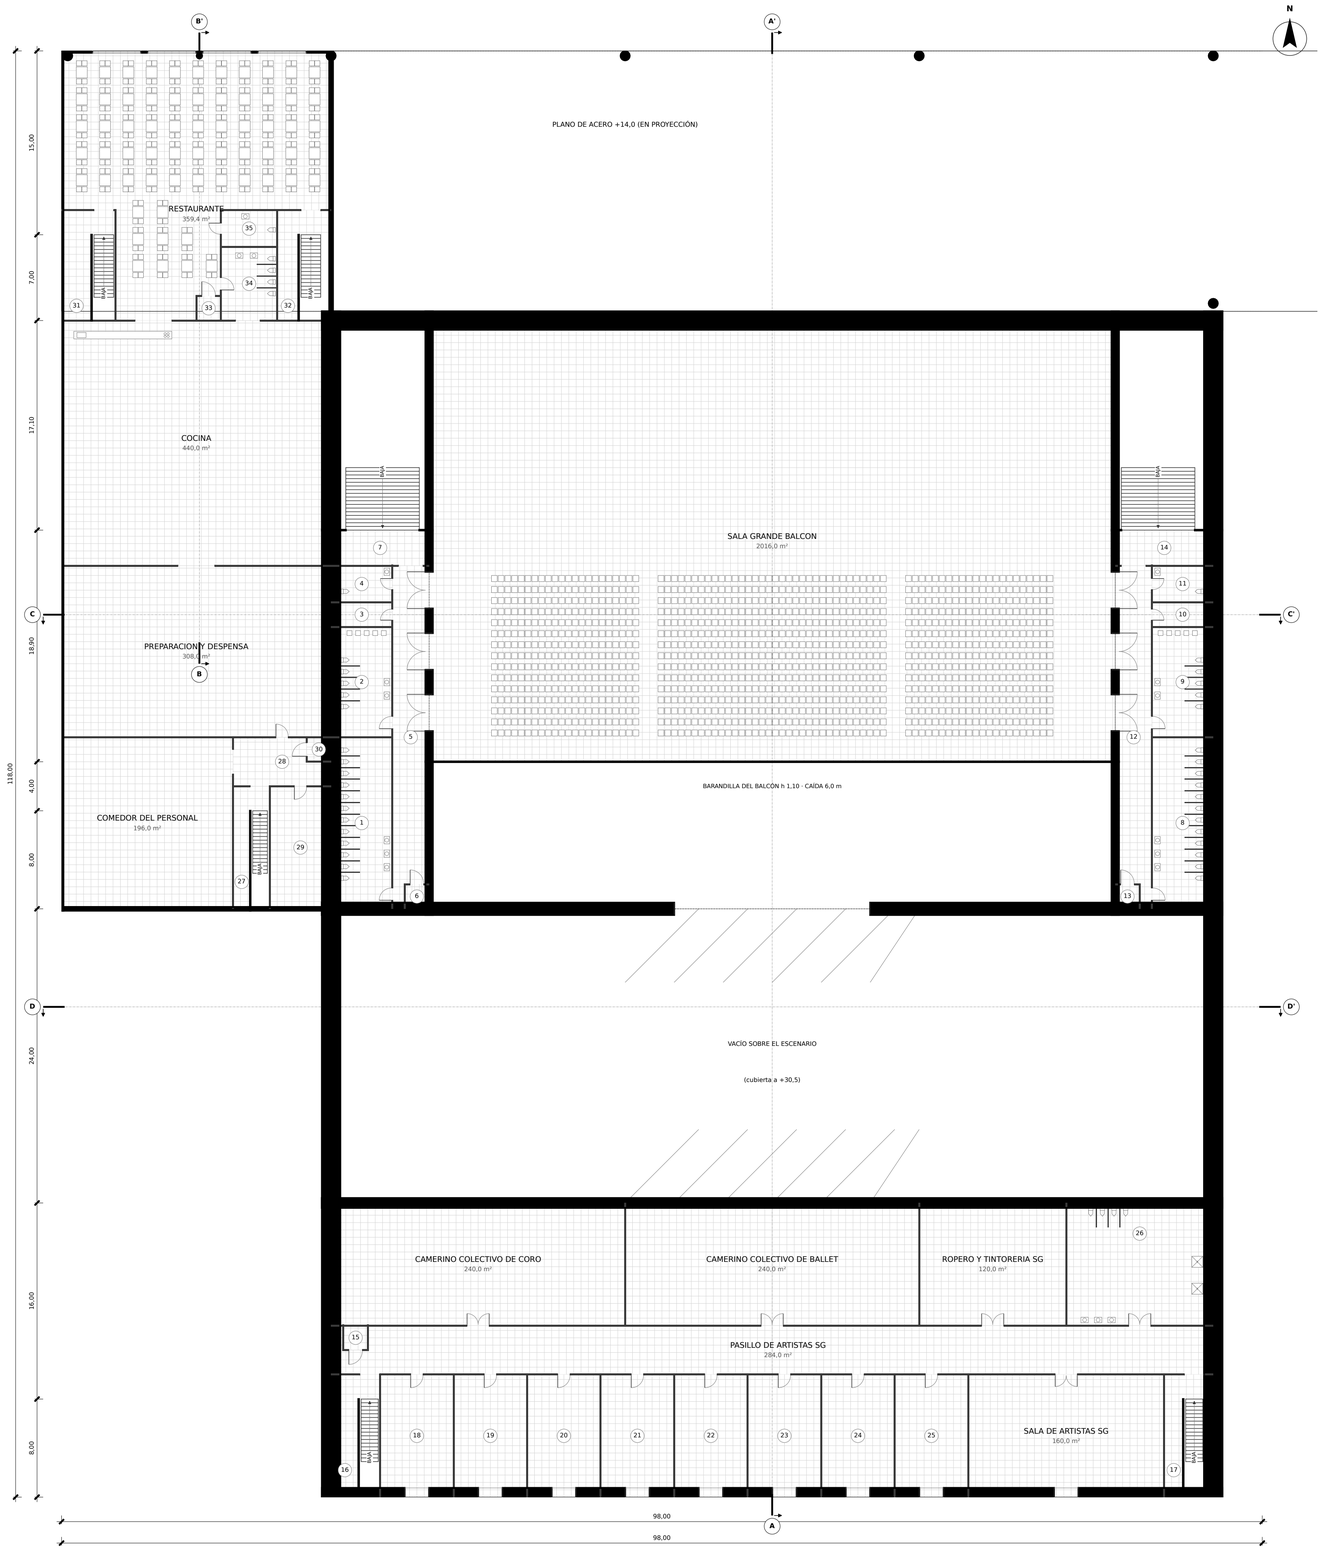


PLANTA PRIMERA · TRAMO OESTE

E 1:250

0 2 5 10 20 m

1 Aseos mujeres SGO N1 · 70,0 m²
2 Aseos hombres SGO N1 · 45,0 m²
3 Cuarto de limpieza SGO N1 · 10,0 m²
4 Aseo accesible SGO N1 · 15,0 m²
5 Pasillo de anillo SGO N1 · 84,0 m²
6 Ascensor SGO · 4,0 m²
7 Rellano de escalera SGO · 23,2 m²
8 Aseos mujeres SGE N1 · 70,0 m²
9 Aseos hombres SGE N1 · 45,0 m²
10 Cuarto de limpieza SGE N1 · 10,0 m²
11 Aseo accesible SGE N1 · 15,0 m²
12 Pasillo de anillo SGE N1 · 84,0 m²
13 Ascensor SGE · 4,0 m²
14 Rellano de escalera SGE · 23,2 m²
15 Ascensor de artistas SG · 4,0 m²
16 Escalera artistas SG O · 26,0 m²
17 Escalera artistas SG E · 20,4 m²
18 Camerino solista 1 · 60,0 m²
19 Camerino solista 2 · 60,0 m²
20 Camerino solista 3 · 60,0 m²
21 Camerino solista 4 · 60,0 m²
22 Camerino solista 5 · 60,0 m²
23 Camerino solista 6 · 60,0 m²
24 Camerino solista 7 · 60,0 m²
25 Camerino solista 8 · 60,0 m²
26 Aseos y duchas de artistas SG · 120,0 m²
27 Escalera de servicio · 17,2 m²
28 Distribuidor de servicio · 32,0 m²
29 Almacen de menaje · 50,0 m²
30 Ascensor de servicio · 4,0 m²
31 Escalera del restaurante O · 25,9 m²
32 Escalera del restaurante E · 21,1 m²
33 Ascensor del restaurante · 4,0 m²
34 Aseos del restaurante · 27,6 m²
35 Aseo accesible del restaurante · 13,8 m²

CASO_022 · PROPUESTA A	E 1:250	**P02a**
PLANTA PRIMERA · TRAMO OESTE	Anteproyecto	