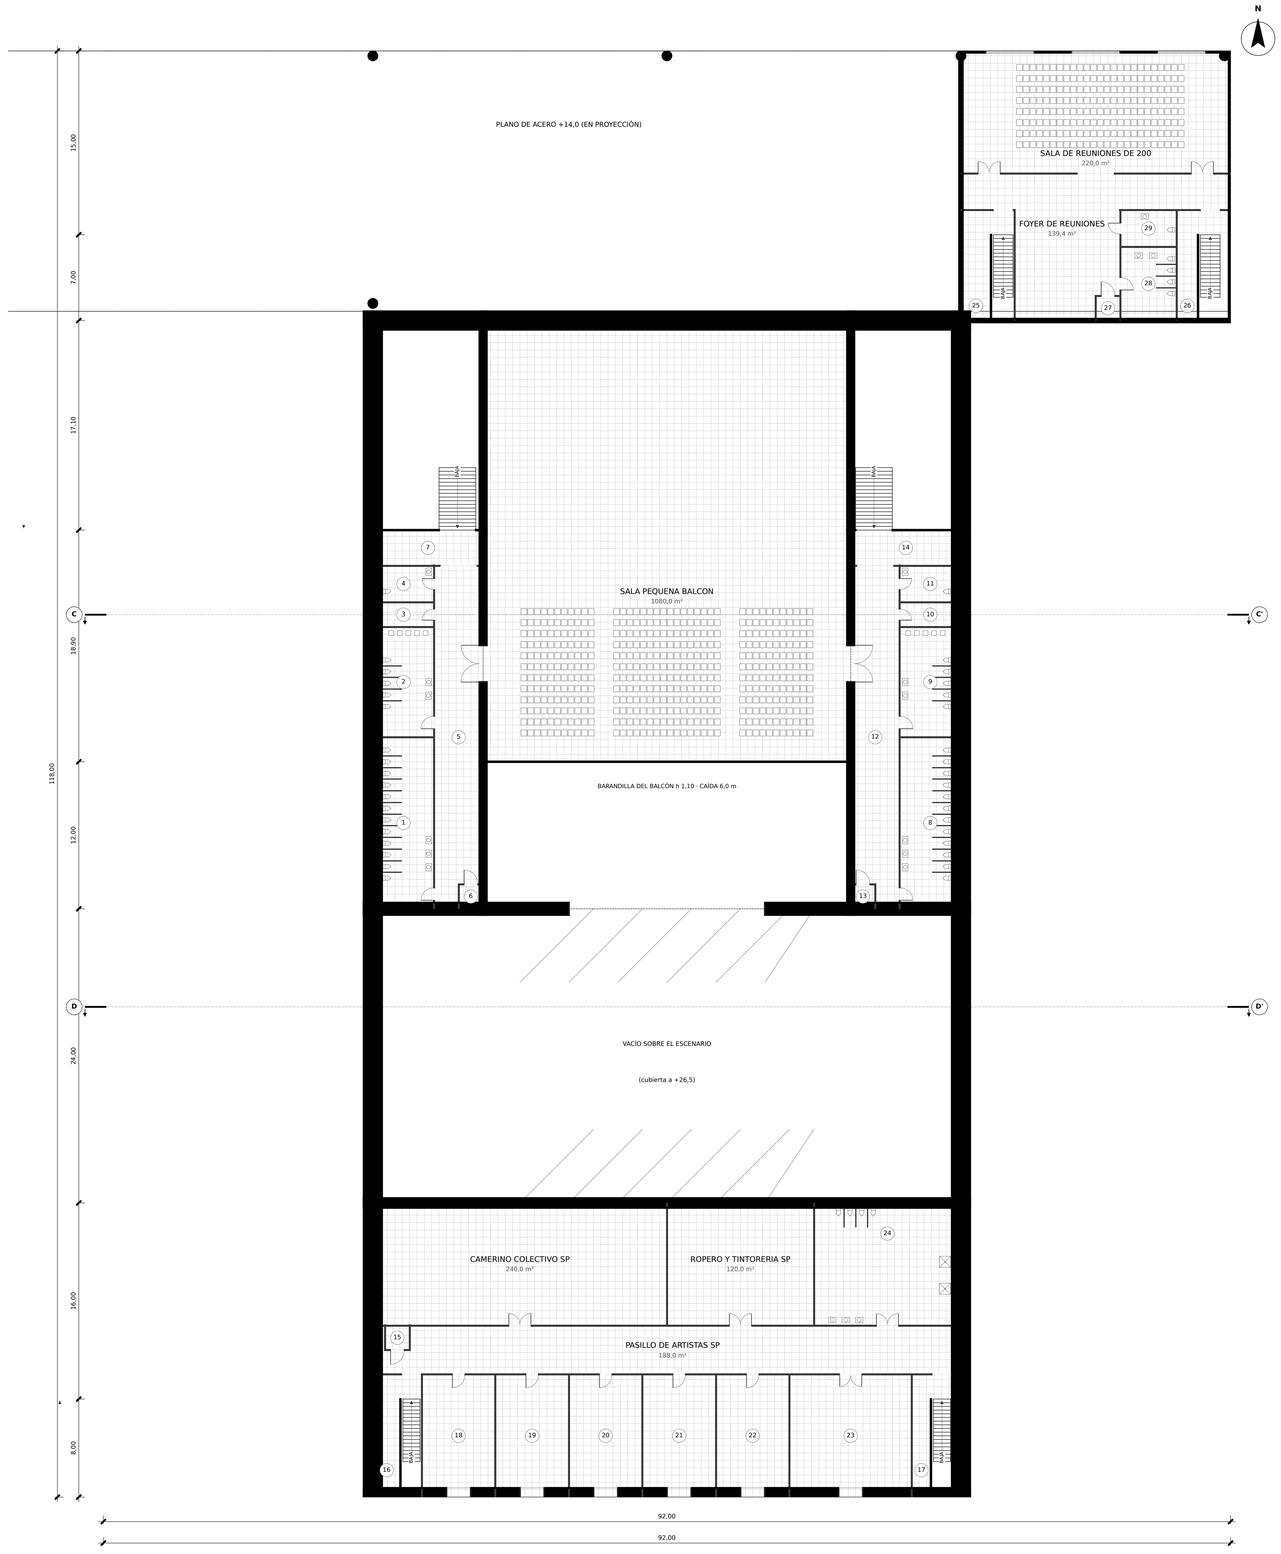


PLANTA PRIMERA · TRAMO ESTE

E 1:250

0 2 5 10 20 m

1 Aseos mujeres SPO N1 · 70,0 m²
2 Aseos hombres SPO N1 · 45,0 m²
3 Cuarto de limpieza SPO N1 · 10,0 m²
4 Aseo accesible SPO N1 · 15,0 m²
5 Pasillo de anillo SPO N1 · 112,0 m²
6 Ascensor SPO · 4,0 m²
7 Rellano de escalera SPO · 26,1 m²
8 Aseos mujeres SPE N1 · 70,0 m²
9 Aseos hombres SPE N1 · 45,0 m²
10 Cuarto de limpieza SPE N1 · 10,0 m²
11 Aseo accesible SPE N1 · 15,0 m²
12 Pasillo de anillo SPE N1 · 112,0 m²
13 Ascensor SPE · 4,0 m²
14 Rellano de escalera SPE · 26,1 m²
15 Ascensor de artistas SP · 4,0 m²
16 Escalera artistas SP O · 26,0 m²
17 Escalera artistas SP E · 20,4 m²
18 Camerino solista SP 1 · 60,0 m²
19 Camerino solista SP 2 · 60,0 m²
20 Camerino solista SP 3 · 60,0 m²
21 Camerino solista SP 4 · 60,0 m²
22 Camerino solista SP 5 · 60,0 m²
23 Administracion y direccion · 100,0 m²
24 Aseos y duchas de artistas SP · 120,0 m²
25 Escalera de reuniones O · 26,0 m²
26 Escalera de reuniones E · 21,0 m²
27 Ascensor de reuniones · 4,0 m²
28 Aseos del embarcadero · 27,6 m²
29 Aseo accesible del embarcadero · 13,8 m²

CASO_022 · PROPUESTA A	E 1:250	**P02b**
PLANTA PRIMERA · TRAMO ESTE	Anteproyecto	