


**SECCIÓN A-A'**
E 1:200

0 2 5 10 20 m

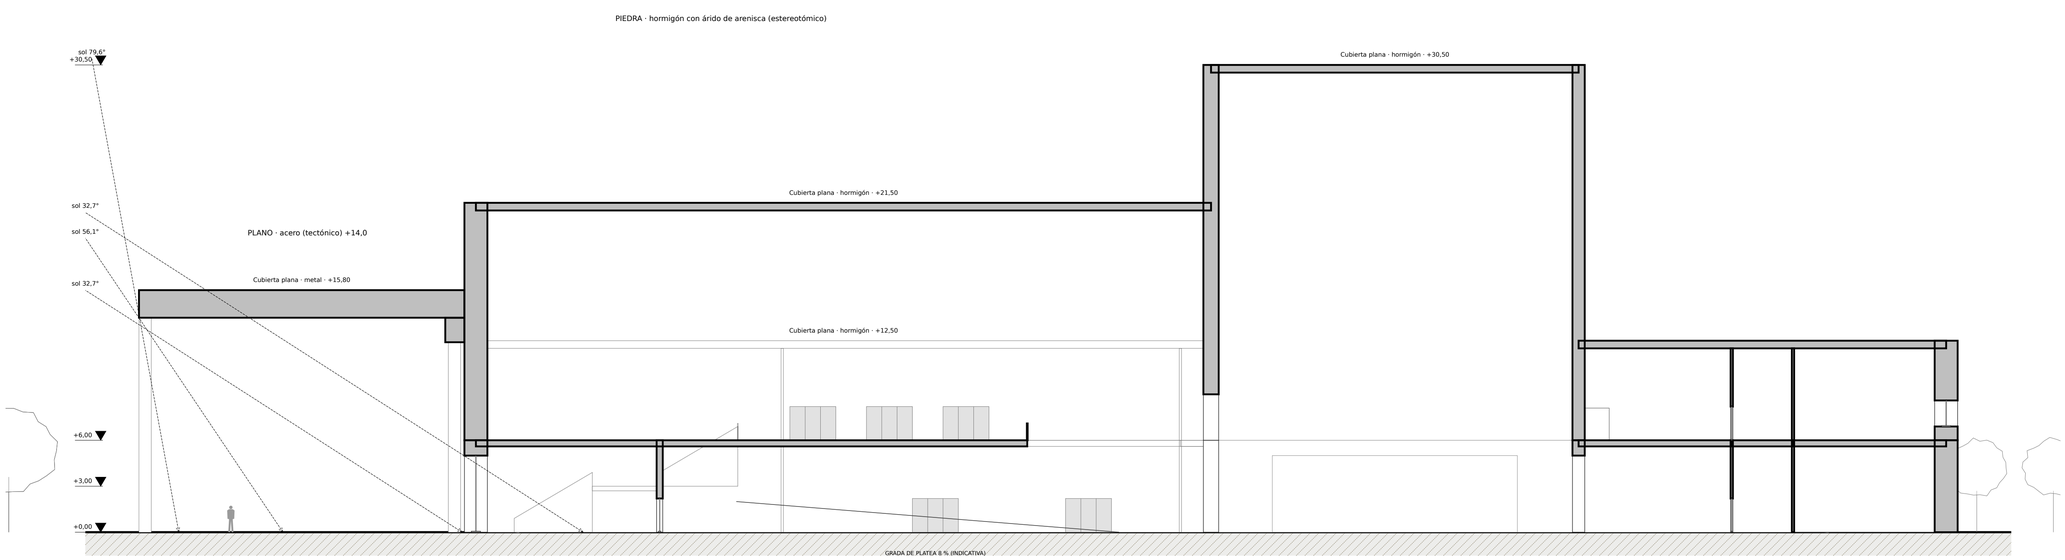


**SECCIÓN B-B'**
E 1:200

0 2 5 10 20 m

- - Rayo de sol: sol 32,7°
- - Rayo de sol: sol 32,7°
- - Rayo de sol: sol 56,1°
- - Rayo de sol: sol 79,6°
- - Rayo de sol: sol 32,7°
- - Rayo de sol: sol 56,1°

- - Rayo de sol: sol 79,6°
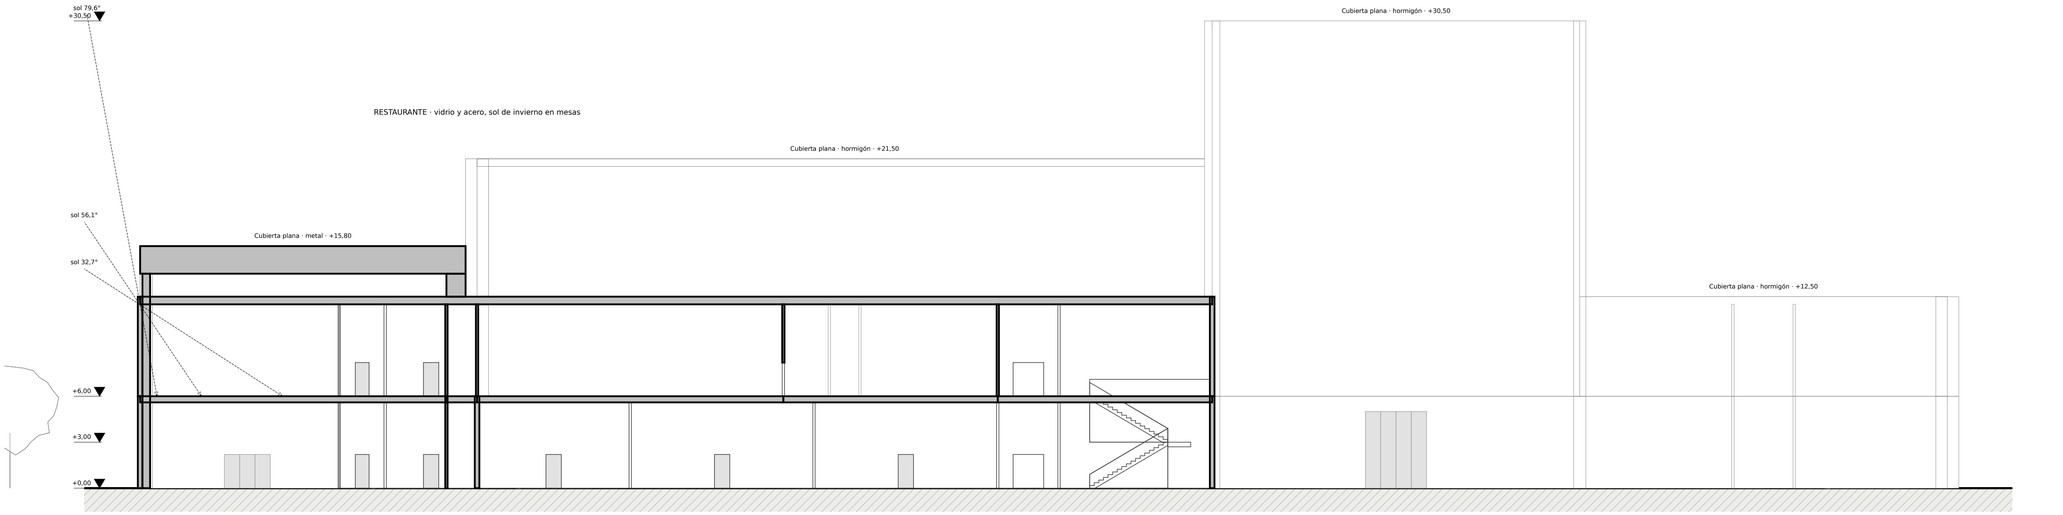
| | | |
|---|---|---|
| **CASO_022 · PROPUESTA A** | E 1:200 | **S01** |
| SECCIÓN GENERADORA A-A (PIEDRA, PLAZA Y PLANO) Y B-B (RESTAURANTE) | Anteproyecto | |