ANTEPROYECTO
VIVIENDA SOCIAL
PROGRESIVA
CASO_001 - Propuesta B

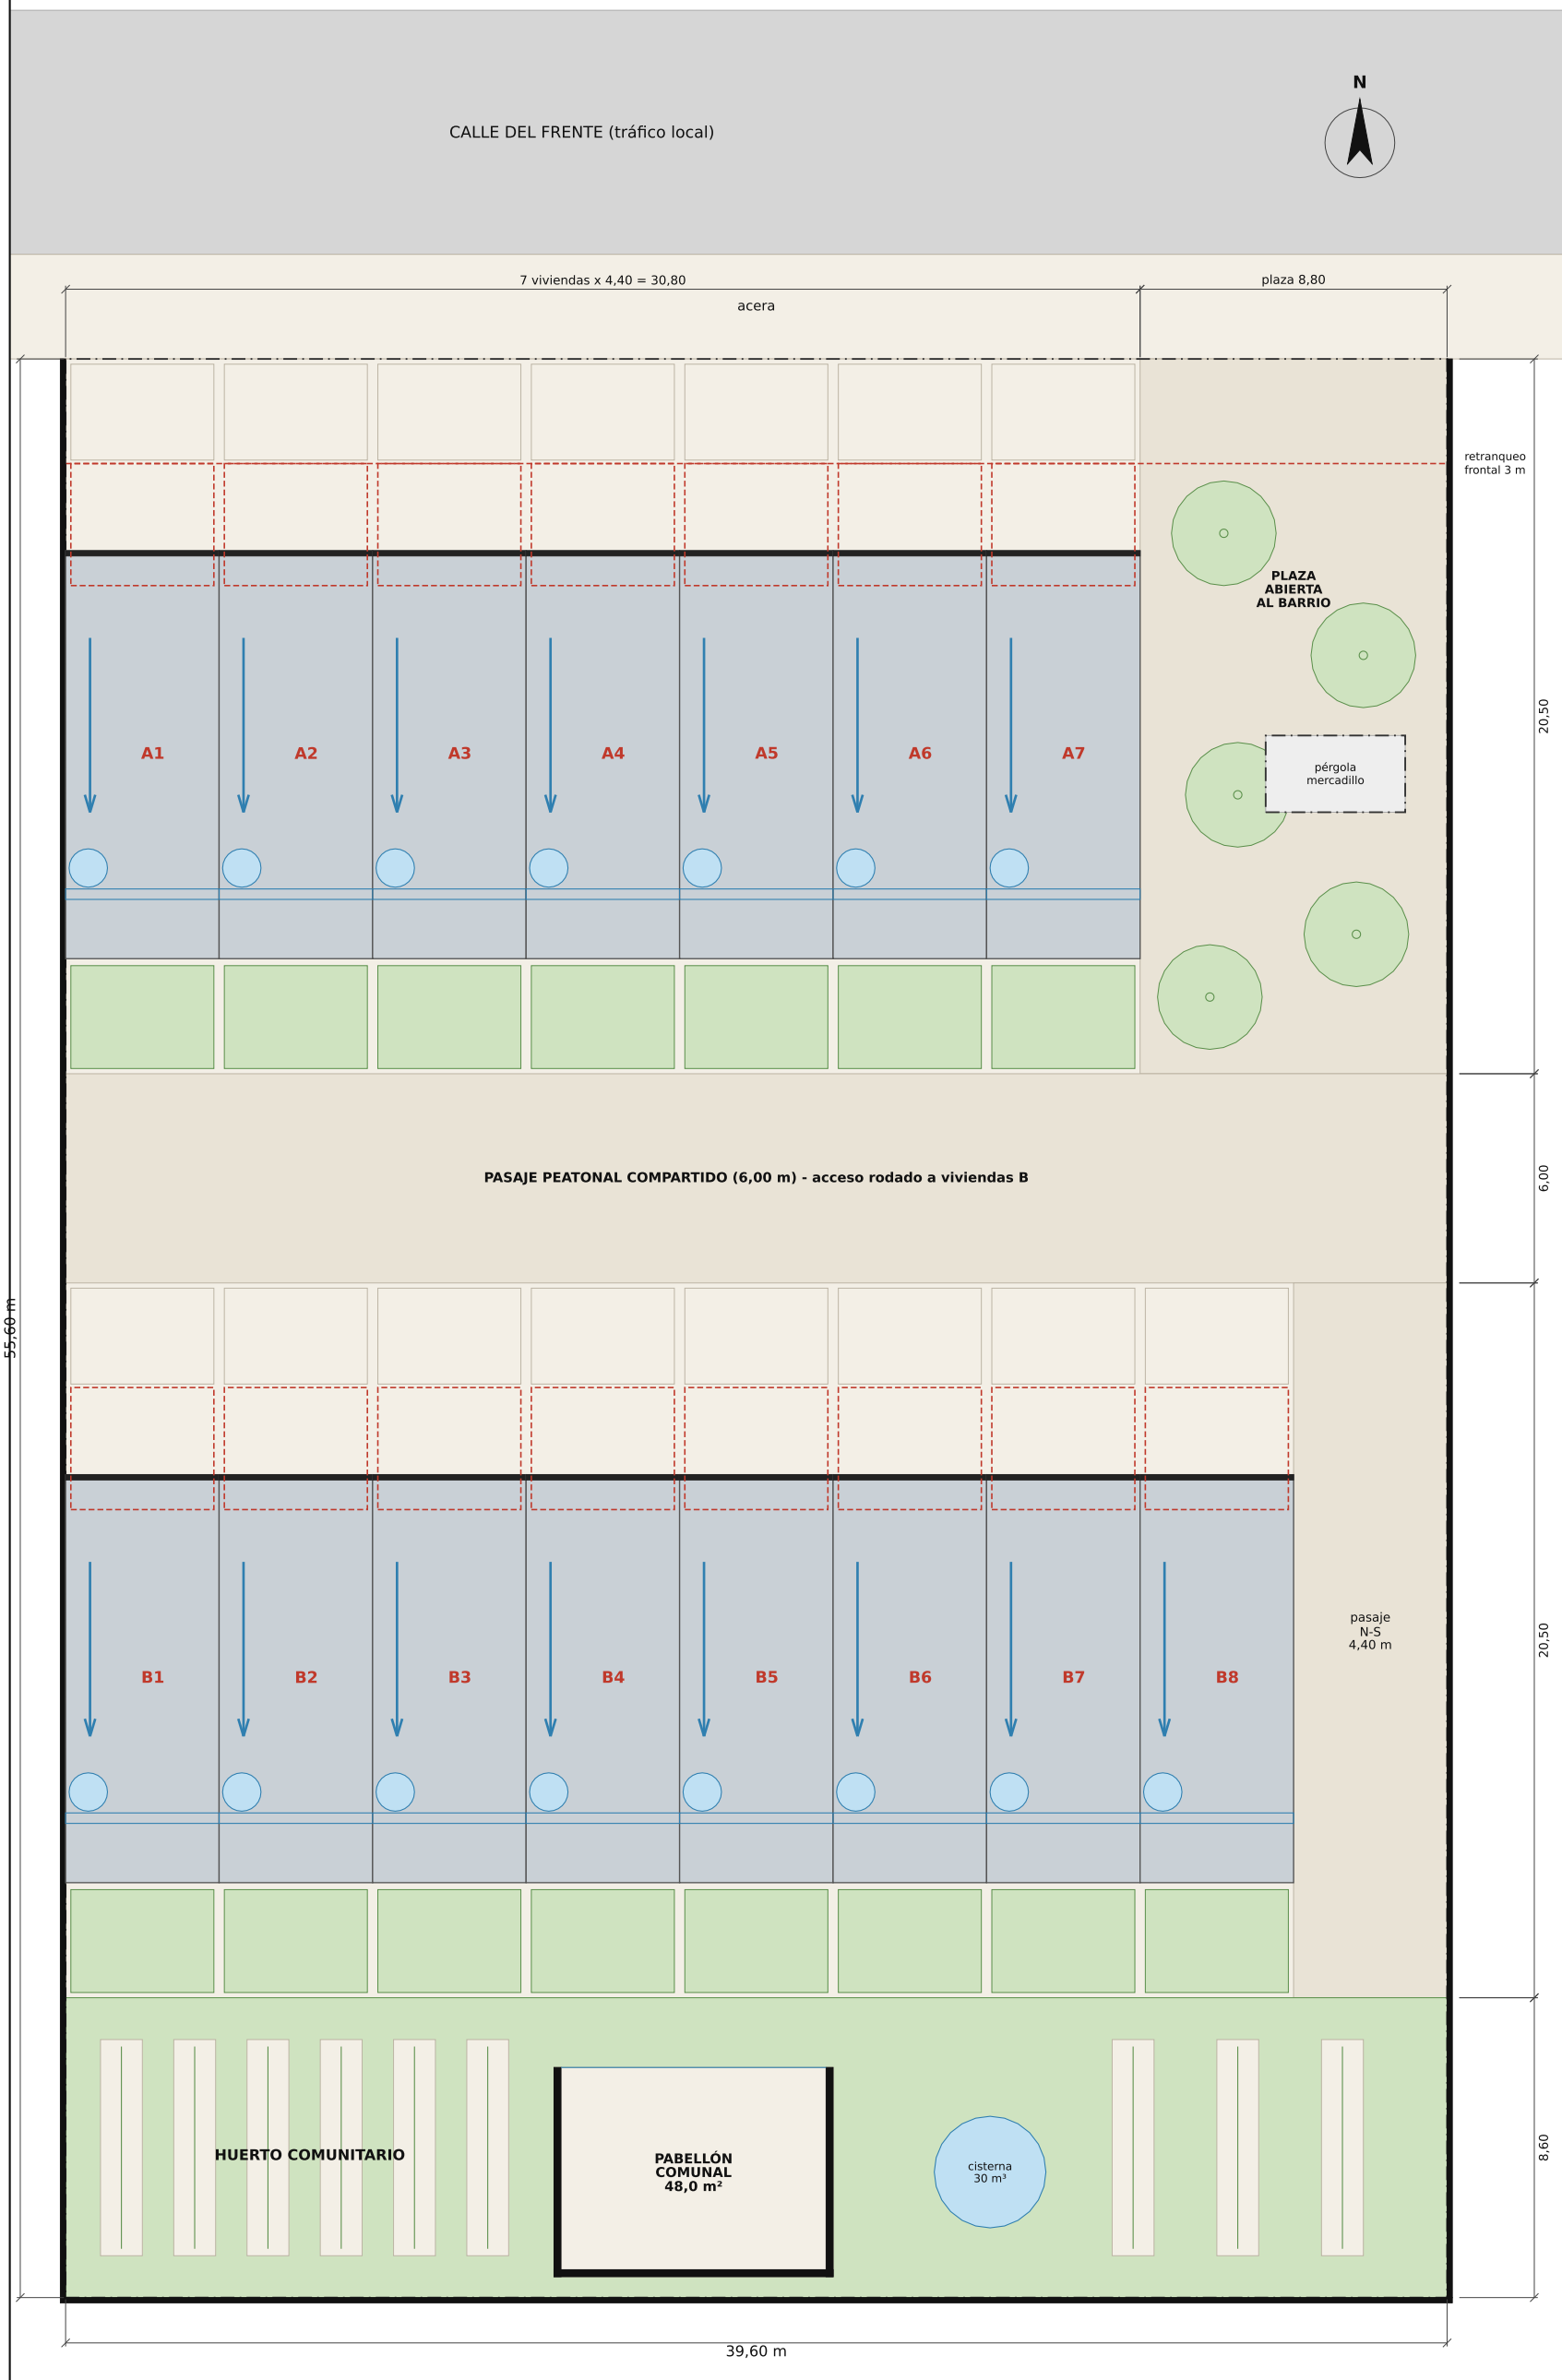

PLANTA DE CUBIERTAS
(cota +5,95 a +7,25)

Cubierta a un agua (14,4 %)
baja al norte y sube al sur
clerestorio/celosía ventilada
en el borde alto sur
Depósito de agua sobre torre
de escalera

Escala 1:200
(formato 297x420 mm)