PLANTA BAJA (+0,45)

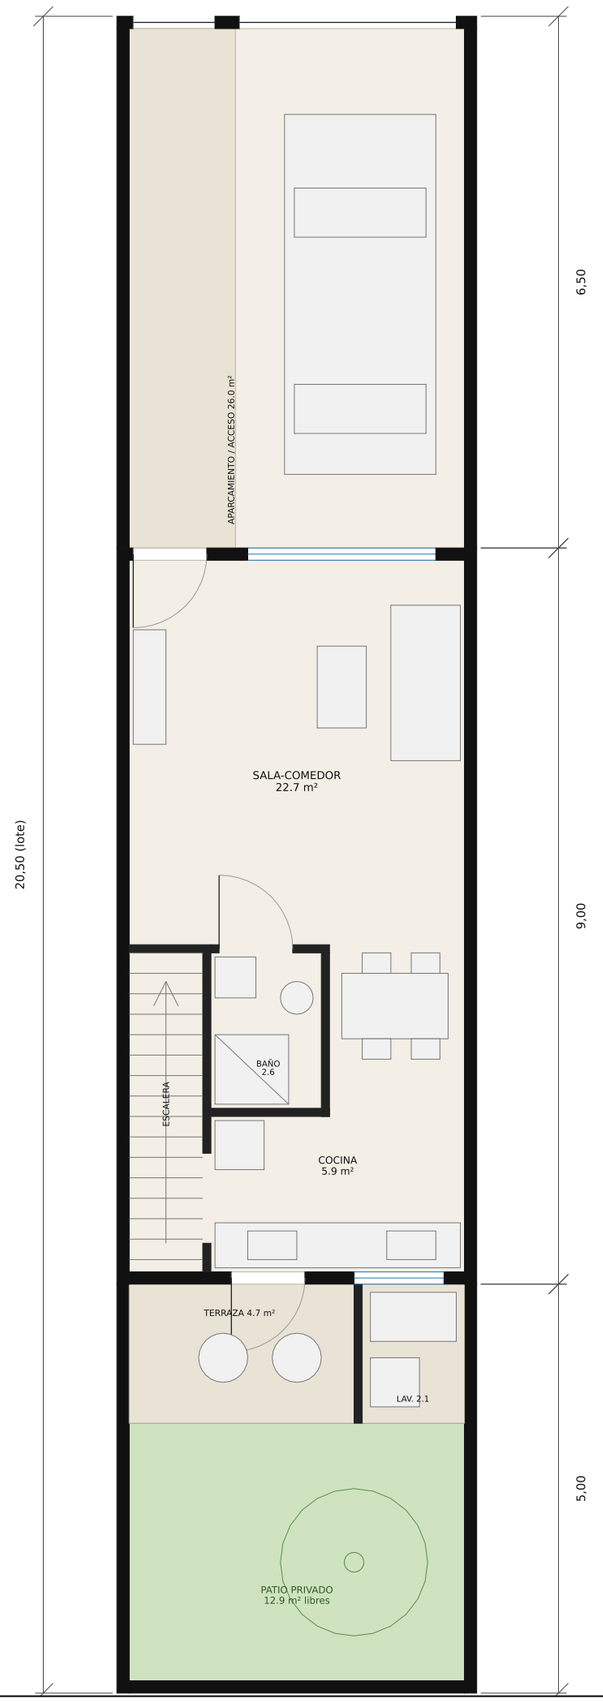

PLANTA ALTA (+3,25)

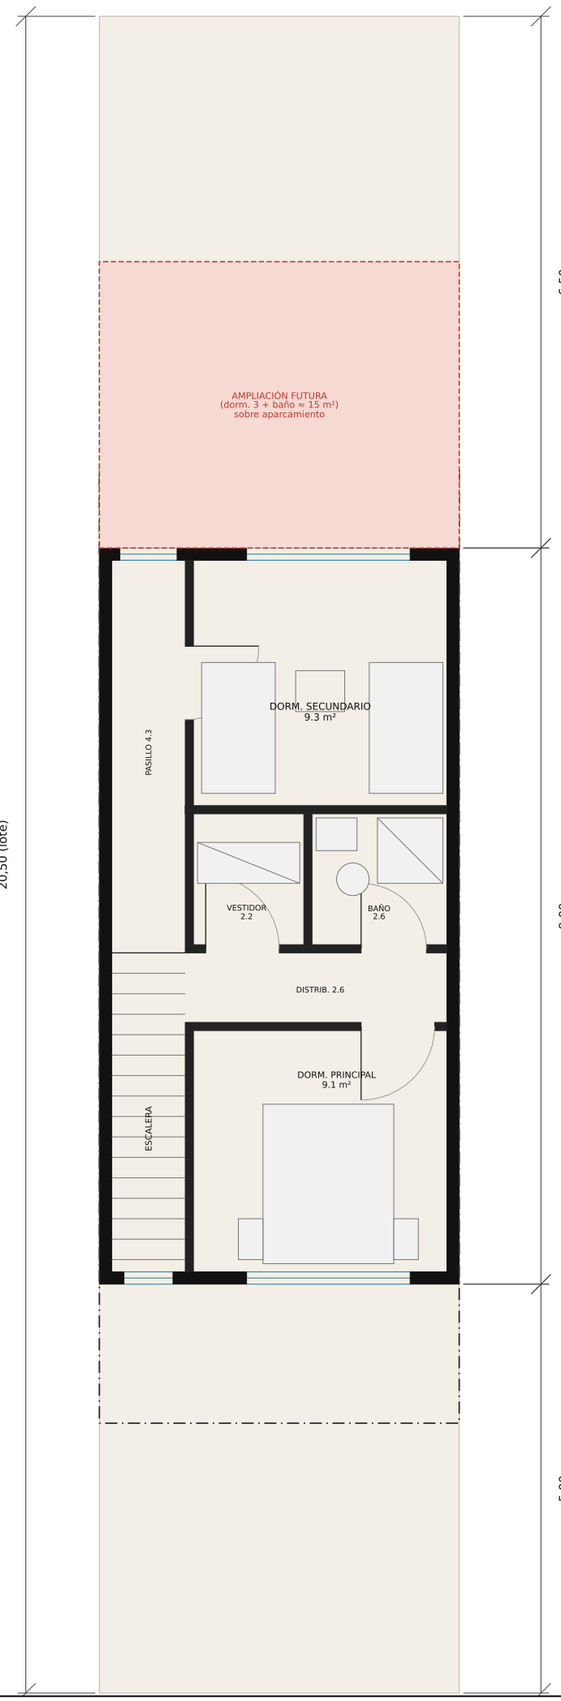

N

CUADRO DE SUPERFICIES (vivienda tipo)

PLANTA BAJA (superficie útil)	
Sala-comedor	22.7 m²
Cocina	5.9 m²
Baño social	2.6 m²
Lavadero	2.1 m²
Terraza cubierta	4.7 m²
Escalera (PB)	3.5 m²
PLANTA ALTA (superficie útil)	
Dormitorio secundario	9.3 m²
Vestidor/ropero	2.2 m²
Baño principal	2.6 m²
Distribuidor	2.6 m²
Dormitorio principal	9.1 m²
Pasillo (PA)	4.3 m²
Escalera (PA)	3.5 m²
Útil total (con terraza)	**75.2 m²**
Construida por planta (9,00 x 4,40)	39,6 m²
Construida total (2 plantas)	**79,2 m²**

0 1 2 5 m

ANTEPROYECTO VIVIENDA SOCIAL PROGRESIVA CASO_001 - Propuesta B

VIVIENDA TIPO PLANTAS BAJA Y ALTA

Estado inicial 79 m² construidos
Lote 4,40 x 20,50 m
Orientación frente N

Escala 1:75
(formato 420x297 mm)