PLANTA BAJA (+0,45)

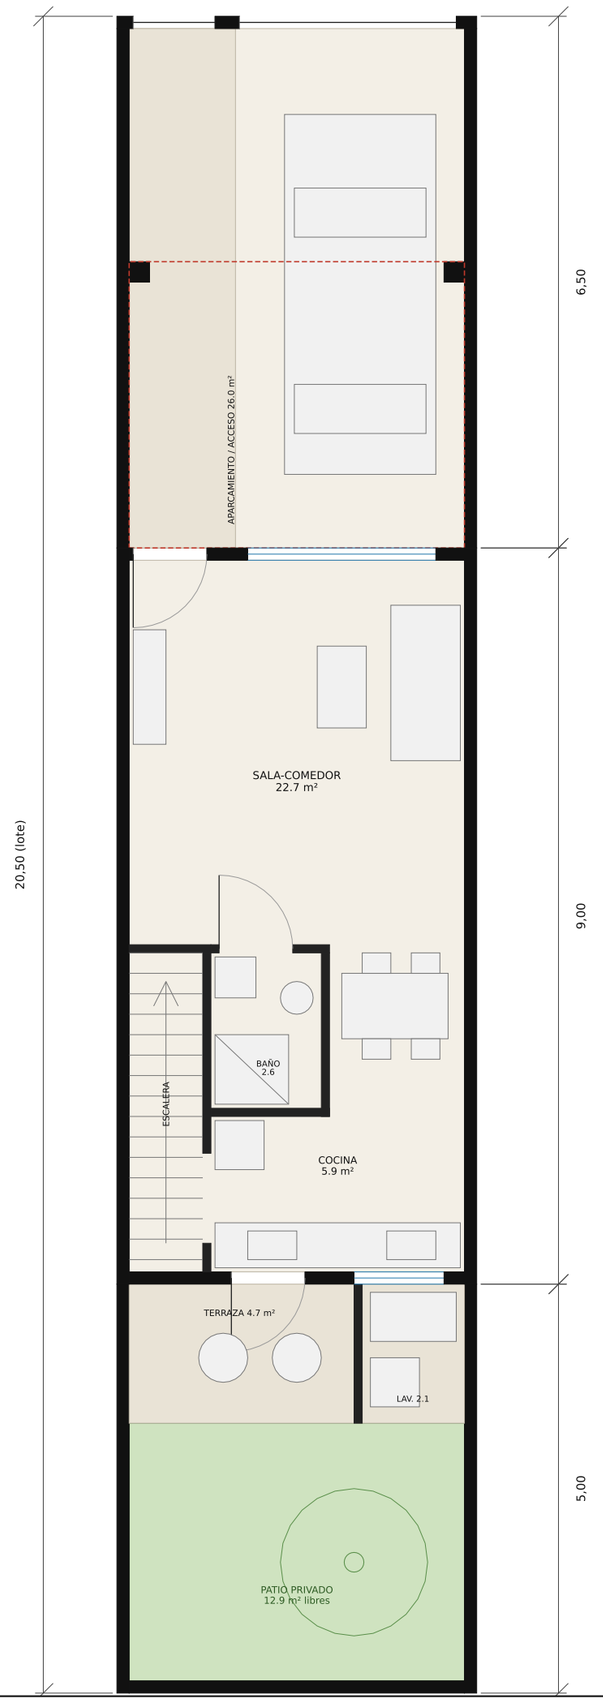

PLANTA ALTA (+3,25)

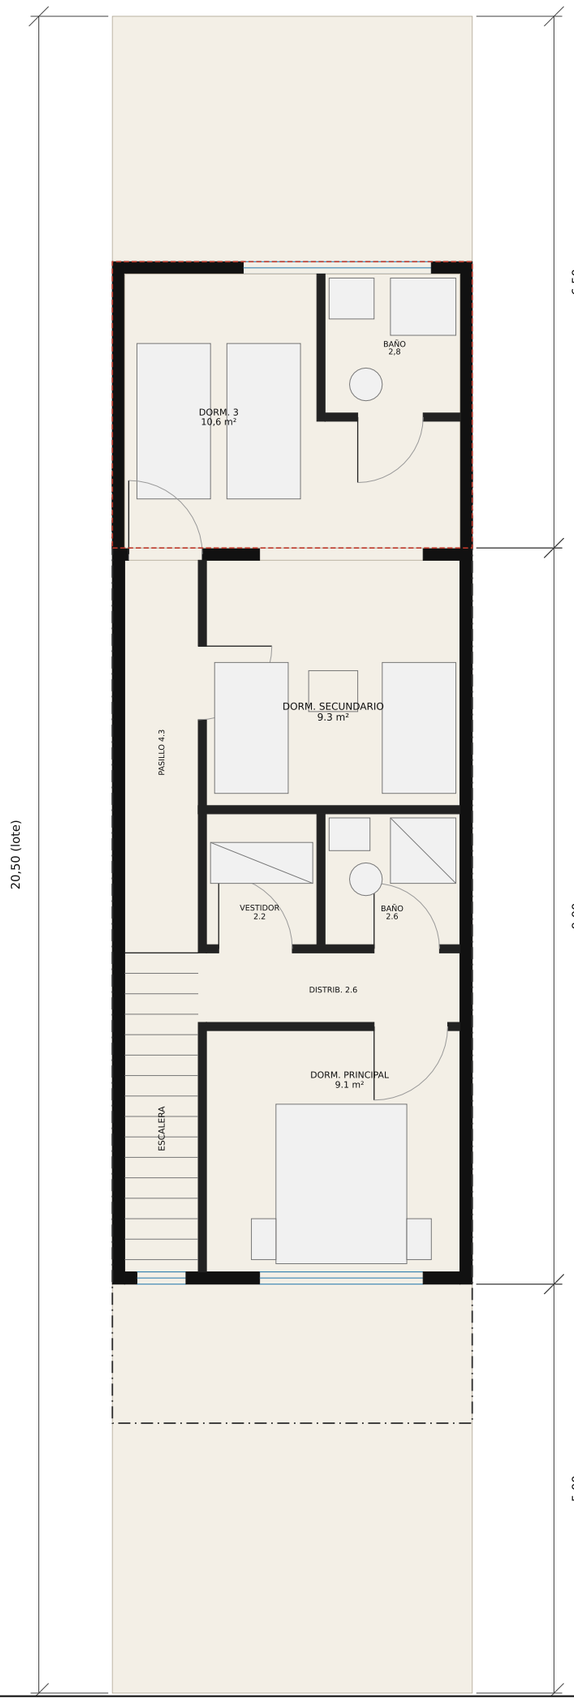

N

CUADRO DE SUPERFICIES (vivienda tipo)

PLANTA BAJA (superficie útil)	
Sala-comedor	22.7 m²
Cocina	5.9 m²
Baño social	2.6 m²
Lavadero	2.1 m²
Terraza cubierta	4.7 m²
Escalera (PB)	3.5 m²
PLANTA ALTA (superficie útil)	
Dormitorio secundario	9.3 m²
Vestidor/ropero	2.2 m²
Baño principal	2.6 m²
Distribuidor	2.6 m²
Dormitorio principal	9.1 m²
Pasillo (PA)	4.3 m²
Escalera (PA)	3.5 m²
Útil total (con terraza)	**75.2 m²**
Construida por planta (9,00 x 4,40)	39,6 m²
Construida total (2 plantas)	**79,2 m²**
AMPLIACIÓN (4,40 x 3,50 sobre aparcamiento)	
Dormitorio 3 + baño (bruto)	15,4 m²
Construida total ampliada	**94,6 m²**
Opción B: cerrar PB bajo ampliación	+13 m²

0 1 2 5 m

ANTEPROYECTO VIVIENDA SOCIAL PROGRESIVA CASO_001 - Propuesta B

VIVIENDA TIPO AMPLIADA PLANTAS BAJA Y ALTA

Ampliación ejecutada por el propietario sin demoler: dormitorio 3 + baño sobre el aparcamiento (carport)

Escala 1:75 (formato 420x297 mm)