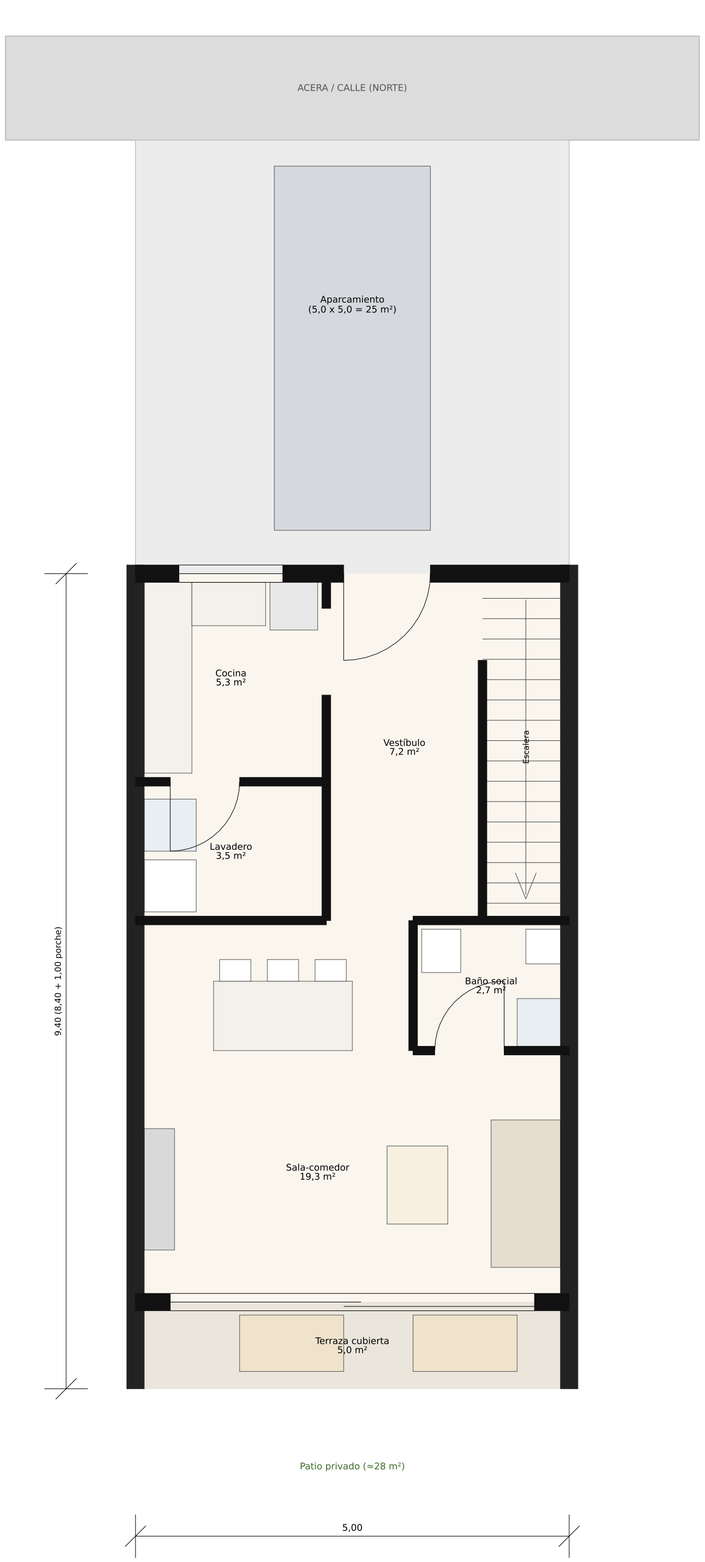

PLANTA BAJA

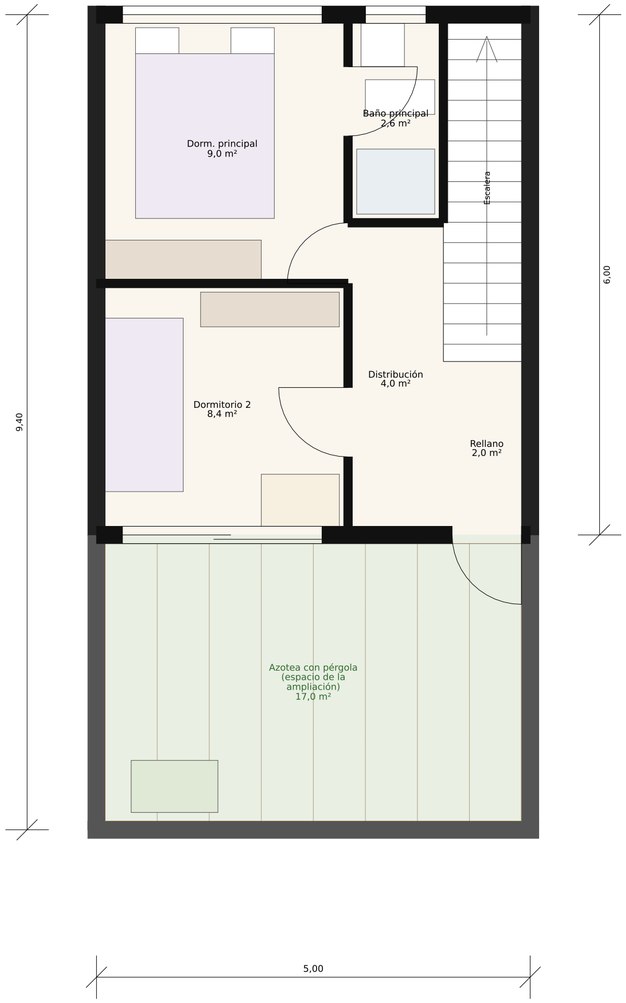

PLANTA PRIMERA (estado inicial)

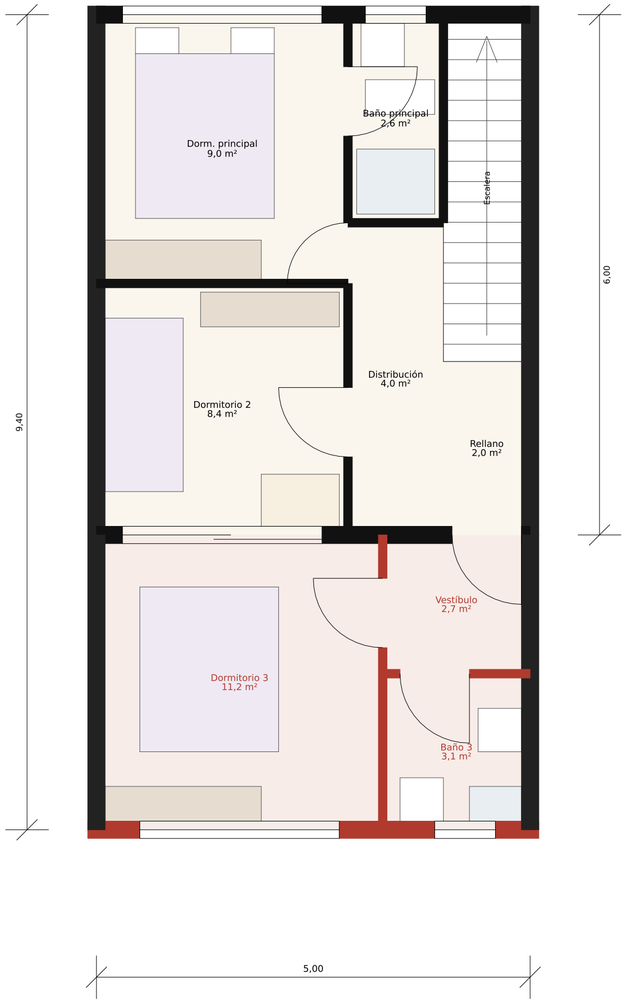

PLANTA PRIMERA con AMPLIACIÓN

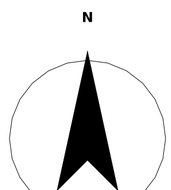

Superficie útil vivienda inicial: PB 47,0 m² + P1 30,0 m² = 77,0 m²

Ampliación prevista: dormitorio 3 + baño 3 + vestíbulo = 17,0 m² (dorm.+baño ≈ 14,3 m²)

Escala gráfica 1:50

VIVIENDA TIPO

Planta baja, planta primera y ampliación - 1:50

Escala 1:50 | Hoja 3/5 | Anteproyecto CASO_001 - propuesta C