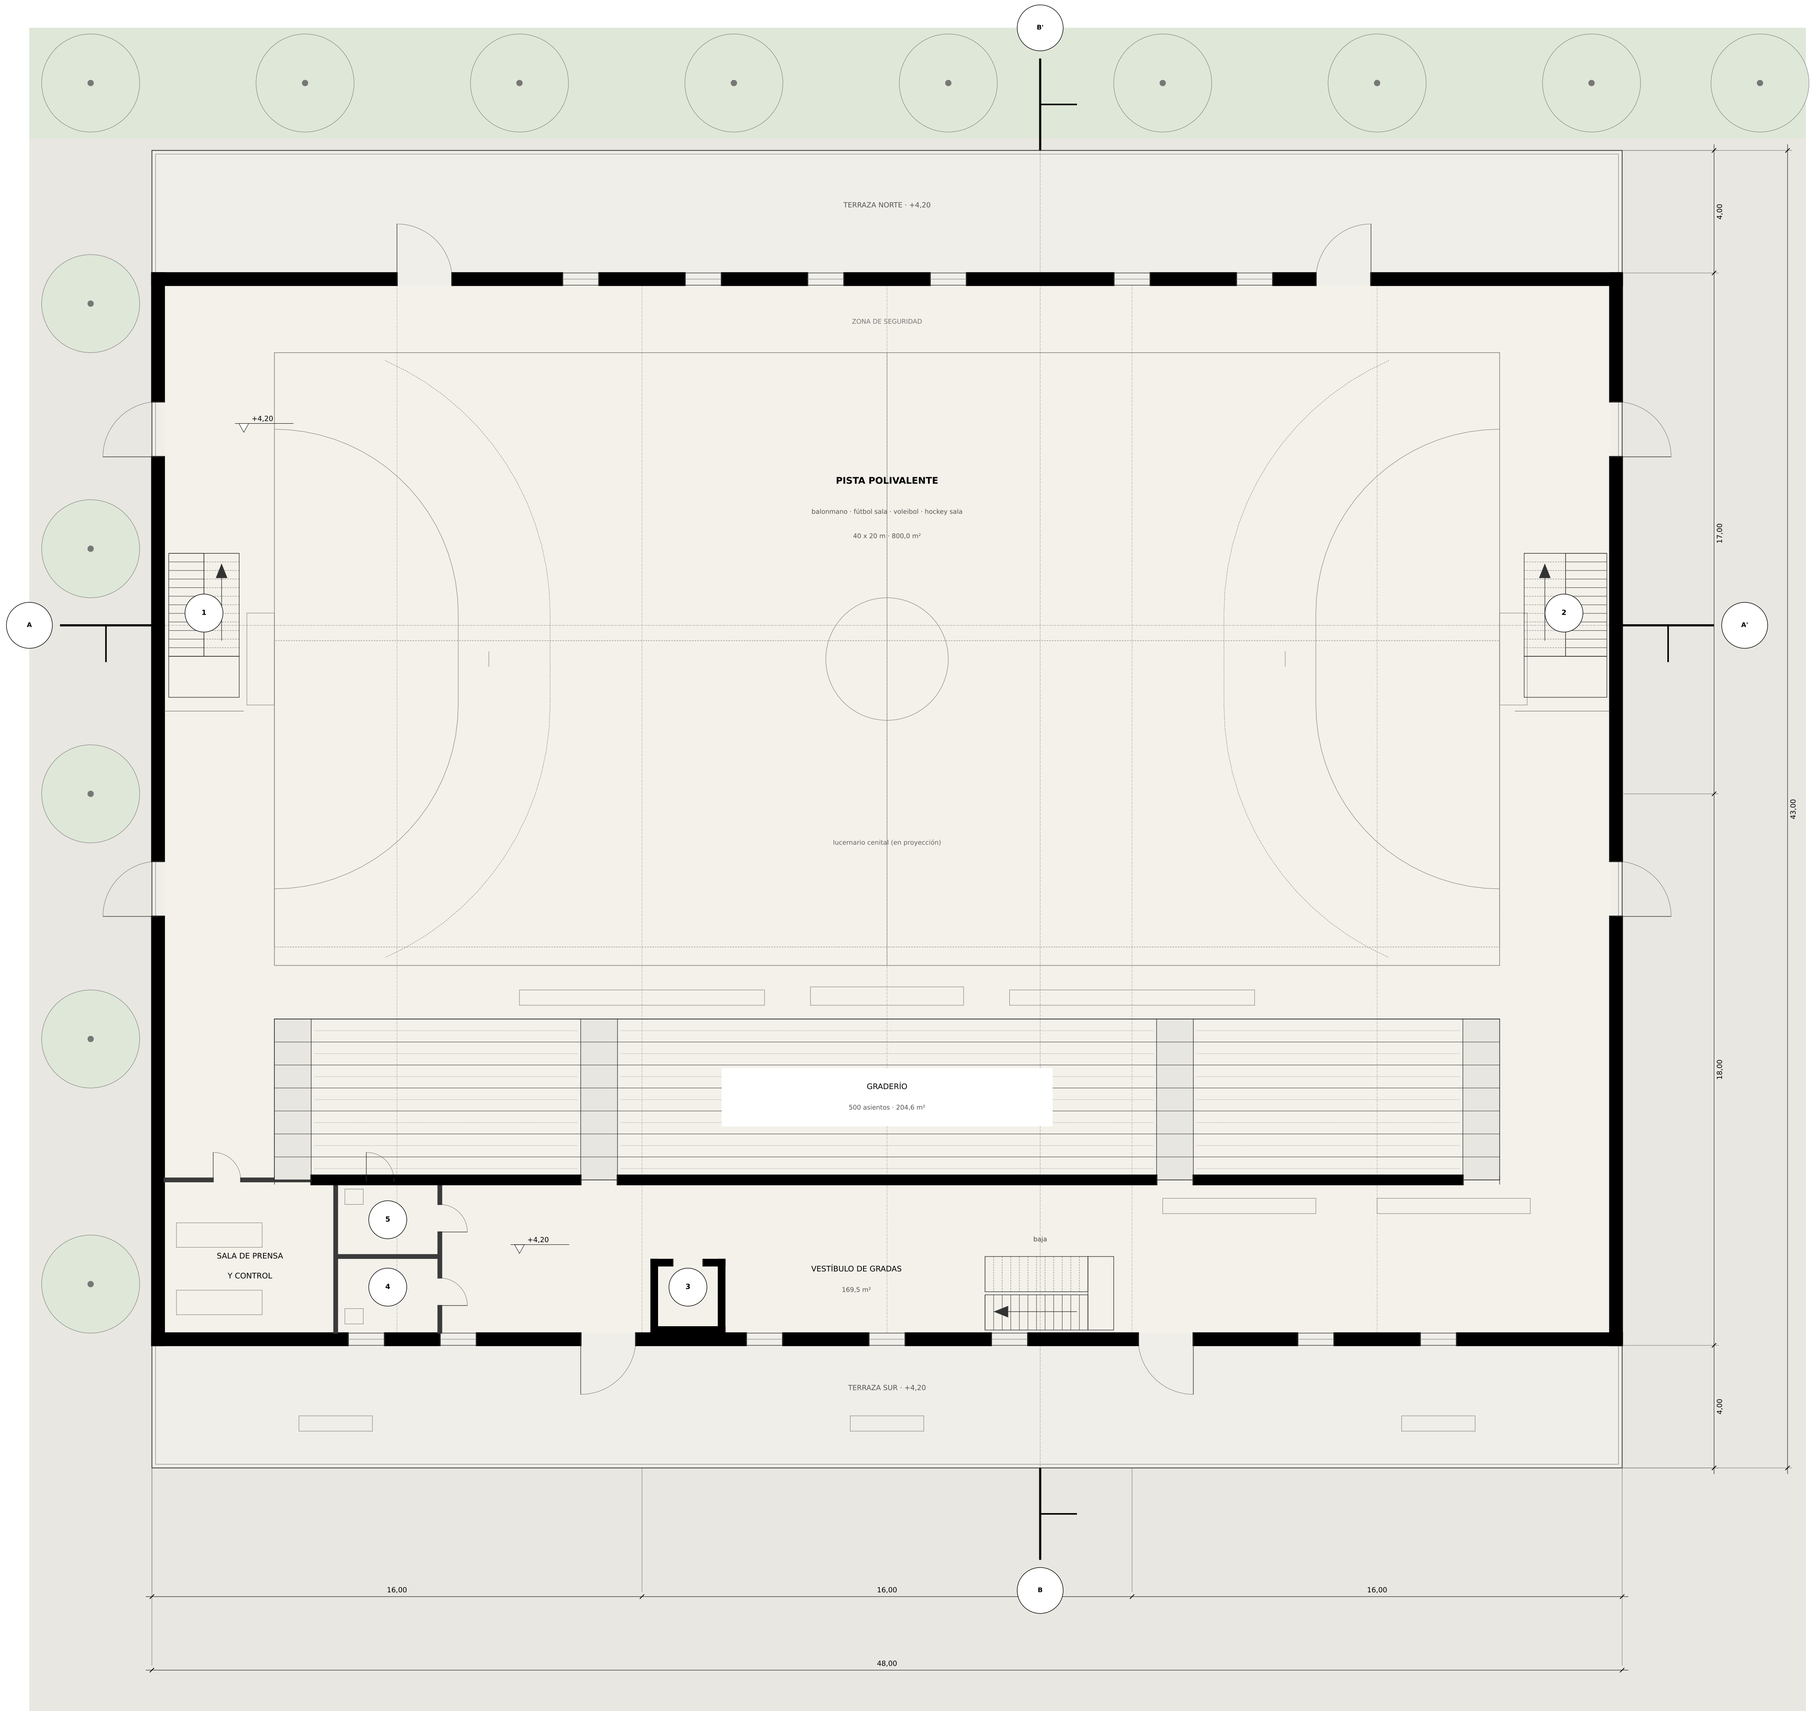

PLANTA ALTA (+4,20)

E 1:100

N

0 1 2 5 10 m

LEYENDA

PLANTA ALTA · leyenda

1	Escalera de jugadores (desemboca junto a pista)	12,1 m²
2	Escalera este / evacuación	14,1 m²
3	Ascensor	
4	Aseos H y M	16,0 m²
5	Aseo adaptado (en aseos M)	

CASO_002 · PROPUESTA A	Escala 1:100 (A1)
PLANTA ALTA · PISTA Y GRADERÍO	ANTEPROYECTO
	Lámina P02