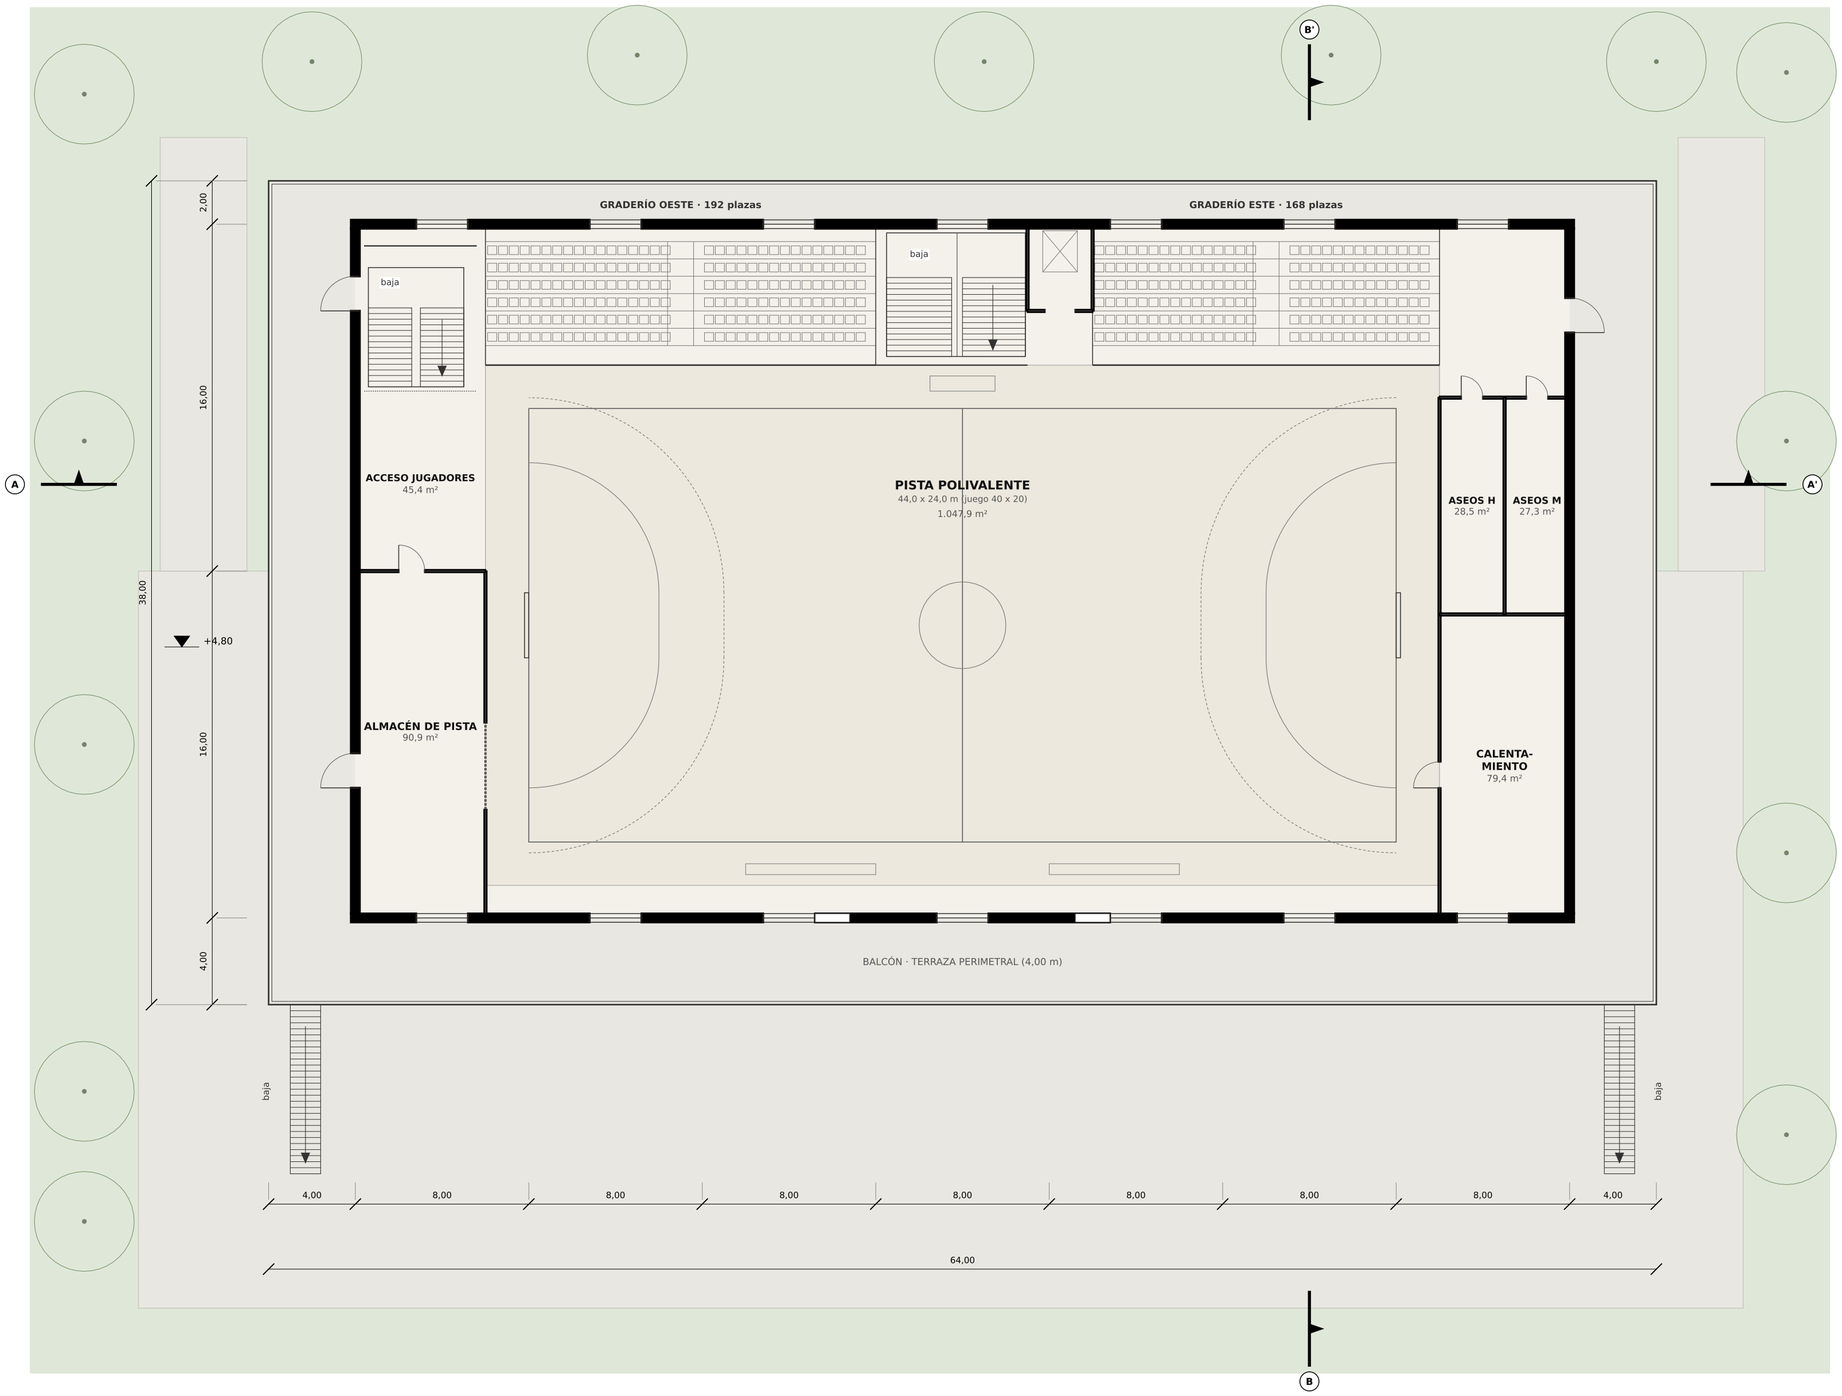


N

SUPERFICIES ÚTILES · PLANTA PRIMERA

PISTA POLIVALENTE	1.047,9 m²
GRADERÍO OESTE	110,5 m²
GRADERÍO ESTE	98,1 m²
ALMACÉN DE PISTA	90,9 m²
ACCESO JUGADORES	45,4 m²
CALENTA- MIENTO	79,4 m²
ASEOS H	28,5 m²
ASEOS M	27,3 m²
TOTAL ÚTIL	**1.527,9 m²**

Forjado de balcón y terraza: 64 x 38 m

Pista de juego 40 x 20 m + 2 m de seguridad

Altura libre del pabellón: 8,00 m (+12,80)

Ventanas: banda vertical translúcida, 7 por fachada

Aforo graderío: 360 plazas sentadas

PLANTA PRIMERA · PABELLÓN

E 1:200

0 1 2 5 10 m

CASO_002 · PROPUESTA C

PLANTA PRIMERA · PABELLÓN +4,80

Anteproyecto

LÁMINA **P02**

ESCALA **E 1:200**

FORMATO **A2**