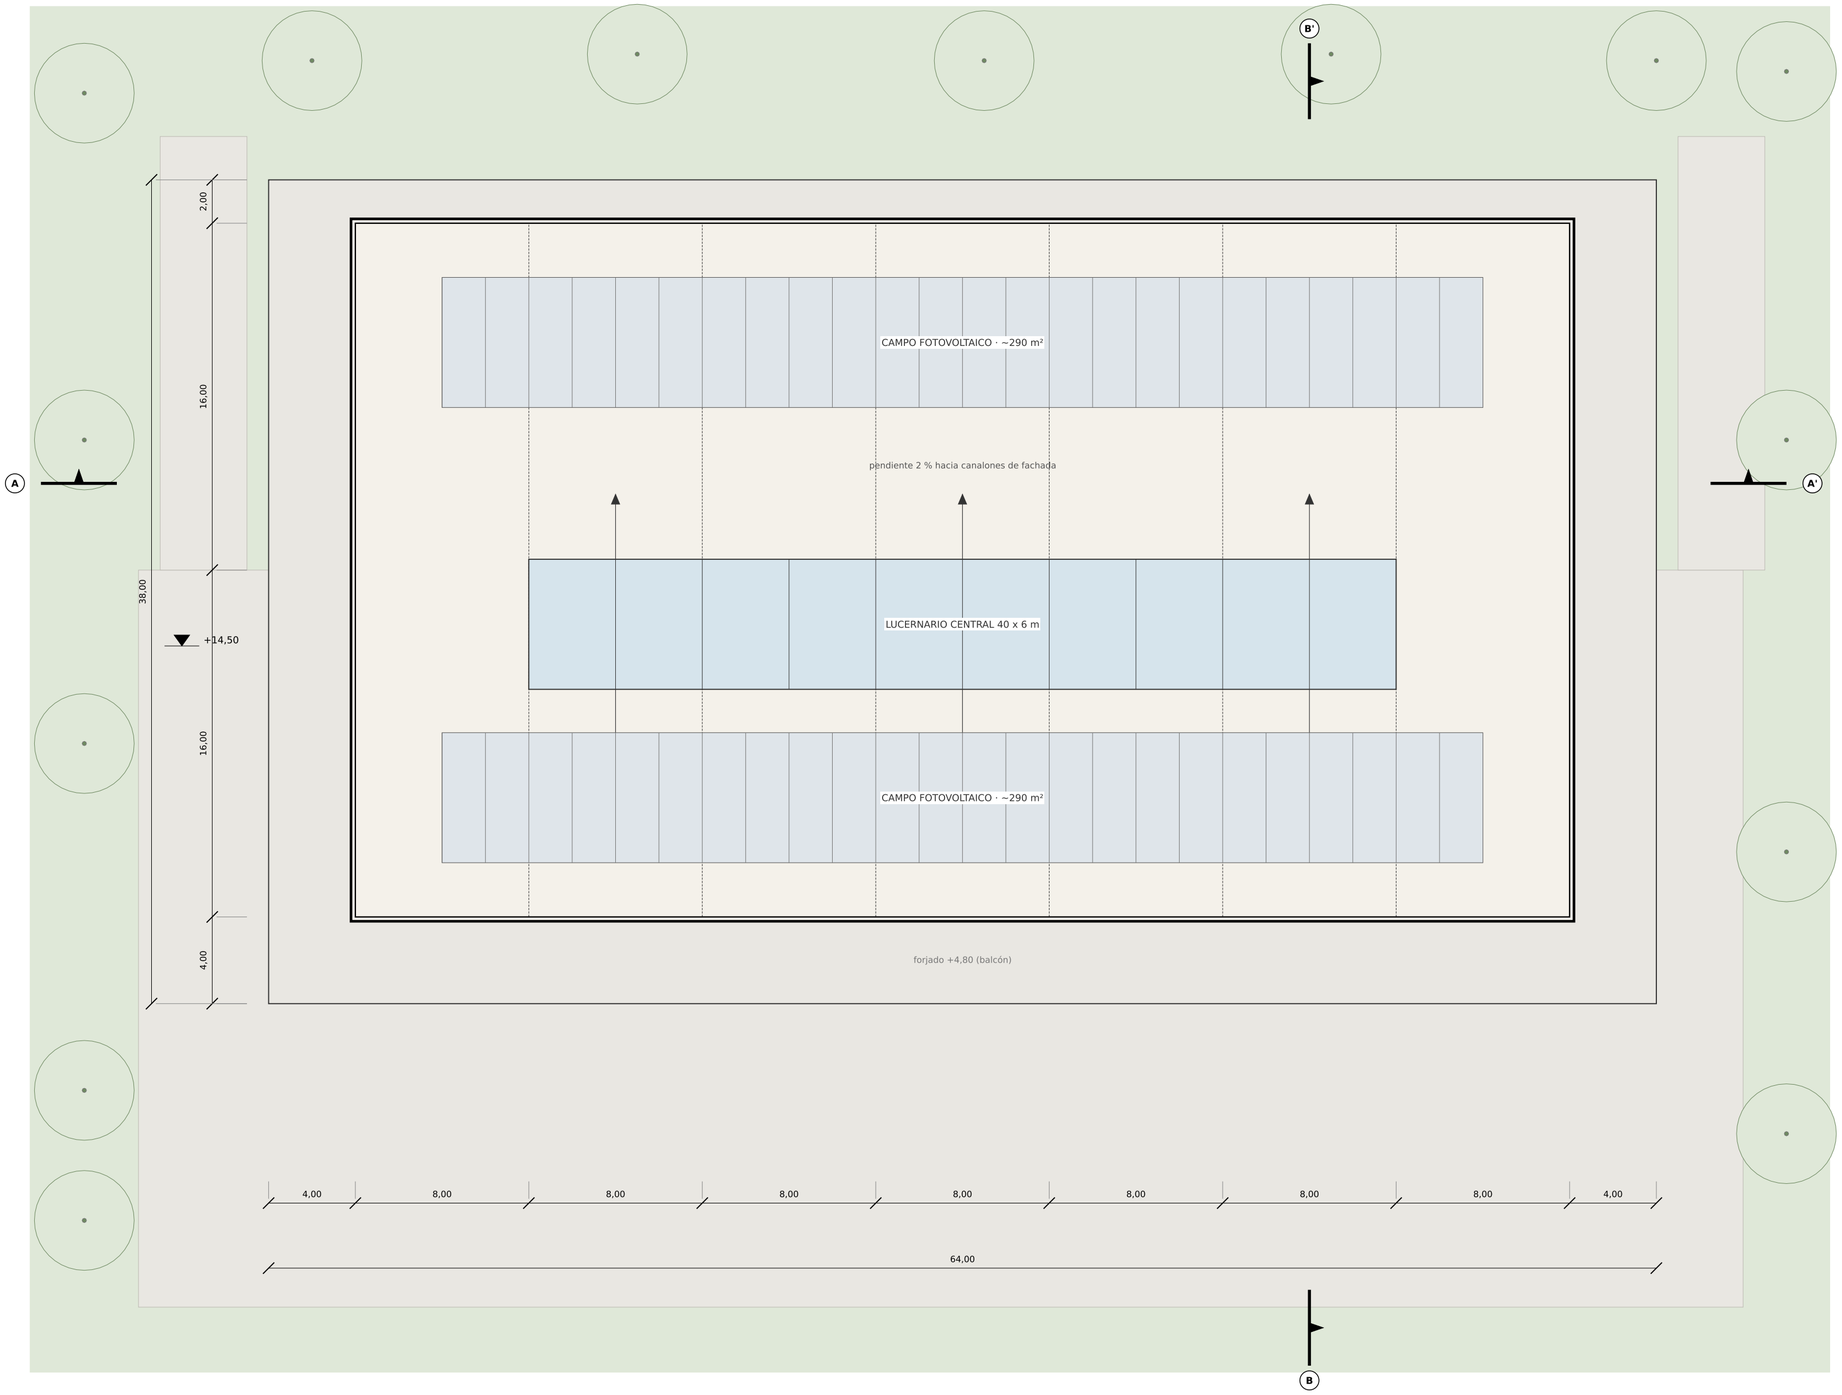

N

CUBIERTA

Cubierta plana invertida, pendiente 2 %
Cerchas de madera laminada cada 8,00 m
Luz libre de las cerchas: 32,00 m
Lucernario central de policarbonato translúcido: luz difusa sin deslumbramiento
Campo fotovoltaico en las dos bandas laterales; retranqueo del peto 1,5 m
Recogida de pluviales en canalones perimetrales; cota de cumbrera +14,50
Peto de remate +15,00

PLANTA DE CUBIERTA

E 1:200

0 1 2 5 10 m

CASO_002 · PROPUESTA C

PLANTA DE CUBIERTA · +14,50

Anteproyecto

LÁMINA **P03**

ESCALA **E 1:200**

FORMATO **A2**