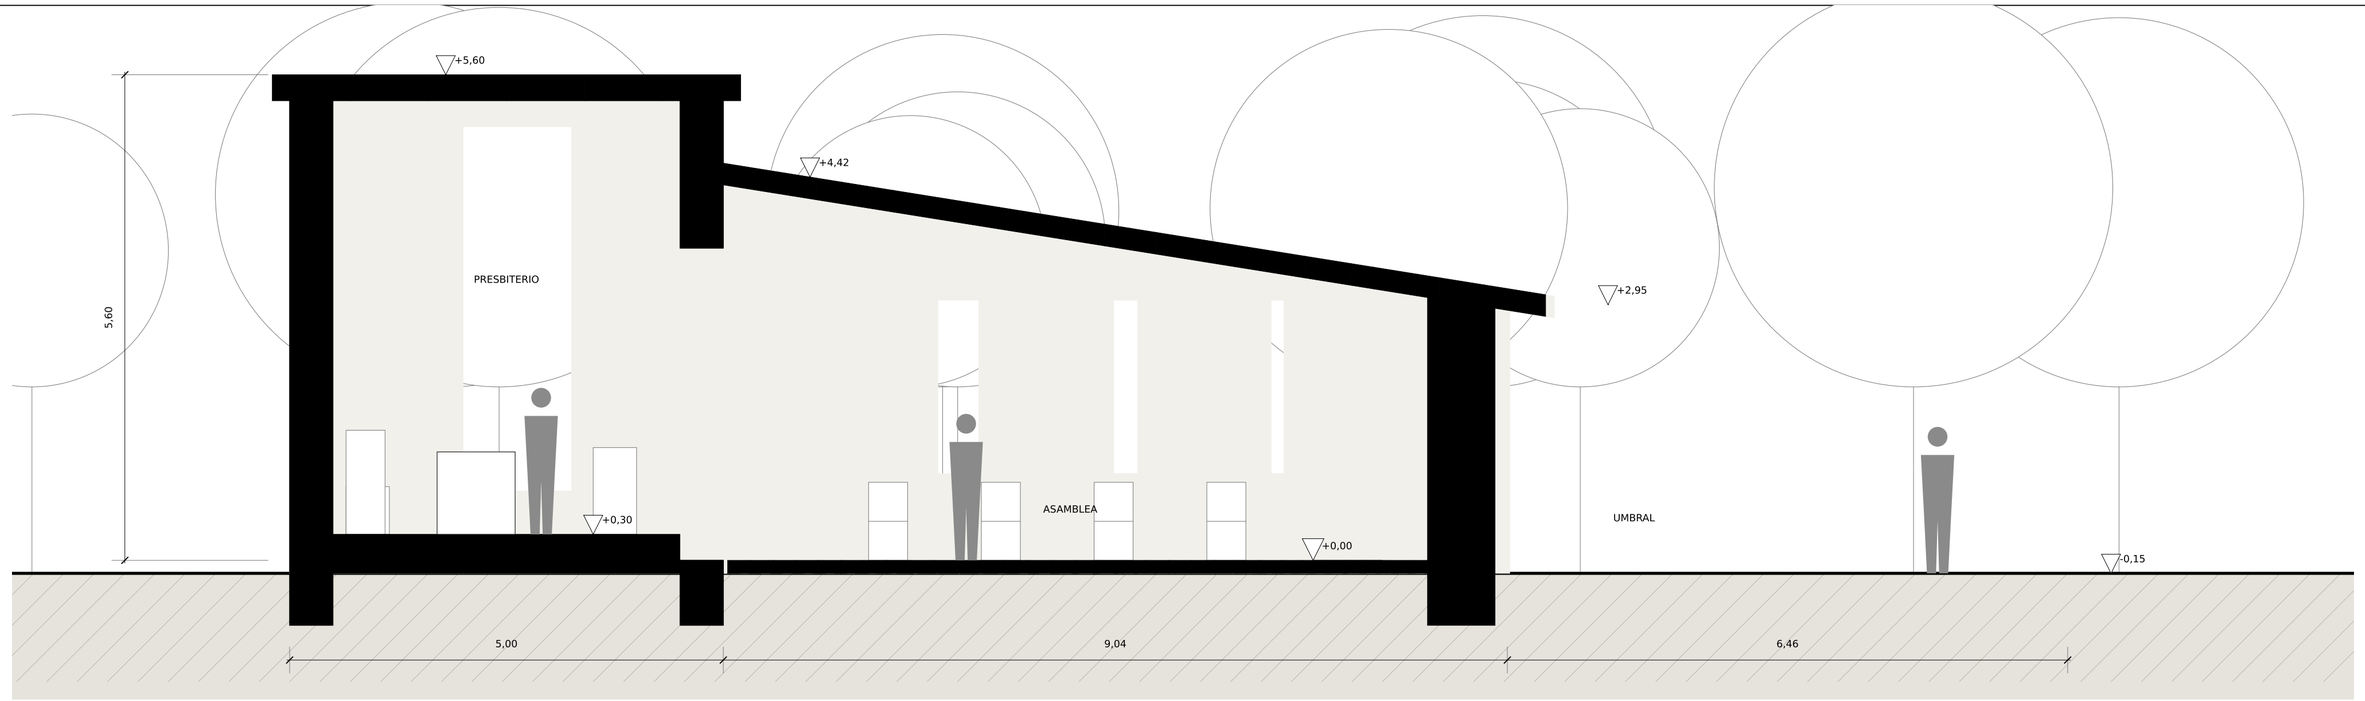

SECCIÓN LONGITUDINAL A-A'

E 1:50

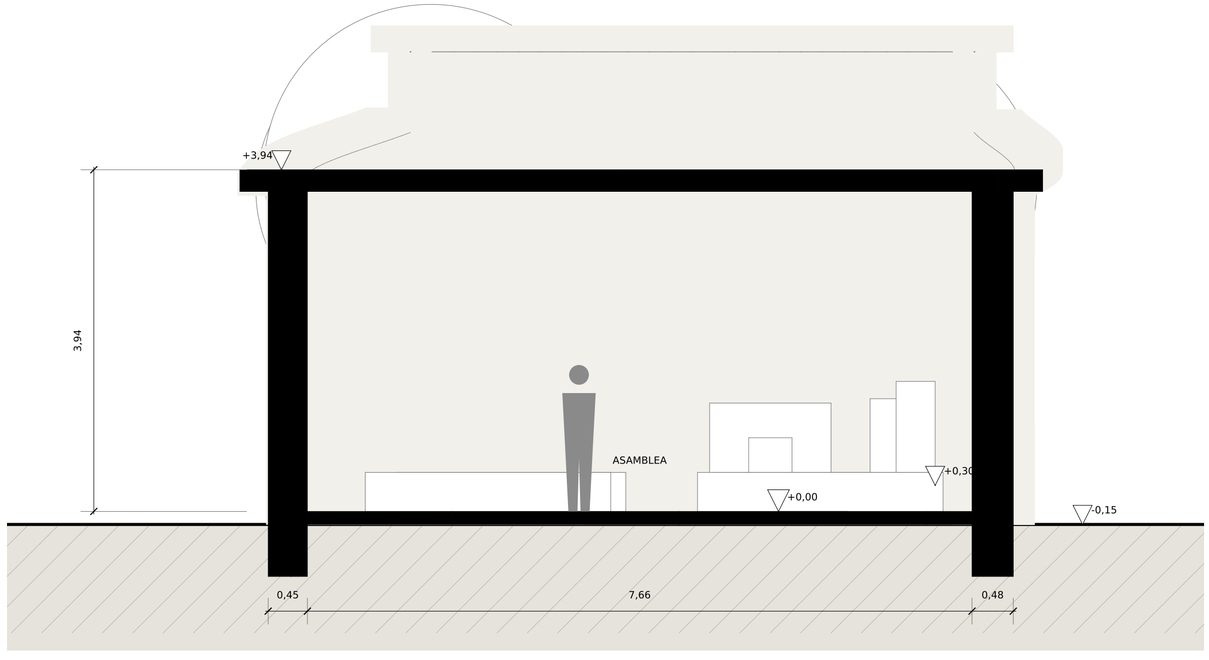

SECCIÓN TRANSVERSAL B-B'

E 1:50

0 1 2 5 10 m

Notas constructivas

Muros: mampostería de piedra y ladrillo recuperados de la vivienda desmontada, trabados con mortero de cal; espesor 0,45 m (nave) y 0,50 m (presbiterio).

Zapata corrida de piedra a -0,75 m; solera de cal y grava sobre encachado, a ±0,00.

Cubierta: vigas y cabios de madera recuperada, tablero y teja cerámica reutilizada; alero de 0,55 m contra el sol de verano; pendiente 16 % hacia el este.

Presbiterio: volumen elevado con rendija norte (luz rasante del mediodía austral).

Ventilación cruzada por rendijas con postigos de madera en muros norte y sur.

Sin instalaciones: luz natural y velas; agua de lluvia en depósito; aseo seco.

CASO_003 · PROPUESTA A	Anteproyecto	
Secciones A-A' y B-B'	Escala 1:50	**S01**