


SECCIÓN LONGITUDINAL A-A'

E 1:250



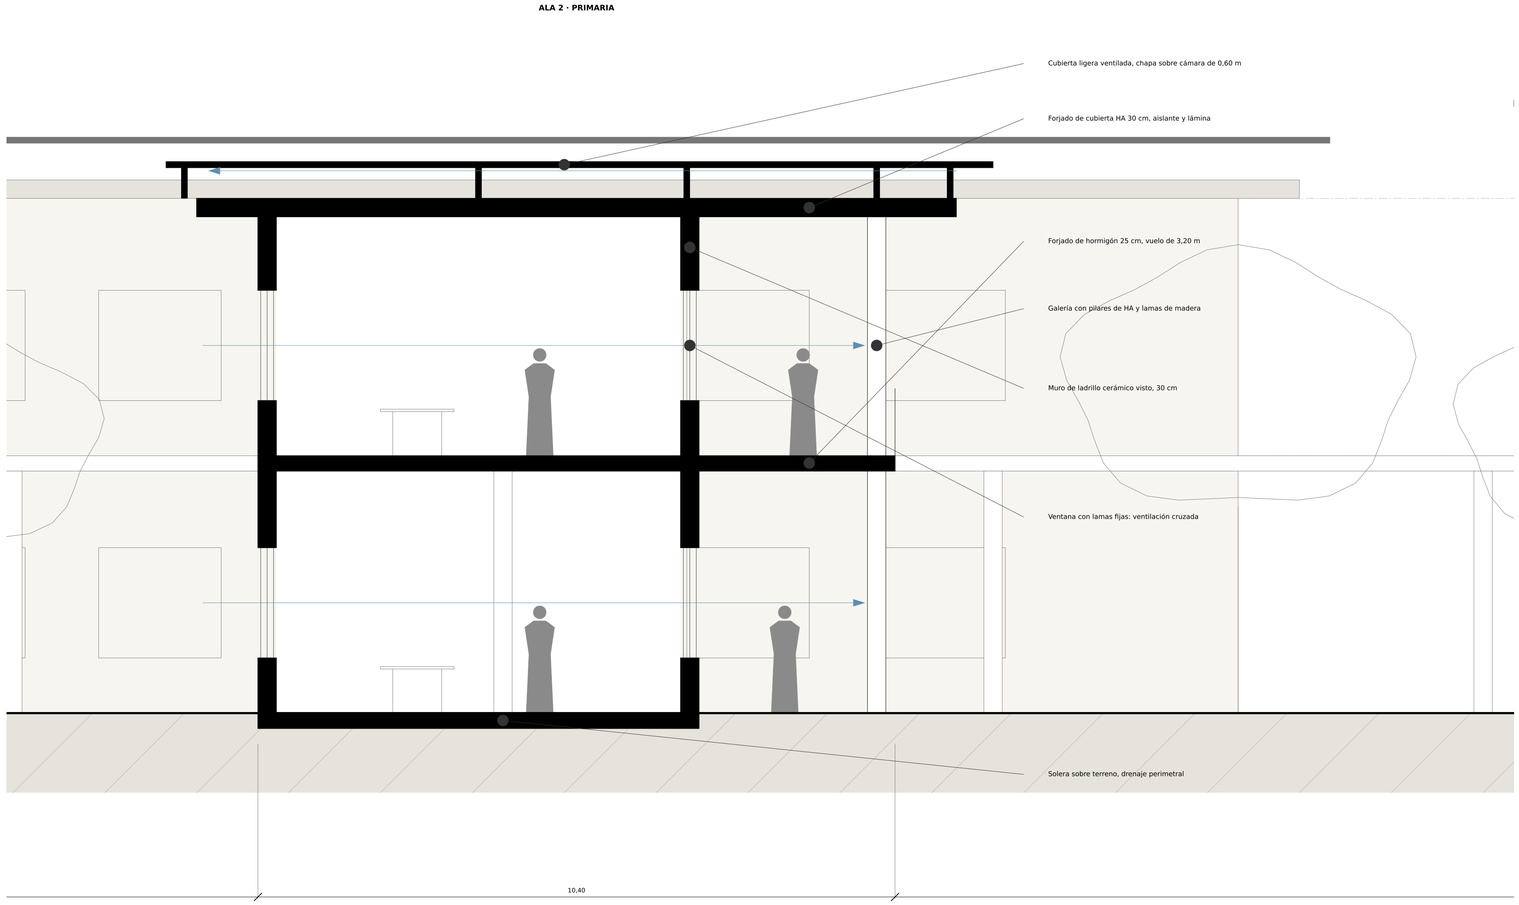

DETALLE · ALA 2 · SECCIÓN TIPO

E 1:50



NOTAS

Niveles: +0,00 PB · +4,20 PP · +8,40 forjado de cubierta · +9,00 cubierta ligera

Flechas azules: ventilación cruzada por las aulas y chimenea de aire en la cámara de cubierta

Alturas libres: PB 3,95 m · PP 3,90 m; la galería norte sombrea y protege del sol de mediodía

CASO_004 · PROPUESTA A	Centro educativo · anteproyecto
	Lámina **S01**
Sección longitudinal A-A'	Escala **1:250 / 1:50**
	Anteproyecto A