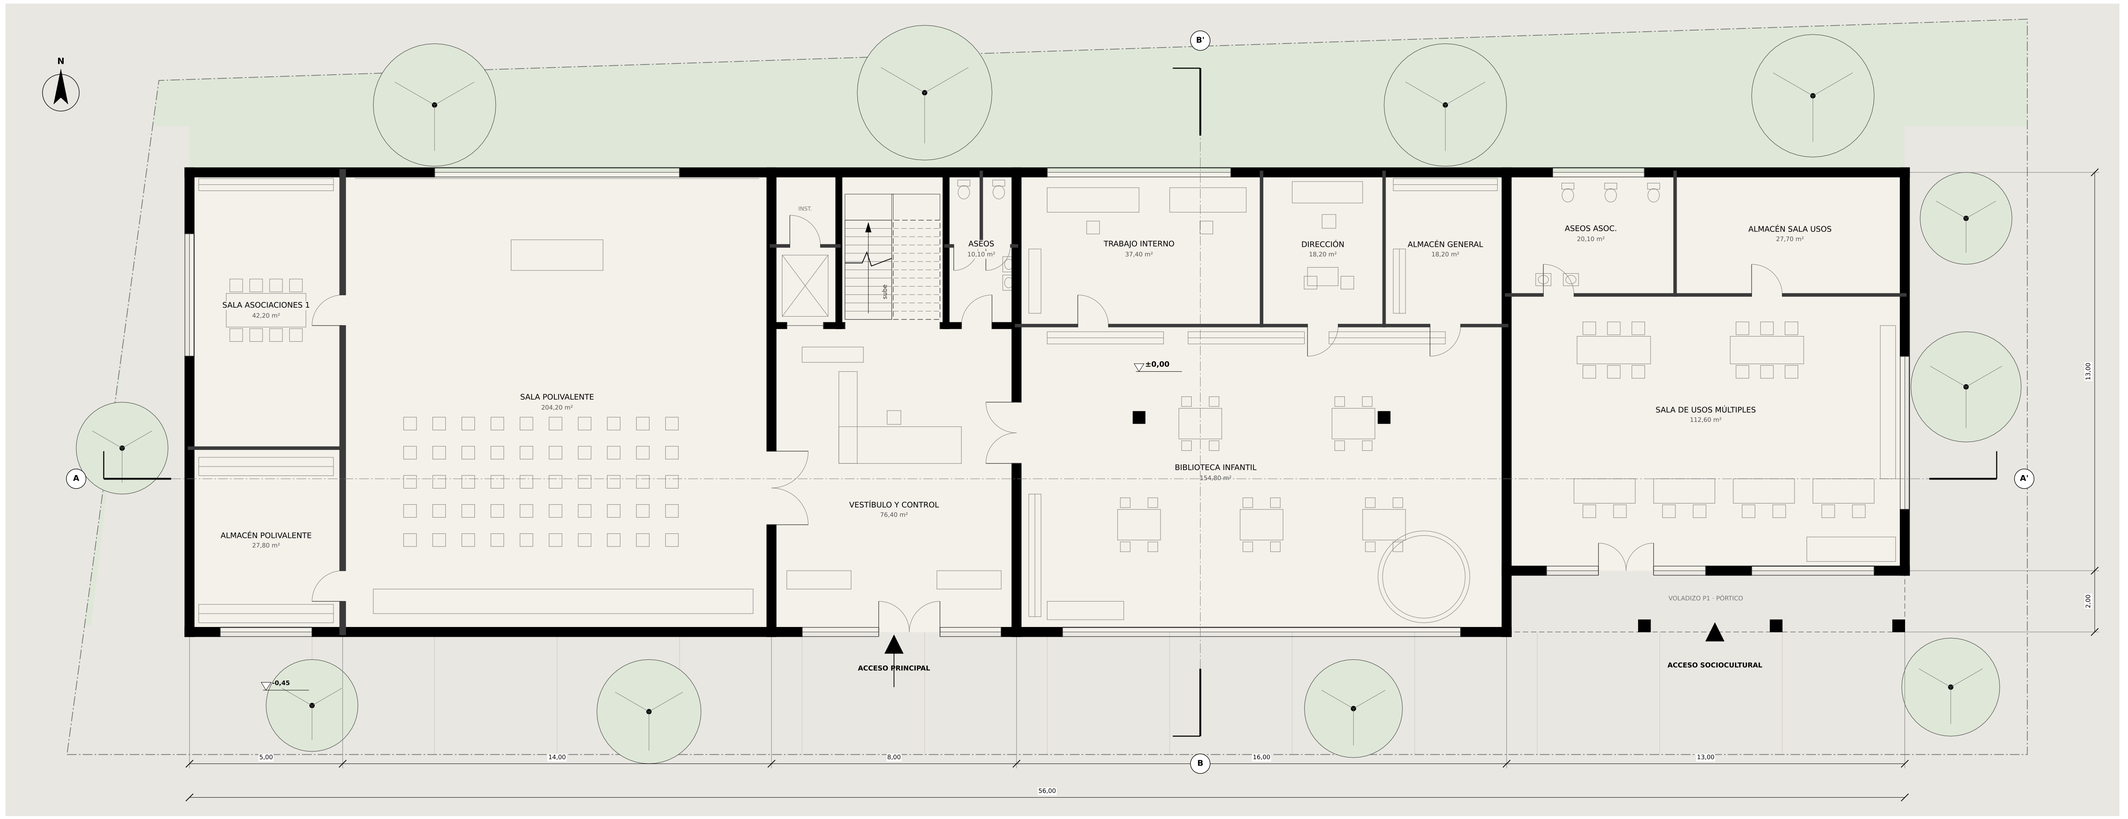


PLANTA BAJA +0,00

E 1:100

0 1 2 5 10 m

RELACIÓN DE ESTANCIAS · PLANTA BAJA

1	Sala polivalente	204,20 m²	5	Aseos	10,10 m²	12	Almacén general	18,20 m²
2	Almacén polivalente	27,80 m²	9	Biblioteca infantil	154,80 m²	13	Sala de usos múltiples	112,60 m²
3	Sala asociaciones 1	42,20 m²	10	Trabajo interno	37,40 m²	14	Aseos asoc.	20,10 m²
4	Vestíbulo y control	76,40 m²	11	Dirección	18,20 m²	15	Almacén sala usos	27,70 m²

CASO_005 · PROPUESTA A	ESCALA E 1:100	LÁMINA **P01**
PLANTA BAJA	Anteproyecto	Biblioteca y centro sociocultural