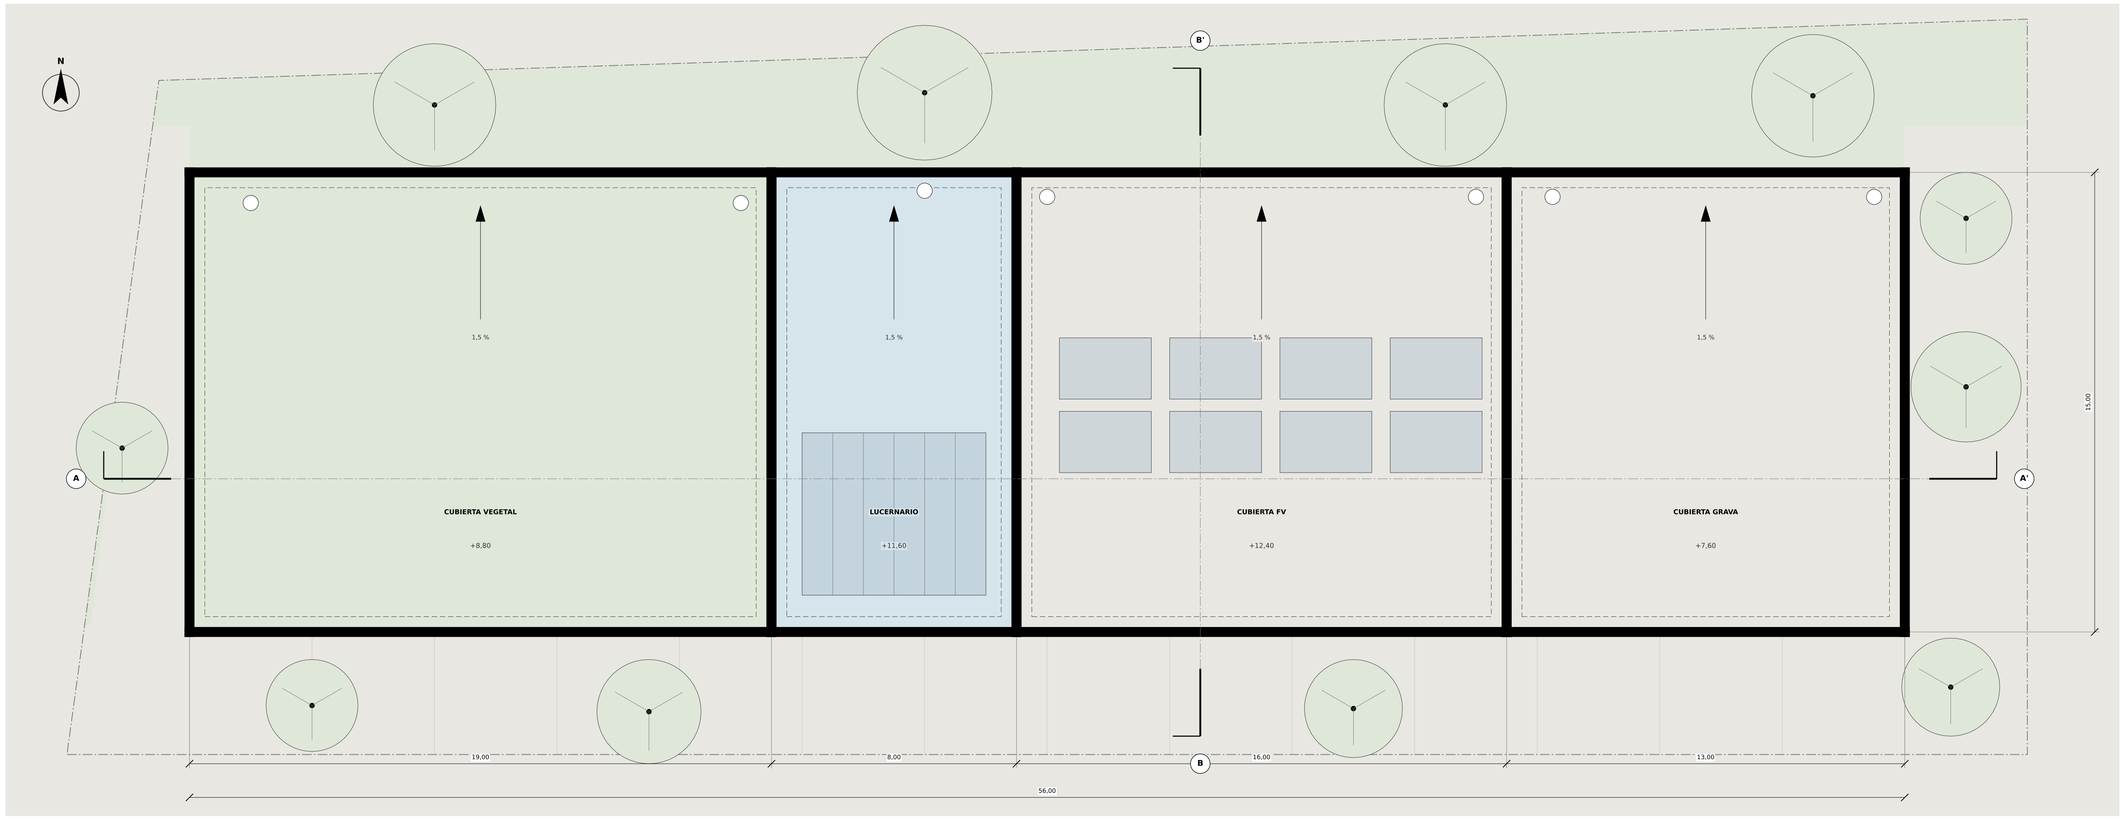

PLANTA DE CUBIERTAS

E 1:100

0 1 2 5 10 m

Cubiertas planas invertidas con pendiente del 1,5 % hacia la fachada norte y bajantes (círculos).

Cotas de coronación de peto. Volumen oeste: cubierta vegetal extensiva. Volumen central: paneles fotovoltaicos.

CASO_005 · PROPUESTA A	ESCALA E 1:100	LÁMINA **P04**
PLANTA DE CUBIERTAS	Anteproyecto	Biblioteca y centro sociocultural