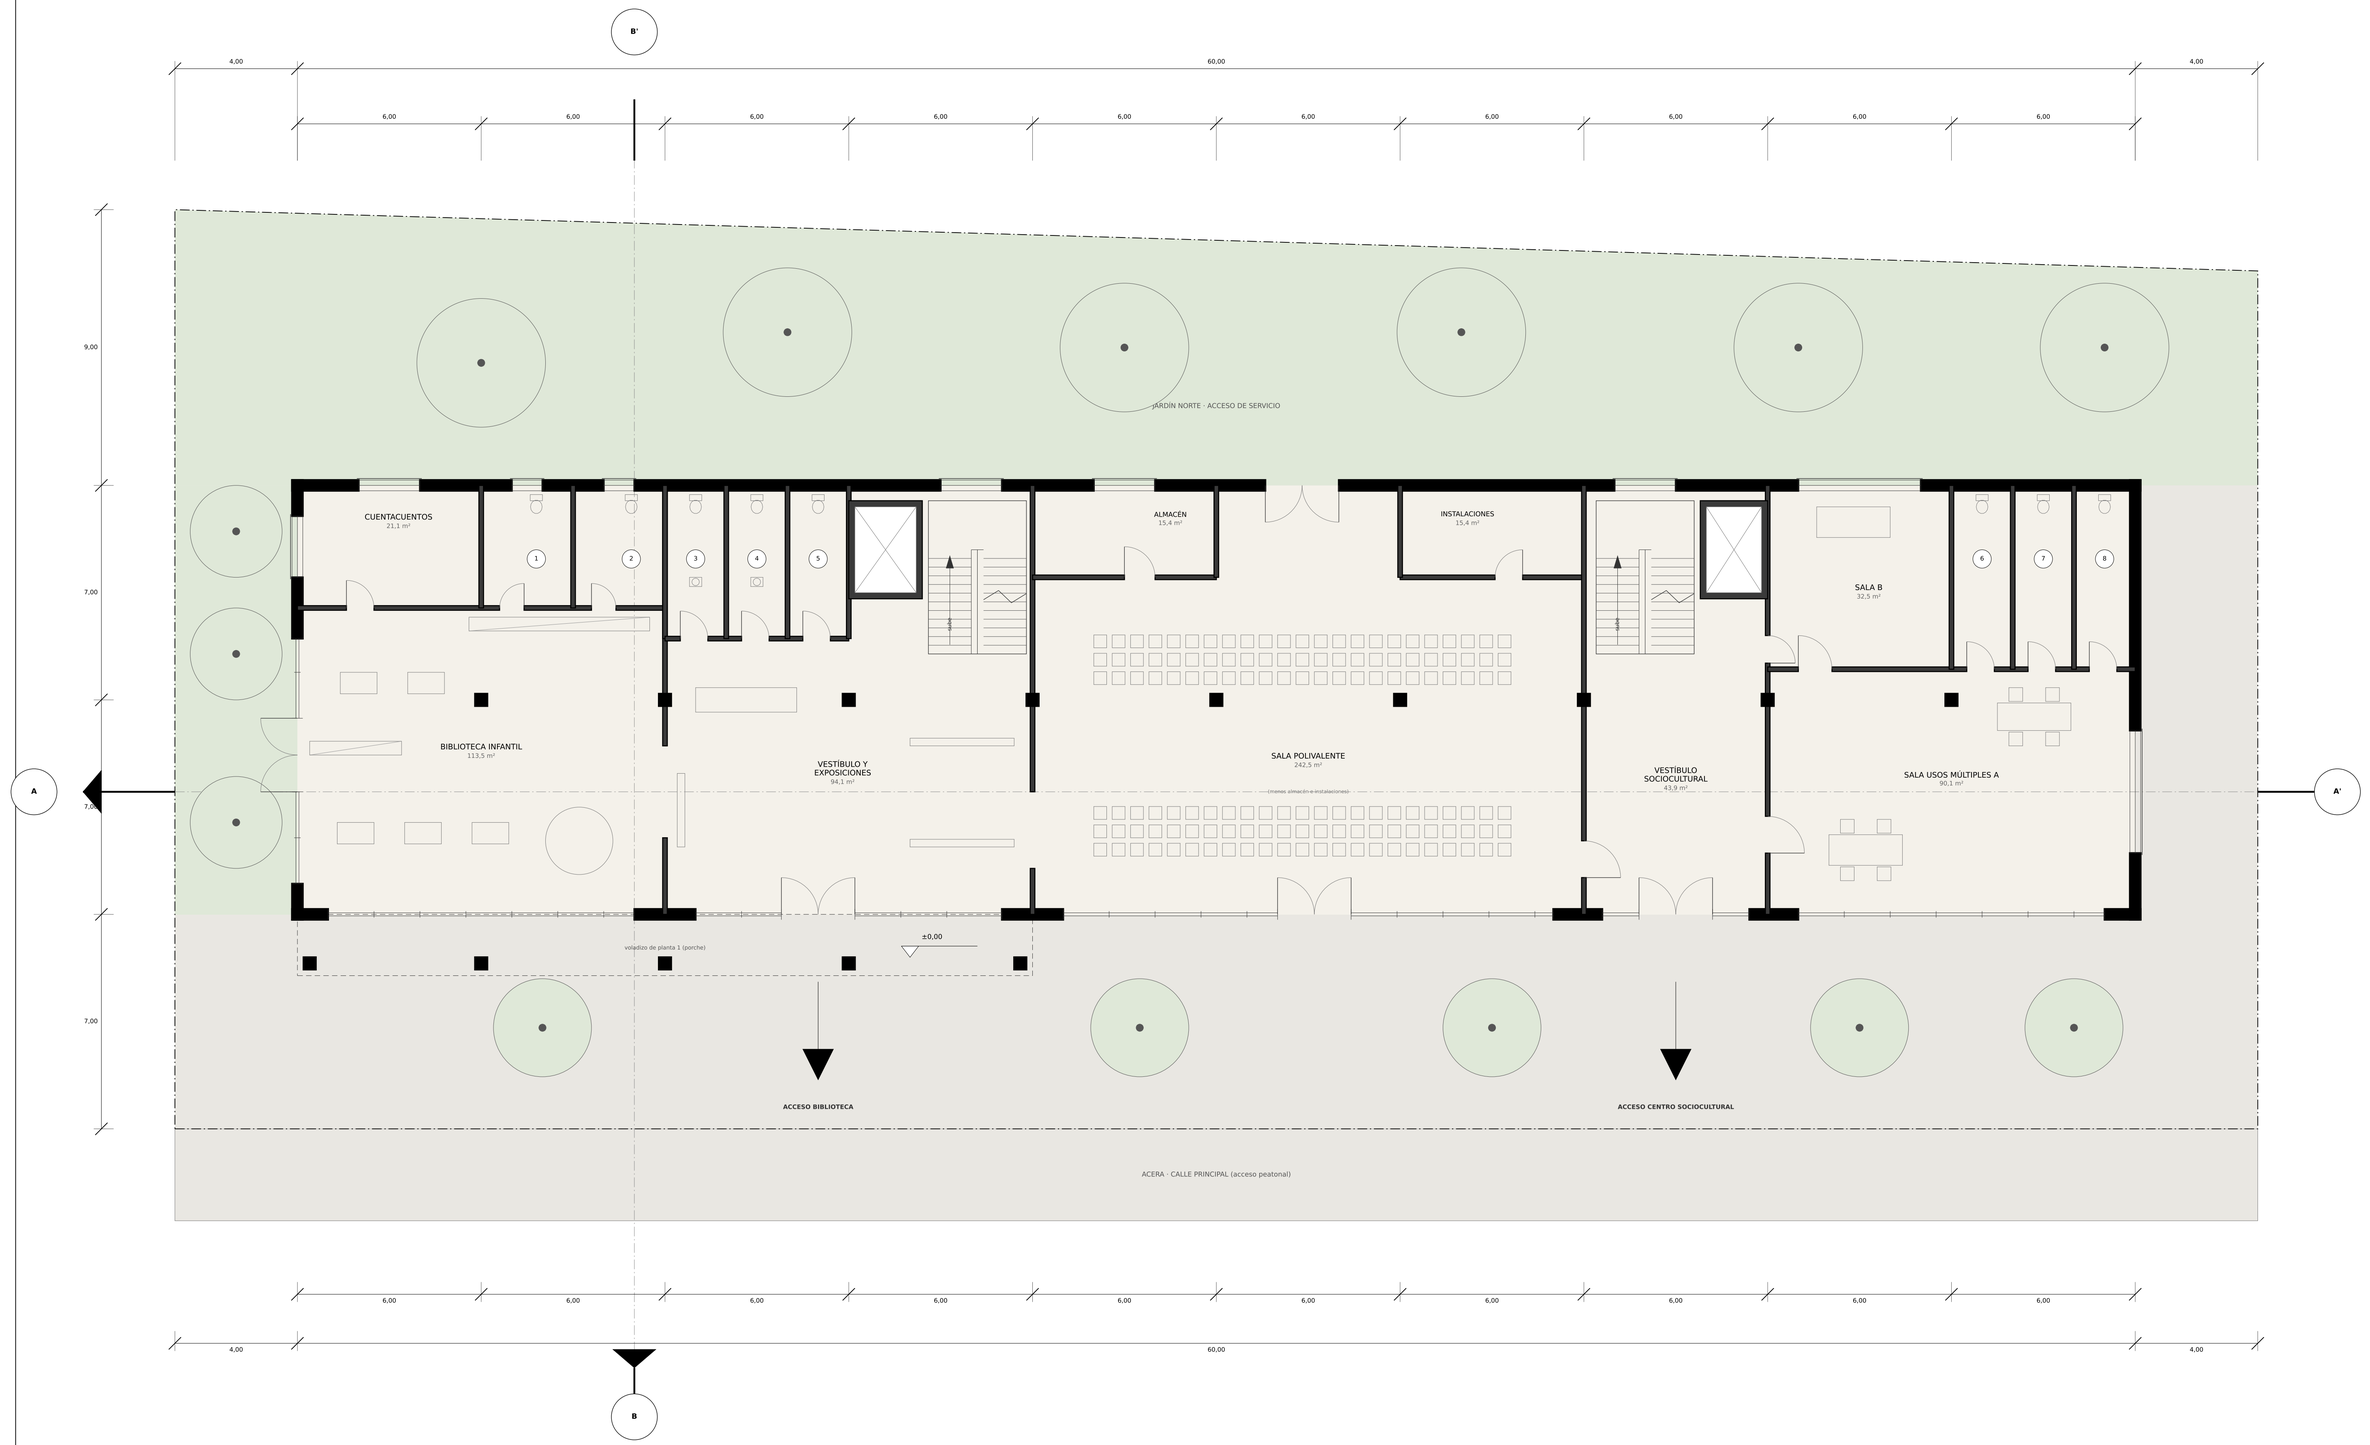


LEYENDA Y SUPERFICIES ÚTILES (m²)

(3)	ASEO MASC.	8,0
(4)	ASEO FEM.	8,0
(5)	ASEO ADAPTADO	8,0
	BIBLIOTECA INFANTIL	113,5
	CUENTACUENTOS	21,1
(1)	ASEO INFANTIL 1	10,0
(2)	ASEO INFANTIL 2	10,0
	VESTÍBULO Y EXPOSICIONES	94,1
	NÚCLEO ESCALERA/ASCENSOR	32,5
	SALA POLIVALENTE	211,7
	ALMACÉN	15,4
	INSTALACIONES	15,4
	VESTÍBULO SOCIOCULTURAL	43,9
	NÚCLEO ESCALERA/ASCENSOR SOCIOCULTURAL	32,5
	SALA USOS MÚLTIPLES A	90,1
	SALA B	32,5
(6)	ASEO MASC.	9,7
(7)	ASEO FEM.	9,7
(8)	ASEO ADAPTADO	9,7

Total útil de la planta: 775,8 m² (superficies netas aproximadas, sin muros)

PLANTA BAJA

E 1:100

0 1 2 5 10 m

CASO_005 · PROPUESTA C

Planta baja

Biblioteca pública y centro sociocultural de barrio

Anteproyecto

Escala: E 1:100

Lámina: **P01**