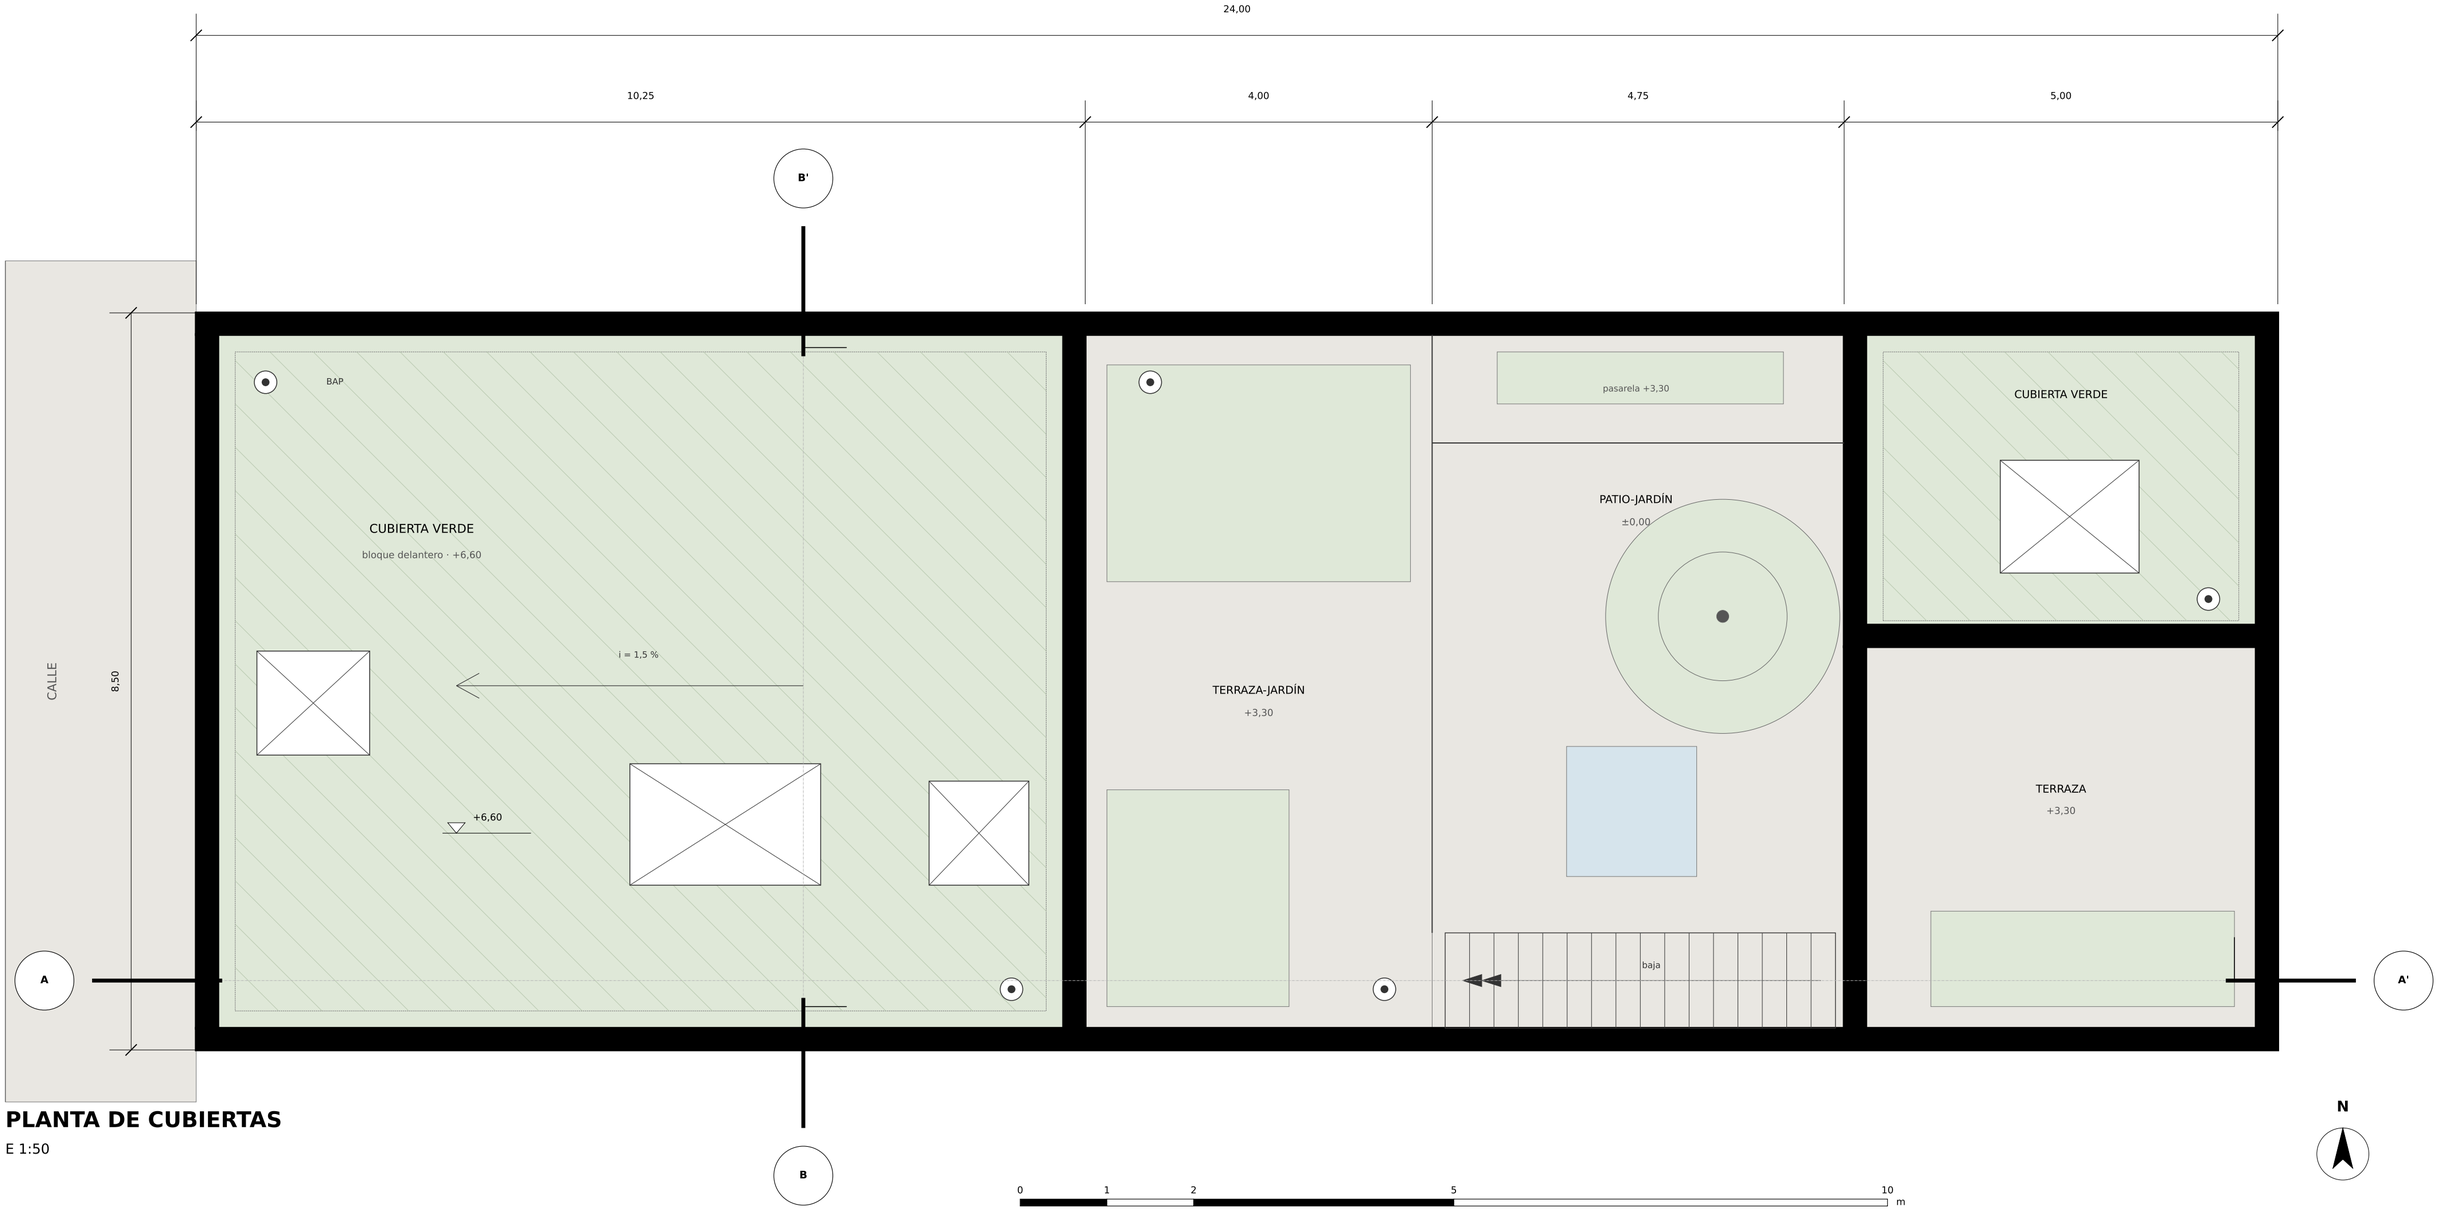

PLANTA DE CUBIERTAS

E 1:50

NOTAS

Cotas en metros. ±0,00 = cota del solar (plano). Altura libre interior 3,00 m; forjados de 0,30 m.

Muros de carga de fábrica armada/hormigón de 0,25 m (negro). Tabiques de 0,10 m (gris oscuro).

Orientación: calle al oeste-suroeste (aquí, oeste); medianeras al norte y al sur.

Cortes A–A' (longitudinal, mirando al norte) y B–B' (transversal, mirando al este).

Cubiertas verdes extensivas (sustrato 12 cm) en bloques delantero (+6,60) y trasero (+6,30).

Evacuación a bajantes (BAP) con depósito de aguas pluviales para riego del patio.

CASO_006 · PROPUESTA A

Planta de cubiertas

Anteproyecto	Escala 1:50	**Lámina P03**