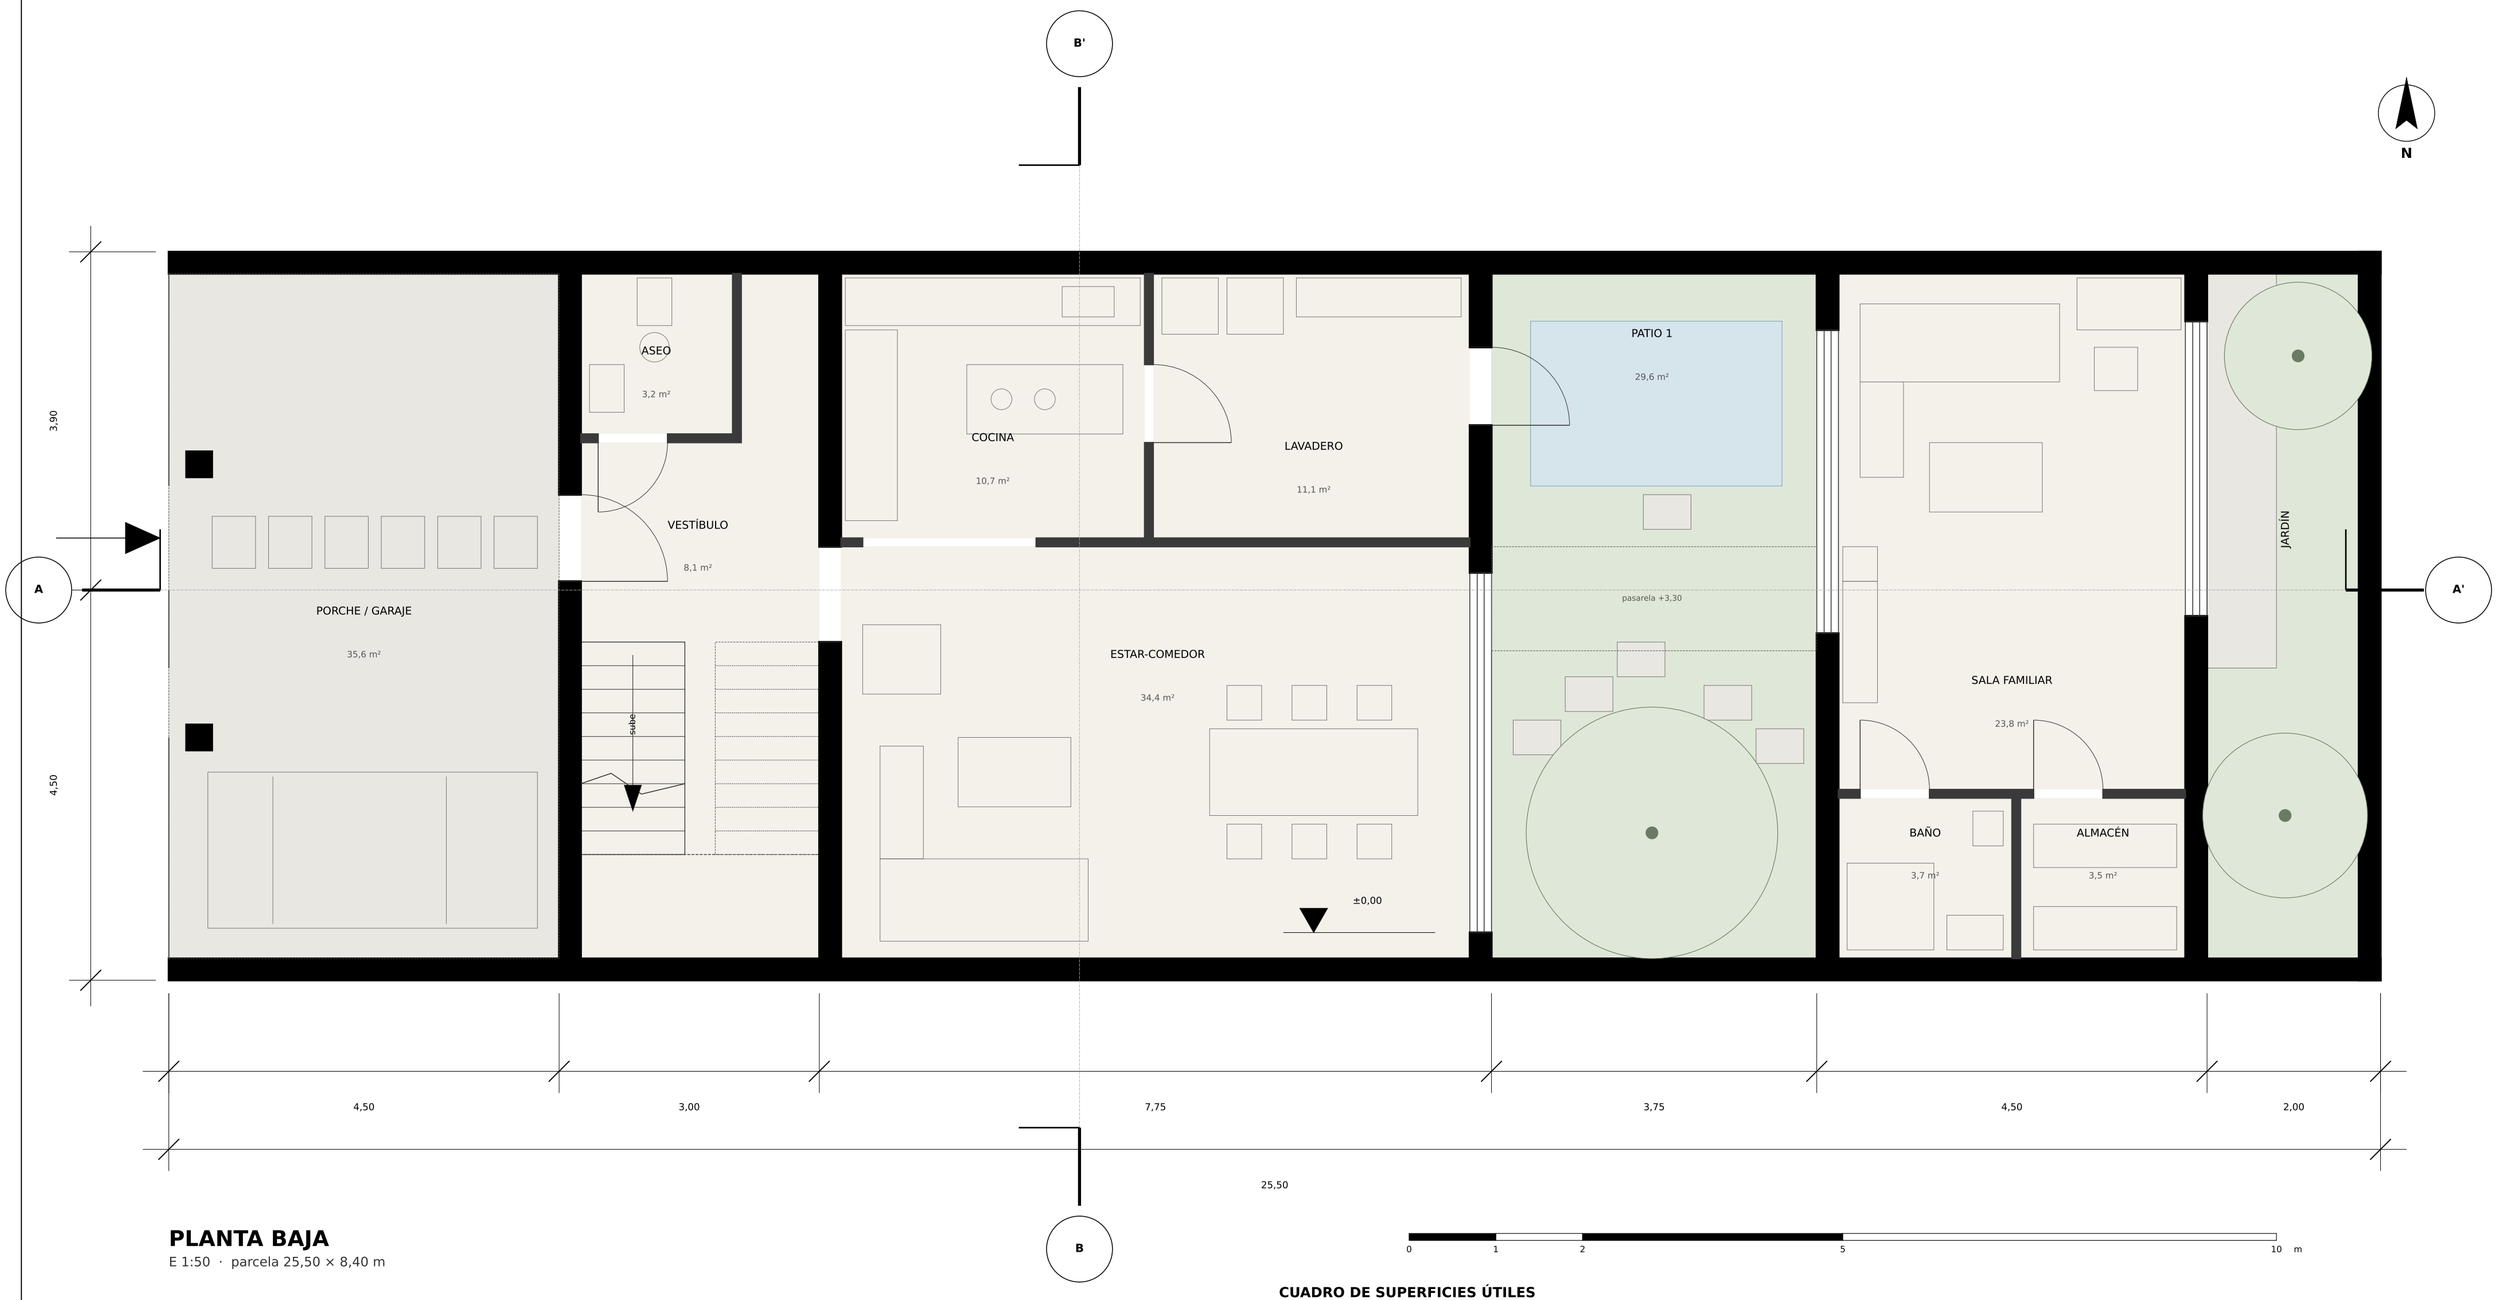

PLANTA BAJA

E 1:50 · parcela 25,50 × 8,40 m

LEYENDA

- Muro de hormigón / medianera (cortado)
- Tabique de ladrillo (cortado)
- Interior
- Exterior pavimentado
- Vegetación / patio
- Agua

Cotas en metros. Celosía de madera en trazo marrón claro.

CUADRO DE SUPERFICIES ÚTILES

ESCALERA	10,0 m²
VESTÍBULO	8,1 m²
ASEO	3,2 m²
ESTAR-COMEDOR	34,4 m²
COCINA	10,7 m²
LAVADERO	11,1 m²
BAÑO	3,7 m²
ALMACÉN	3,5 m²
SALA FAMILIAR	23,8 m²
TOTAL ÚTIL CERRADO	**108,6 m²**
Espacios exteriores / semicubiertos	79,0 m²

CASO_006 · PROPUESTA C

Anteproyecto · vivienda unifamiliar entre medianeras

Escala 1:50

Planta baja +0,00

Lámina **P01**

Anteproyecto