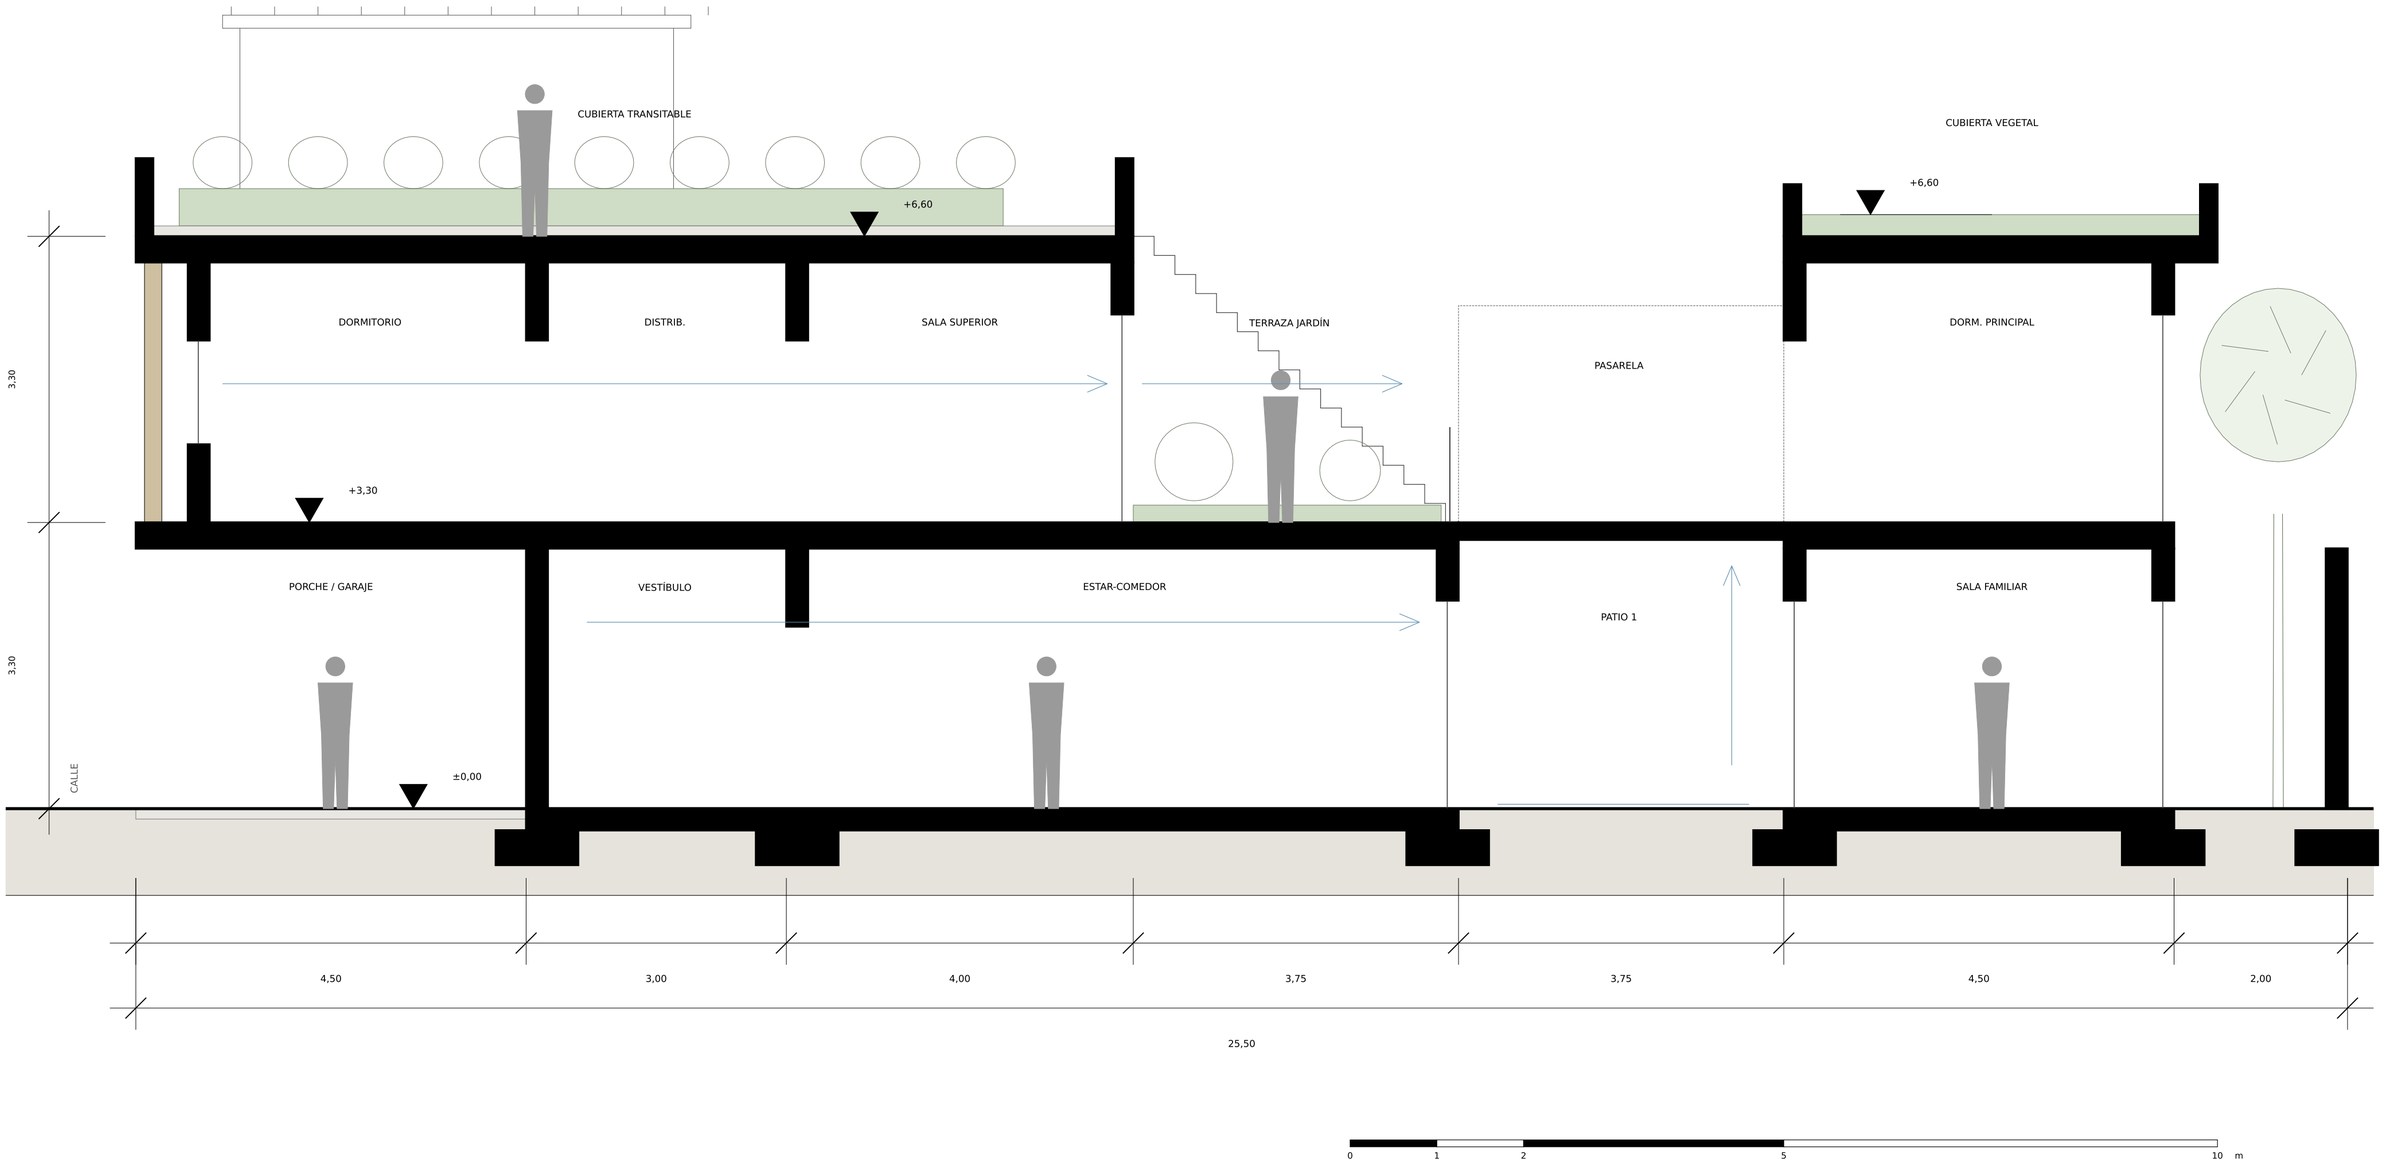

SECCIÓN LONGITUDINAL A-A'

E 1:50

Cota ±0,00 = rasante de calle y acceso. Forjados de hormigón 0,30 m; PB 3,00 m libres; P1 3,00 m libres.

Flechas azules: ventilación cruzada y efecto chimenea por el patio.

CASO_006 · PROPUESTA C Anteproyecto · vivienda unifamiliar entre medianeras	Escala 1:50	
Sección longitudinal A-A'	Lámina **S01**	Anteproyecto