
DETALLE D01

Sección constructiva de fachada

E 1:25 · fragmentos 1 y 2 conectados por las plantas 1.ª a 3.ª


FRAGMENTO 2 · ÚLTIMA PLANTA Y CUBIERTA

Carpintería, dintel, cubierta invertida y peto

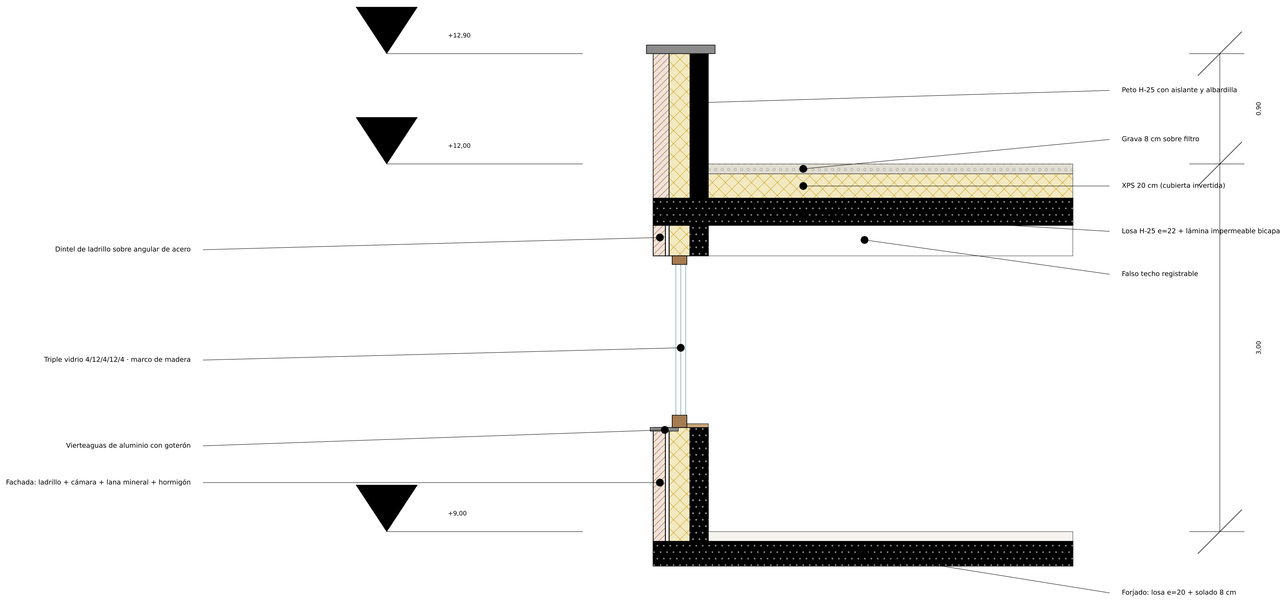

FRAGMENTO 1 · CIMENTACIÓN Y PLANTA BAJA

Arranque de la planta primera (+3,00)

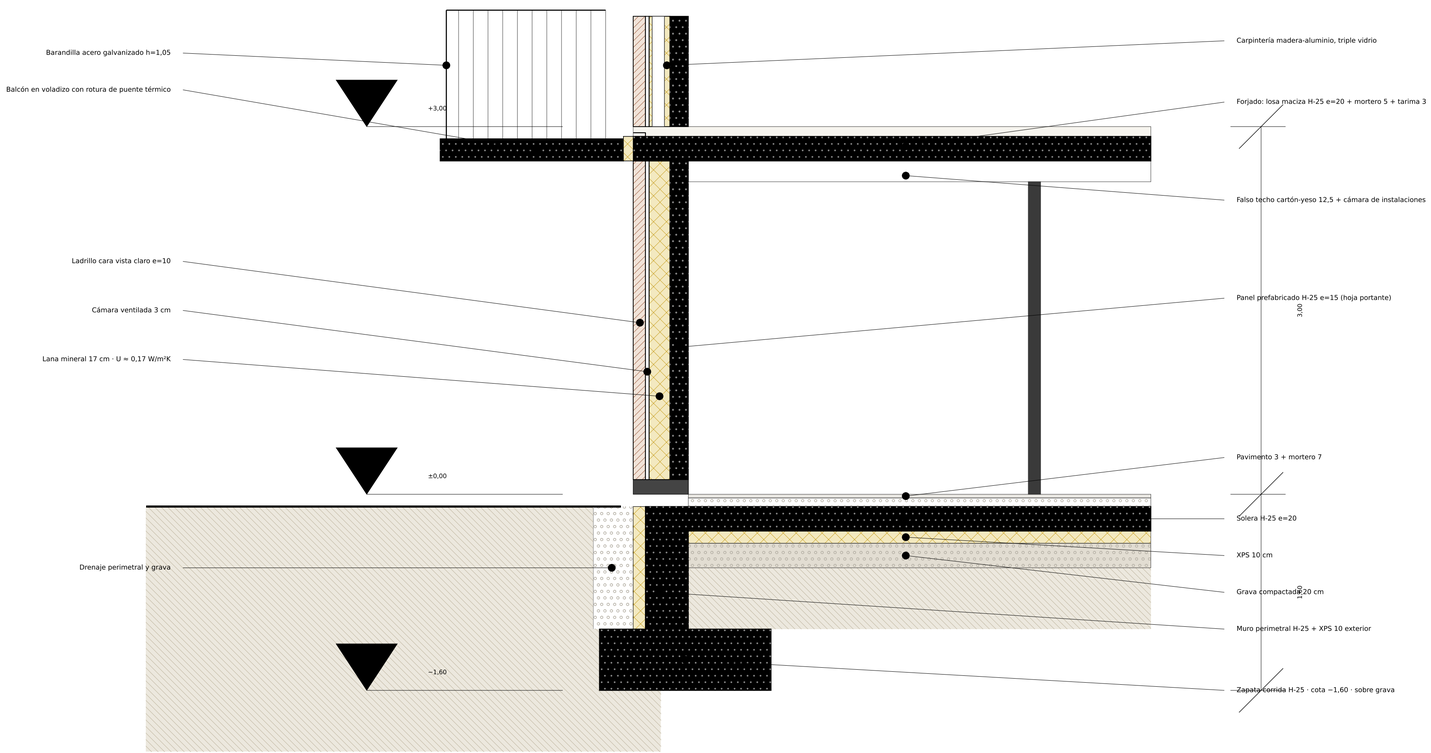

LEYENDA DE MATERIALES

- Hormigón armado H-25 (prefabricado y in situ)
- Ladrillo cara vista claro
- Aislante térmico (lana mineral / XPS)
- Grava / relleno drenante
- Madera (carpintería, pérgola)
- Terreno natural

PRESTACIONES (predimensionado)

Fachada: U = 0,17 W/m²K

Cubierta: U = 0,14 W/m²K (XPS 20 cm)

Solera: U = 0,25 W/m²K

Carpintería: Uw = 0,85 W/m²K (triple vidrio)

Balcones desolidarizados con rotura de puente térmico

Forjado de 3,00 m entre caras superiores de solado

CASO_007 · PROPUESTA A Anteproyecto	ESCALA	LÁMINA
Detalle constructivo de fachada · 1:25	**1:25**	**D01**