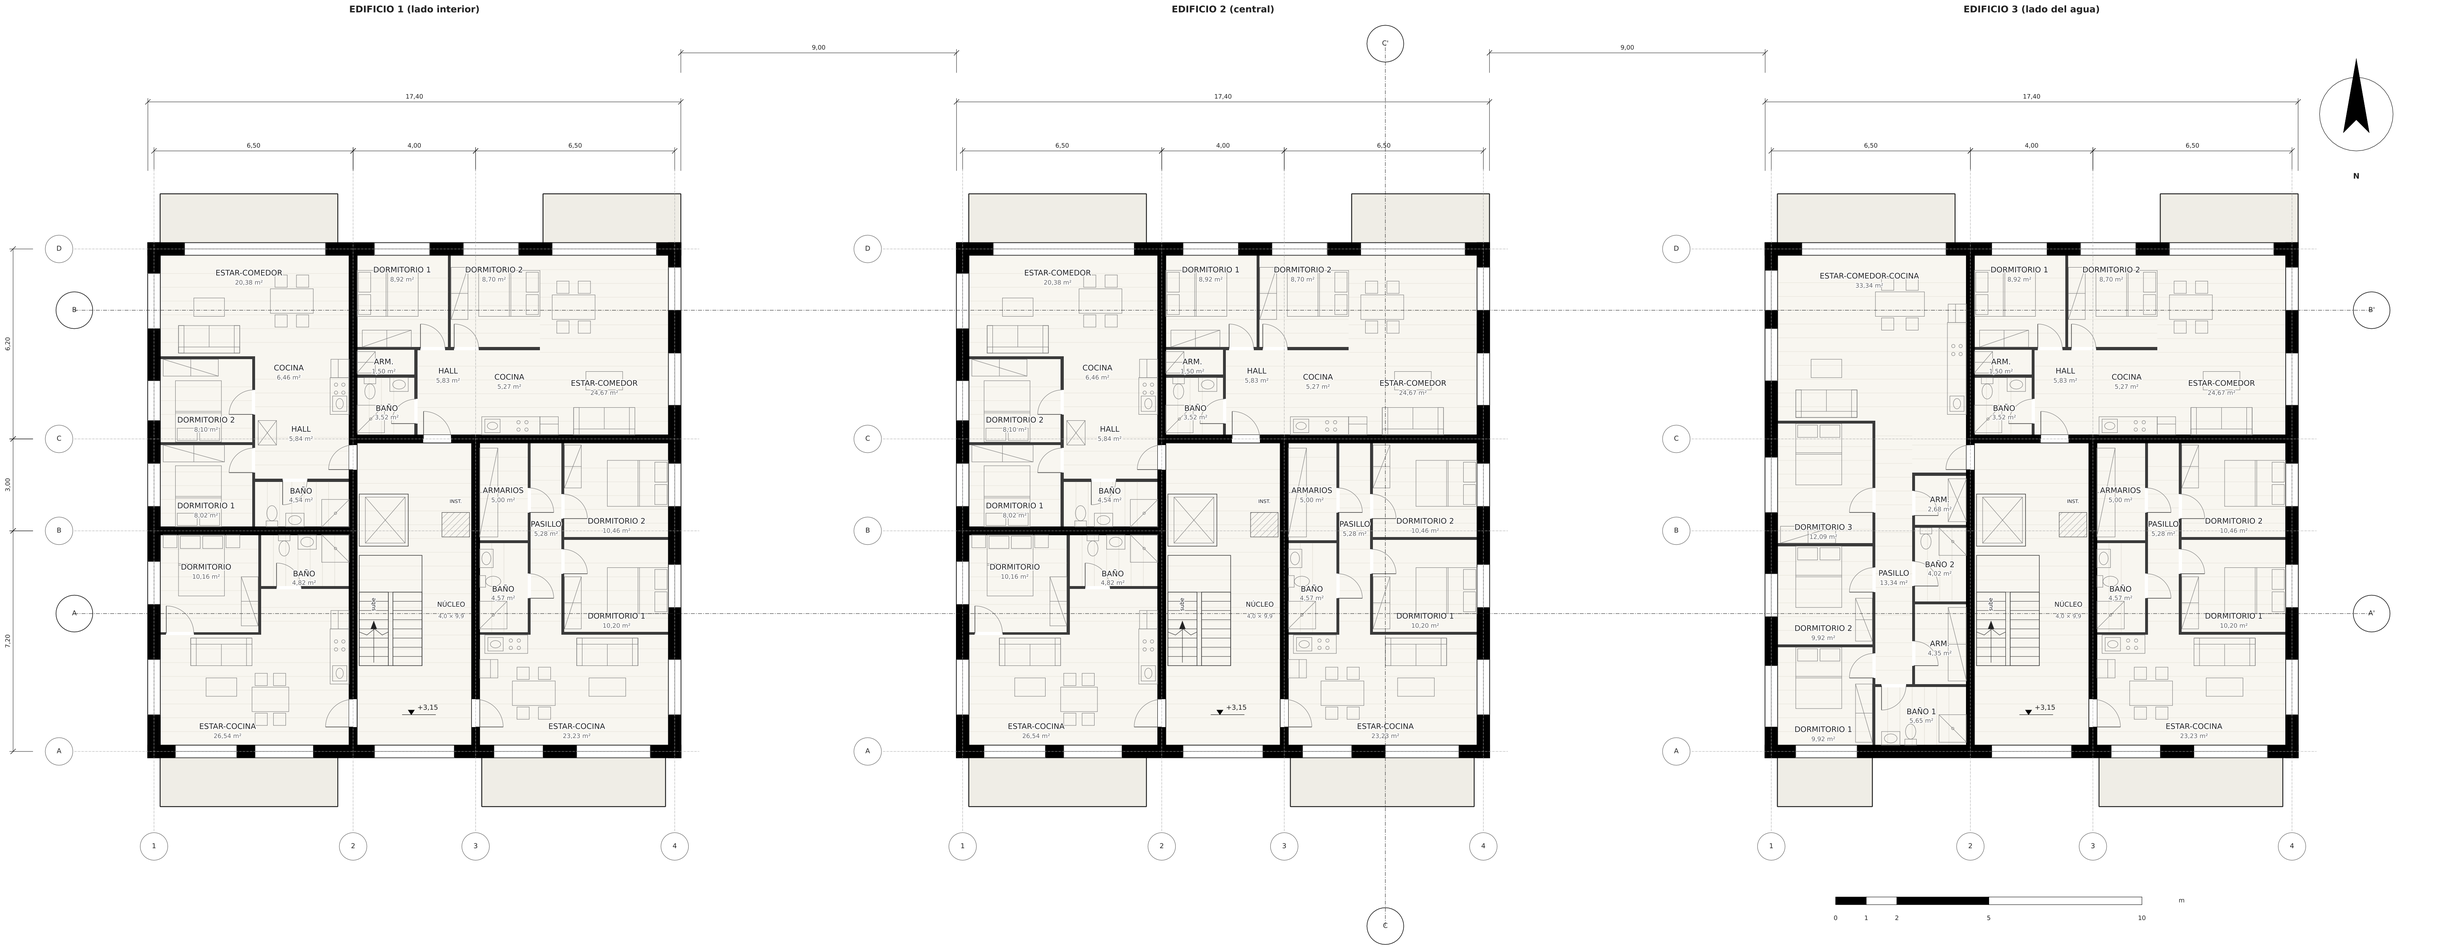


Edificio / planta	Viviendas	Tipos (m² útiles aprox.)	Σ m² útil
INN · baja	2	B 53, C 59	112
INN · 1-3 (c/u)	4	C 59, D 58, A 42, B 53	212
CEN · baja	1	B 53	53
CEN · 1-3 (c/u)	4	C 59, D 58, A 42, B 53	212
AGUA · baja	2	B 53, C 59	112
AGUA · 1-3 (c/u)	3	C 59, D 58, W 95	212

A: 1 dorm. · B, C, D: 2 dorm. · W (edificio agua): 3 dorm. · 38 viviendas en total (programa: 38-42)

Las plantas 1, 2 y 3 son idénticas. Balcones en voladizo (1,60 m) sin apoyo en el terreno. Muros de hormigón en ejes 2, 3 y C; pilares de fachada 0,30 × 0,30.

PLANTA TIPO · NIVELES +3,15 / +6,15 / +9,15

E 1:100

CASO_007 · PROPUESTA B

Escala 1:100

Planta tipo (plantas 1, 2 y 3)

Lámina P02

Anteproyecto · vivienda colectiva · 3 edificios exentos

Anteproyecto