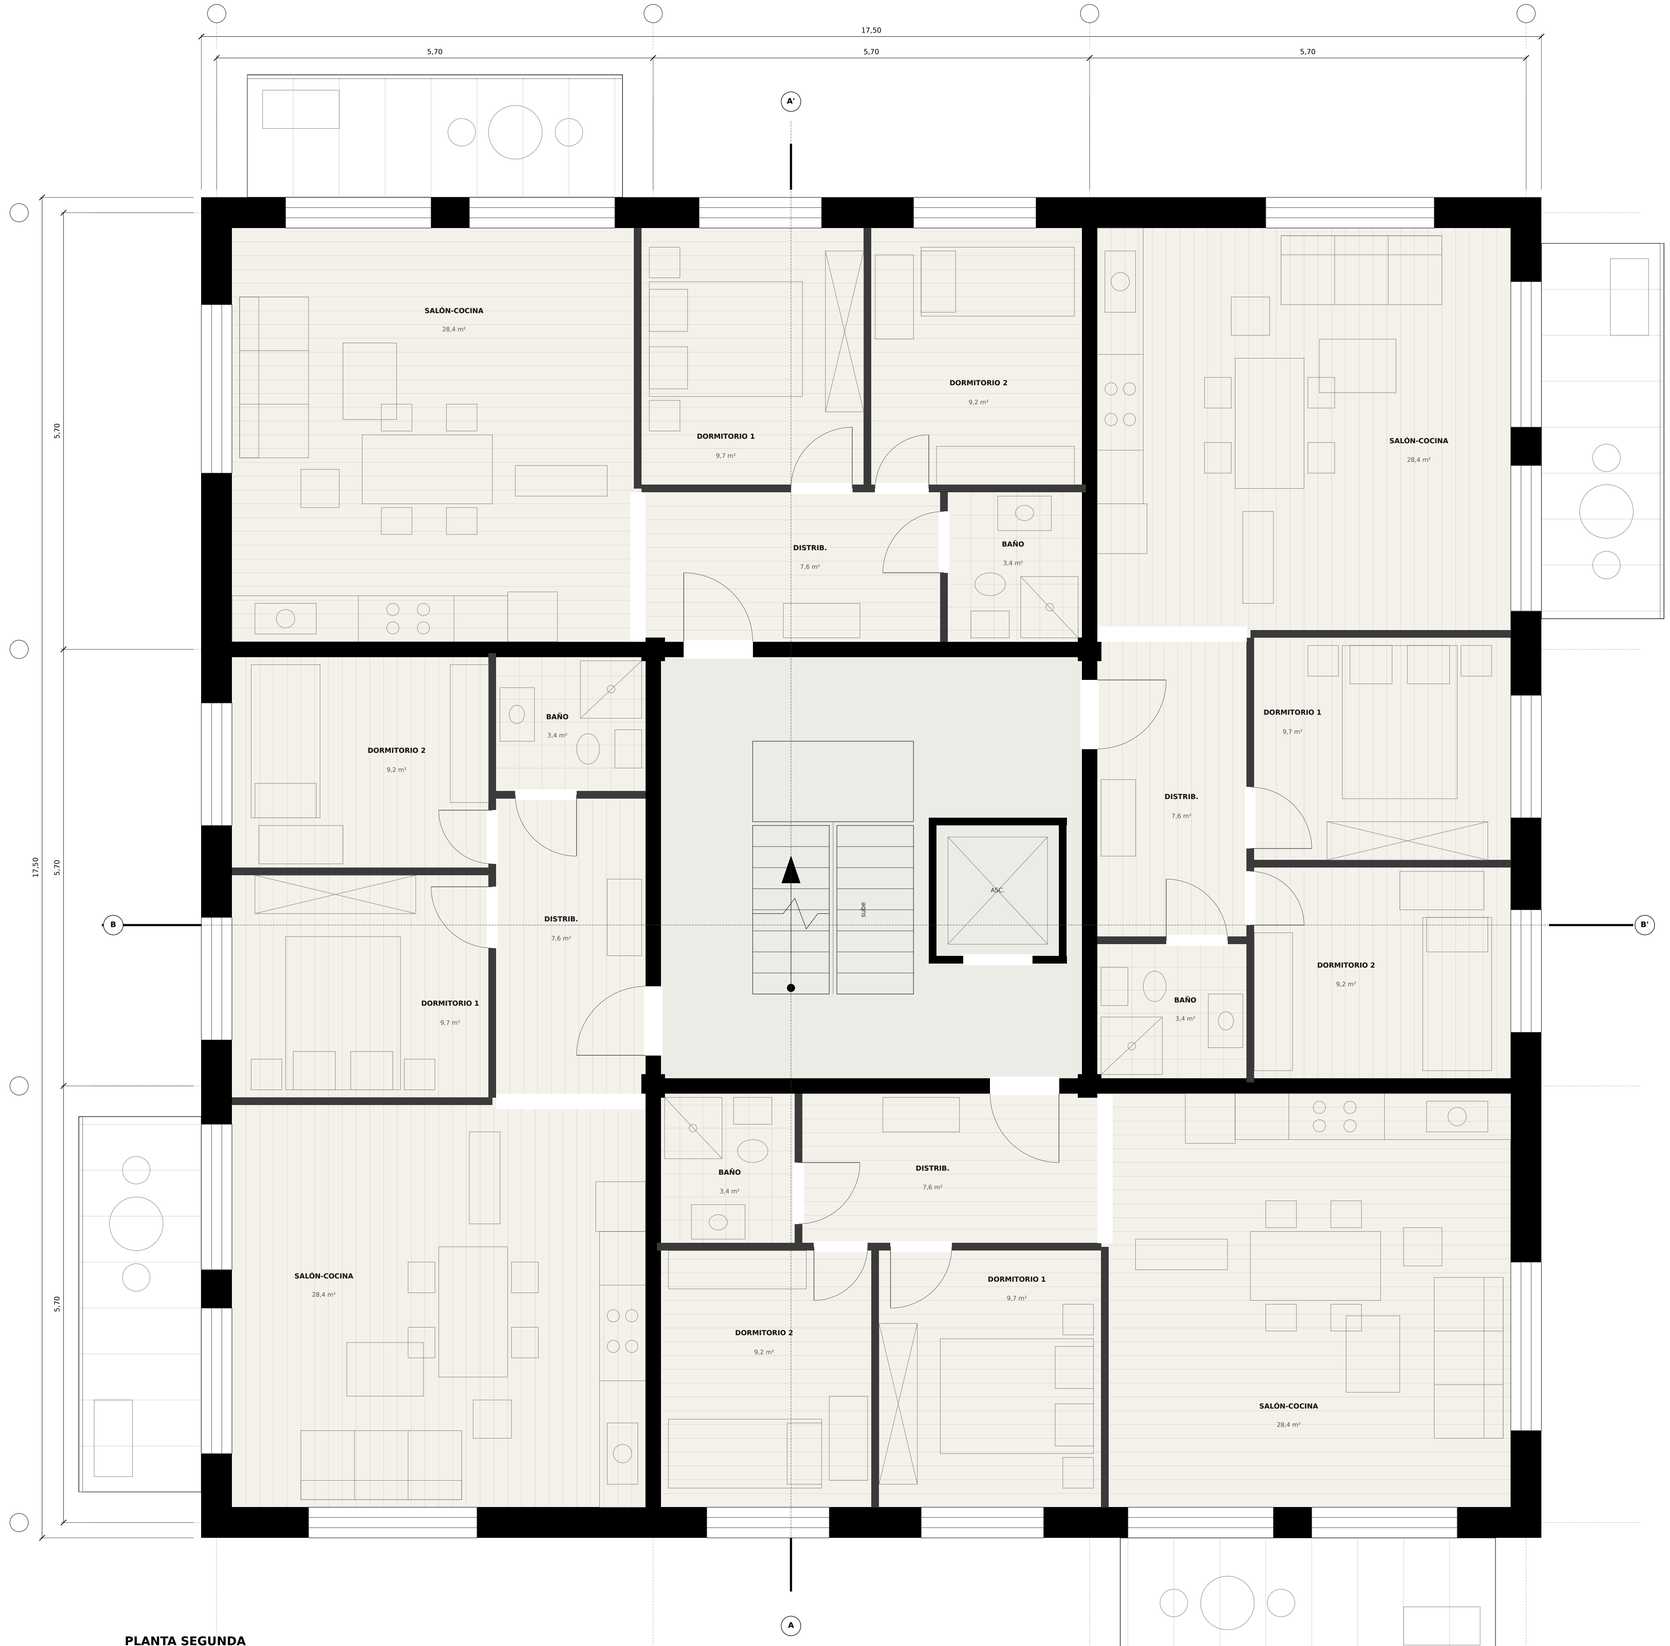


PLANTA SEGUNDA
E 1:40

0 1 2 5 10 m

N

PLANTA SEGUNDA

Cota del forjado: +6,25

Módulo de 17,10 x 17,10 m entre ejes · 17,50 x 17,50 m construidos

VIVIENDA TIPO · 4 POR PLANTA

Estancia	m²
Salón-cocina	28,4
Dormitorio 1	9,7
Dormitorio 2	9,2
Baño	3,4
Distribuidor	7,6
Útil por vivienda	**58,3**
Balcón (no computa)	7,8
Núcleo comunicaciones	30,3

LEYENDA

- Muro de hormigón armado / pilar 0,30 x 0,30
- Tabique cerámico 0,10 (acabado 0,125)
- Balcón volado con rotura de puente térmico
- Ejes estructurales (1-4 / A-D)

Planta idéntica a la primera; cambia la cota y el acabado de petos.

CASO_007 · PROPUESTA C Anteproyecto · vivienda colectiva en propiedad, tres edificios	Dibujo: proyectista C	
Planta segunda	Escala 1:40	**Lámina P03**