
SECCIÓN CONSTRUCTIVA · FACHADA OESTE (voladizo de planta primera)

E 1:25

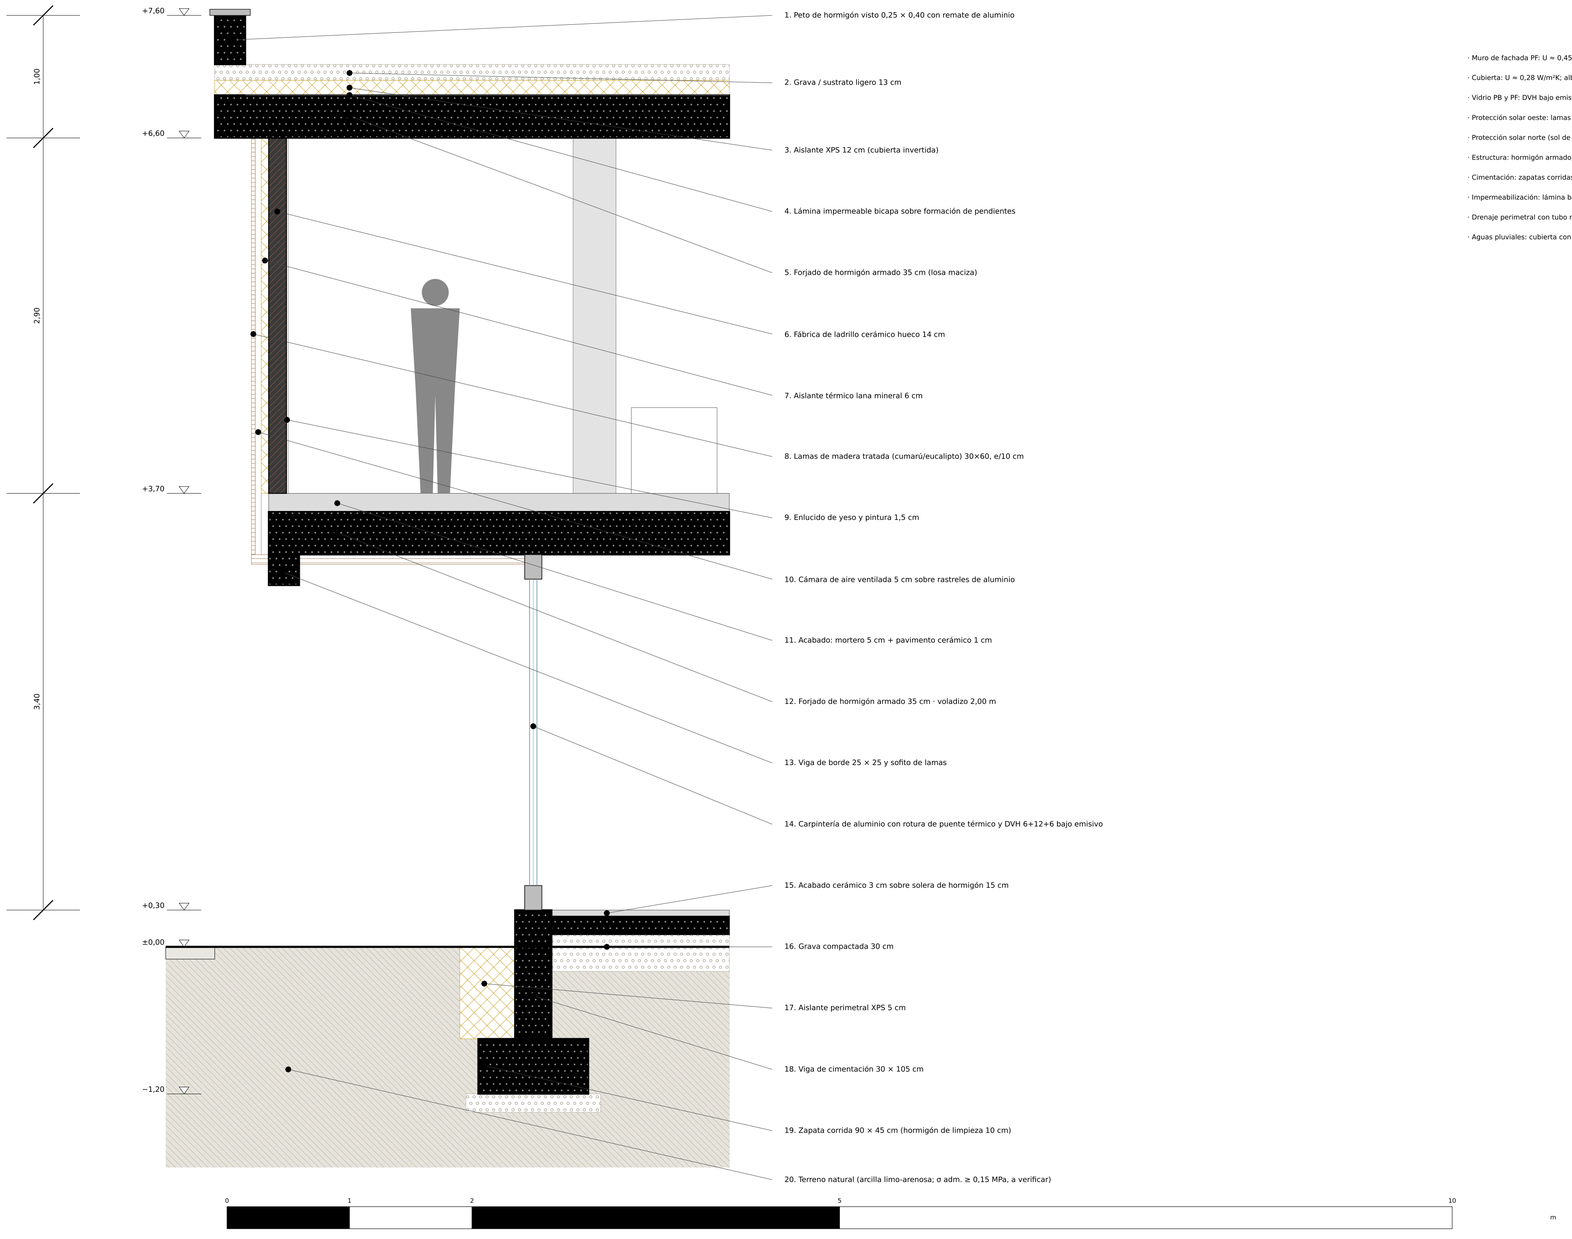

PRESTACIONES DE LA ENVOLVENTE (estimadas)

- Muro de fachada PF: U ≈ 0,45 W/m²K (aislante 6 cm; clima cálido, prima el control solar)
- Cubierta: U ≈ 0,28 W/m²K; albedo alto en zonas sin ajardinar
- Vidrio PB y PF: DVH bajo emisivo, factor solar g ≤ 0,35; U ≈ 1,8 W/m²K
- Protección solar oeste: lamas verticales (autoprotección) y voladizo de 2,00 m
- Protección solar norte (sol de invierno): aleros 0,60 m y vidrios con g ≤ 0,45
- Estructura: hormigón armado; pilares 35×35 cm; losa de 35 cm; vano máx. 6,10 m
- Cimentación: zapatas corridas bajo muros y aisladas 1,40×1,40 m bajo pilares
- Impermeabilización: lámina bajo solera con barrera de vapor (humedad ascendente)
- Drenaje perimetral con tubo ranurado en cota −0,80 y conexión a depósito de riego
- Aguas pluviales: cubierta con 2 % de pendiente y desagües Ø110 con rebosadero

CASO_008 · PROPUESTA A Anteproyecto · Clínica ambulatoria y vivienda	Escala **1:25**	
DETALLE CONSTRUCTIVO · FACHADA OESTE	Lámina **D01**	Anteproyecto