
PLANTA BAJA

E 1:50



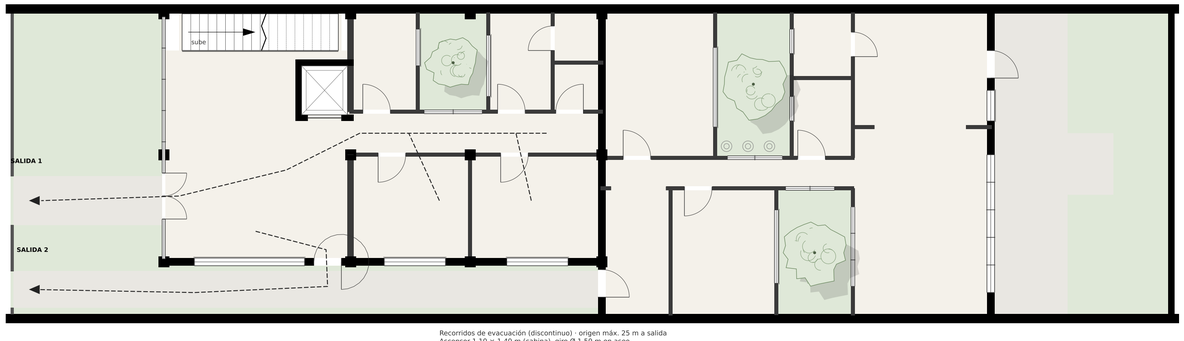

Recorridos de evacuación (discontinuo) · origen máx. 25 m a salida
Ascensor 1,10 × 1,40 m (cabina), giro Ø 1,50 m en aseo
Pasillos ≥ 1,40 m · puertas ≥ 0,90 m

ESQUEMA DE EVACUACIÓN Y ACCESIBILIDAD

E 1:100

CUADRO DE SUPERFICIES ÚTILES (m²)

CLÍNICA · PLANTA BAJA	
Recepción y espera	36,1
Escalera	6,1
Ascensor	2,4
Consultorio 1	12,4
Consultorio 2	13,7
Circulación	10,4
Aseo accesible	6,5
Patio de luz (descubierto)	6,9
Office personal	6,3
Aseo personal	2,2
Vestuario/almacén	2,2
Superficie útil	**98,3**

VIVIENDA CONSERVADA	
Recibidor	8,3
Dormitorio 1	13,6
Patio P2 (descubierto)	9,7
Pasillo	7,2
Dormitorio 2	16,3
Patio P1 (descubierto)	11,2
Baño	4,7
Lavadero	3,9
Estar-comedor	26,0
Cocina	15,7
Superficie útil	**95,7**

RESUMEN	
Clínica útil PB	98,3
Clínica útil P1	114,8
Clínica útil total	**213,1**
Vivienda útil	95,7
Clínica construida (≈)	258,0
Vivienda construida (≈)	125,0
Total construido (≈)	383,0

Programa: 260–440 m² (clínica+reforma)

N

CASO_008 · PROPUESTA A
Anteproyecto · Clínica ambulatoria y vivienda

Escala **1:50**

PLANTA BAJA · CLÍNICA Y VIVIENDA

Lámina **P01**

Anteproyecto