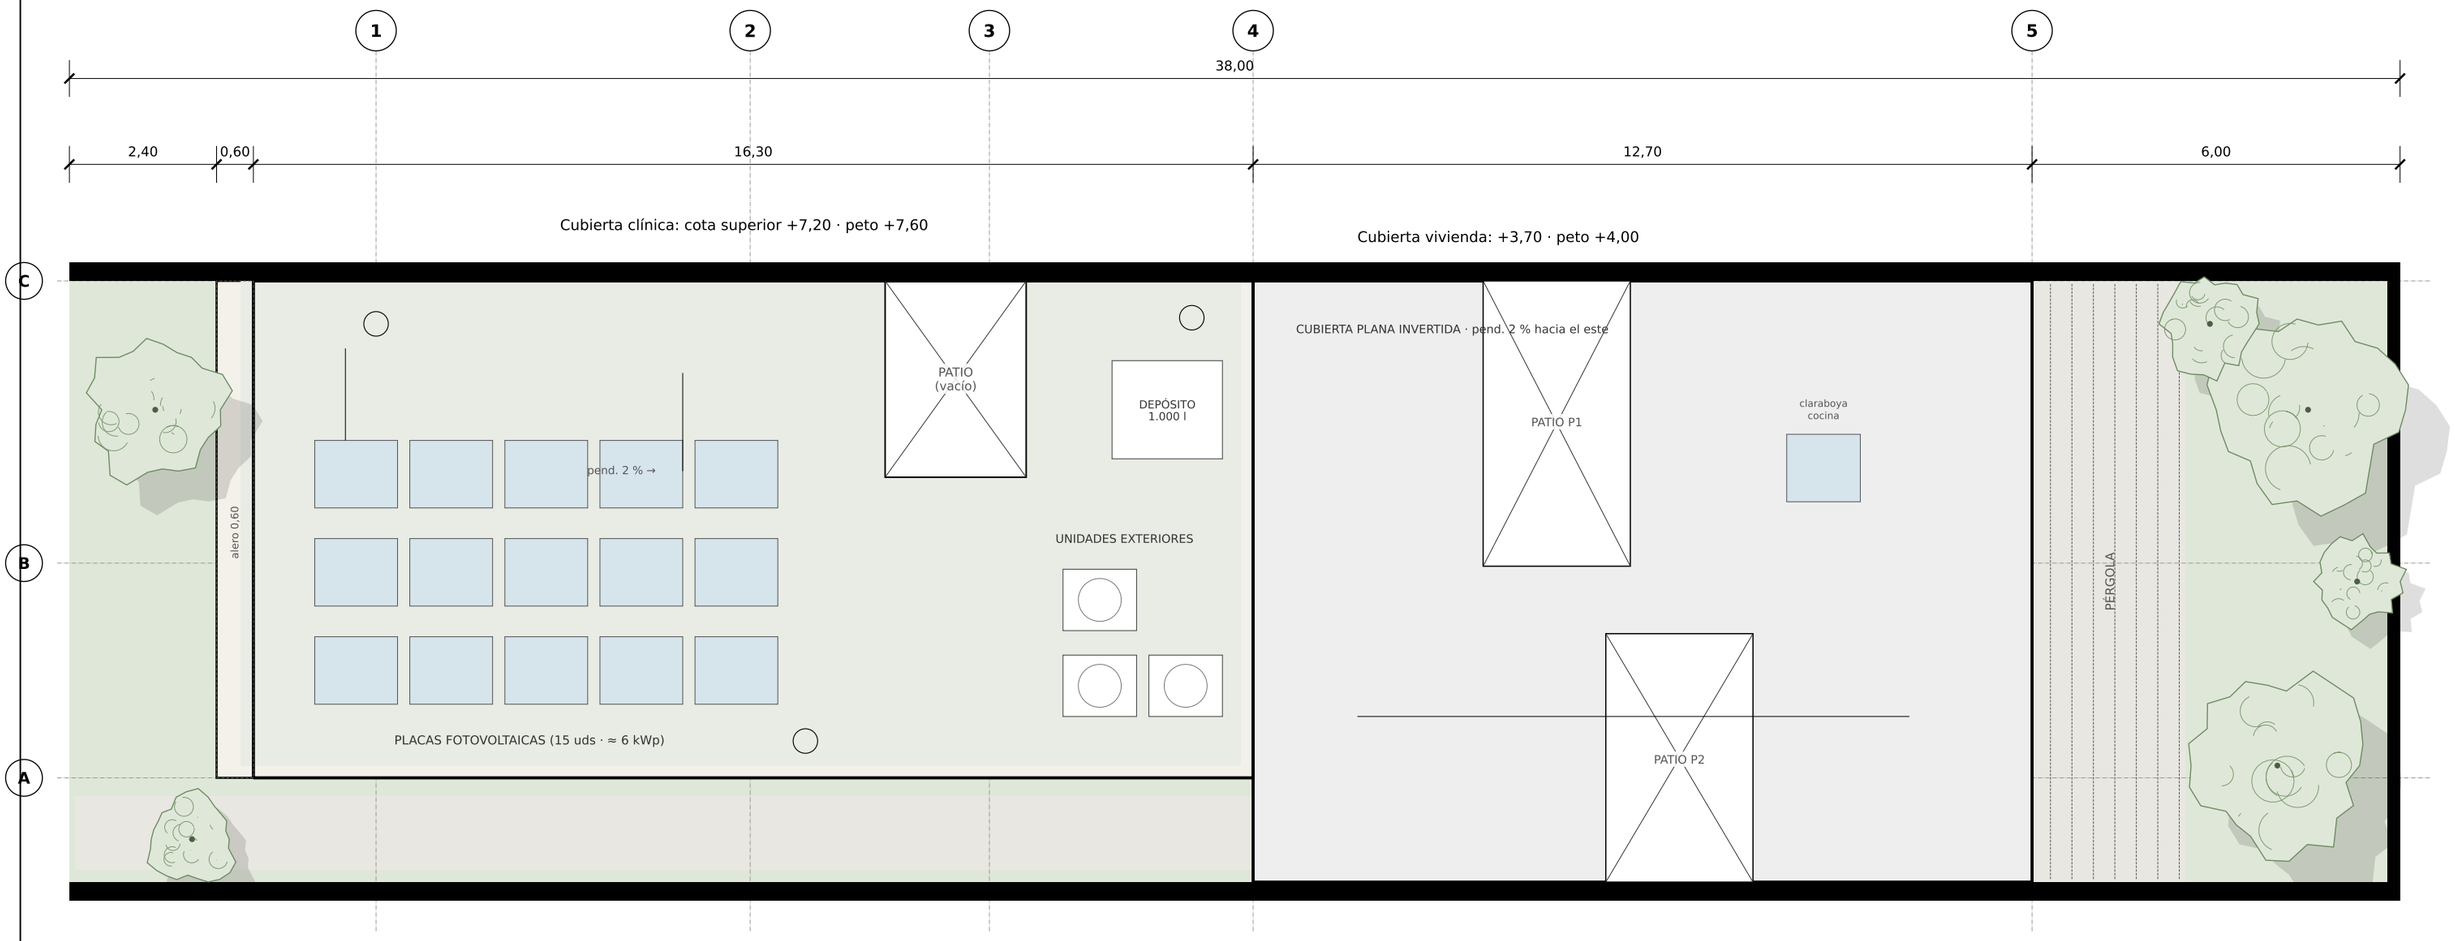


PLANTA DE CUBIERTAS

N

0 1 2 5 10 m

E 1:100

LEYENDA

· Cubierta plana invertida ajardinada (sedum, 8 cm) sobre aislante XPS 10 cm y lámina impermeable

· Peto de hormigón visto h = 0,40 m con remate de aluminio; desagües Ø110 con rebosadero

· Placas fotovoltaicas inclinadas 20° (orientación norte, hemisferio sur) en soportes de acero galvanizado

· Pendiente 2 % hacia desagües; recogida de pluviales a depósito de 5 m³ para riego

CASO_008 · PROPUESTA A Anteproyecto · Clínica ambulatoria y vivienda	Escala **1:100**	
PLANTA DE CUBIERTAS	Lámina **P03**	Anteproyecto