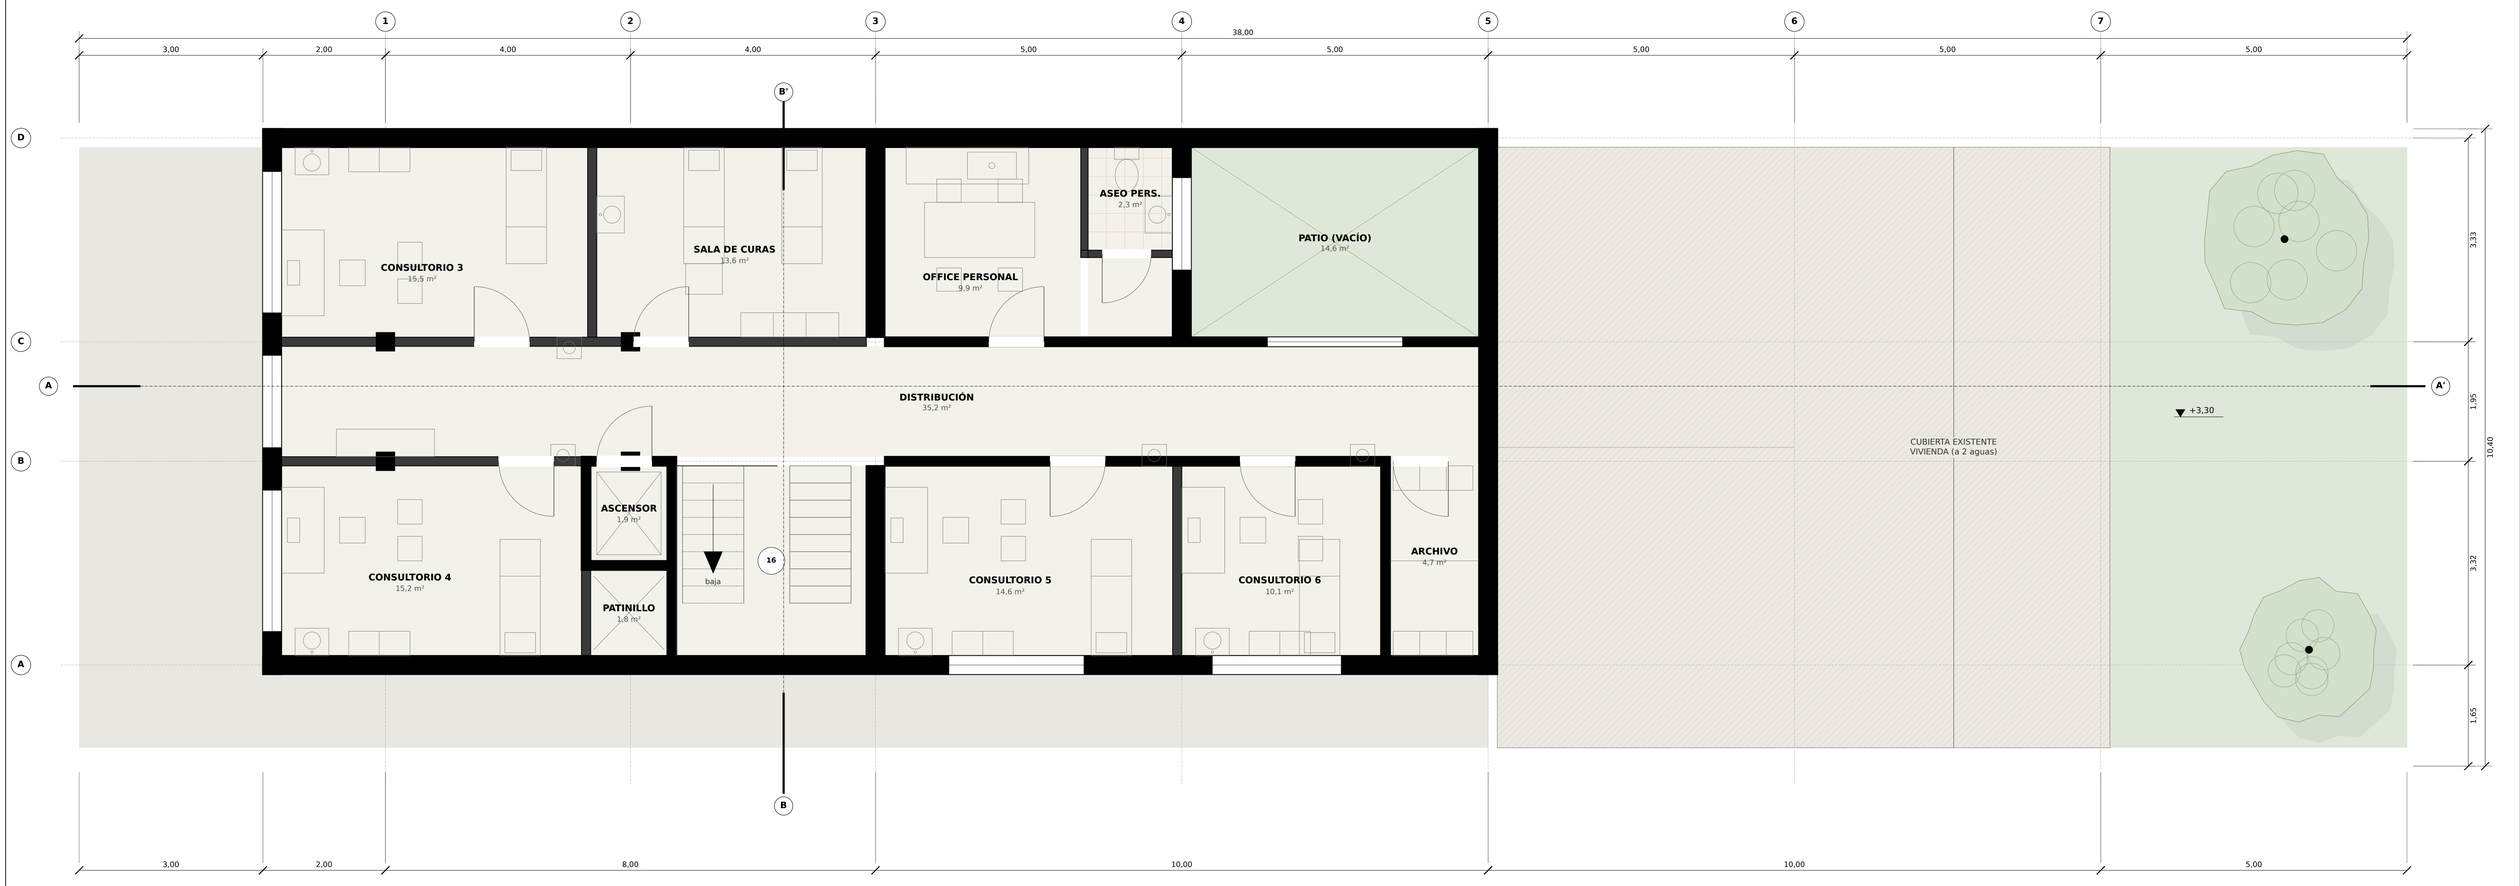

PLANTA PRIMERA

E 1:50

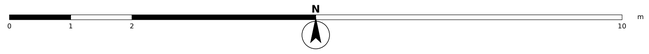

SUPERFICIES ÚTILES — CLÍNICA

13	Consultorio 3	15,5 m²	**20**	Consultorio 5	14,6 m²
14	Consultorio 4	15,2 m²	**21**	Consultorio 6	10,1 m²
15	Sala De Curas	13,6 m²	**22**	Archivo	4,7 m²
16	Escalera (Vacío)	9,6 m²	**23**	Office Personal	9,9 m²
17	Patinillo	1,8 m²	**24**	Aseo Pers.	2,3 m²
18	Ascensor	1,9 m²	**25**	Patio (Vacío)	14,6 m²
19	Distribución	35,2 m²			

LEYENDA

- Muro portante / existente (poché negro)
- Tabique
- Ventana
- Puerta abatible
- Mobiliario
- Eje estructural
- Elemento por encima del corte

ESQUEMA DE ACCESIBILIDAD Y EVACUACIÓN E 1:100

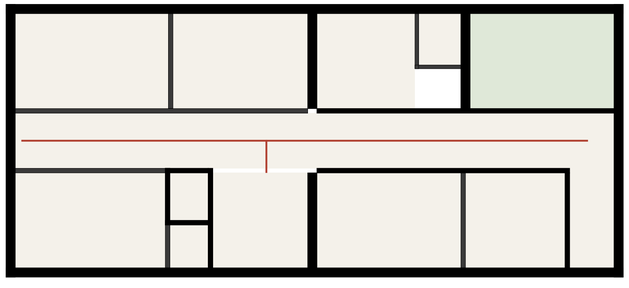

Verde: recorrido accesible (rampa 6 %, aseo 1 adaptado, ascensor)

Rojo: recorrido de evacuación (< 25 m a salida a vía pública)

CASO_008 · PROPUESTA B	**PLANTA PRIMERA**
Anteproyecto · Clínica ambulatoria y vivienda	Escala 1:50 · Lámina P02