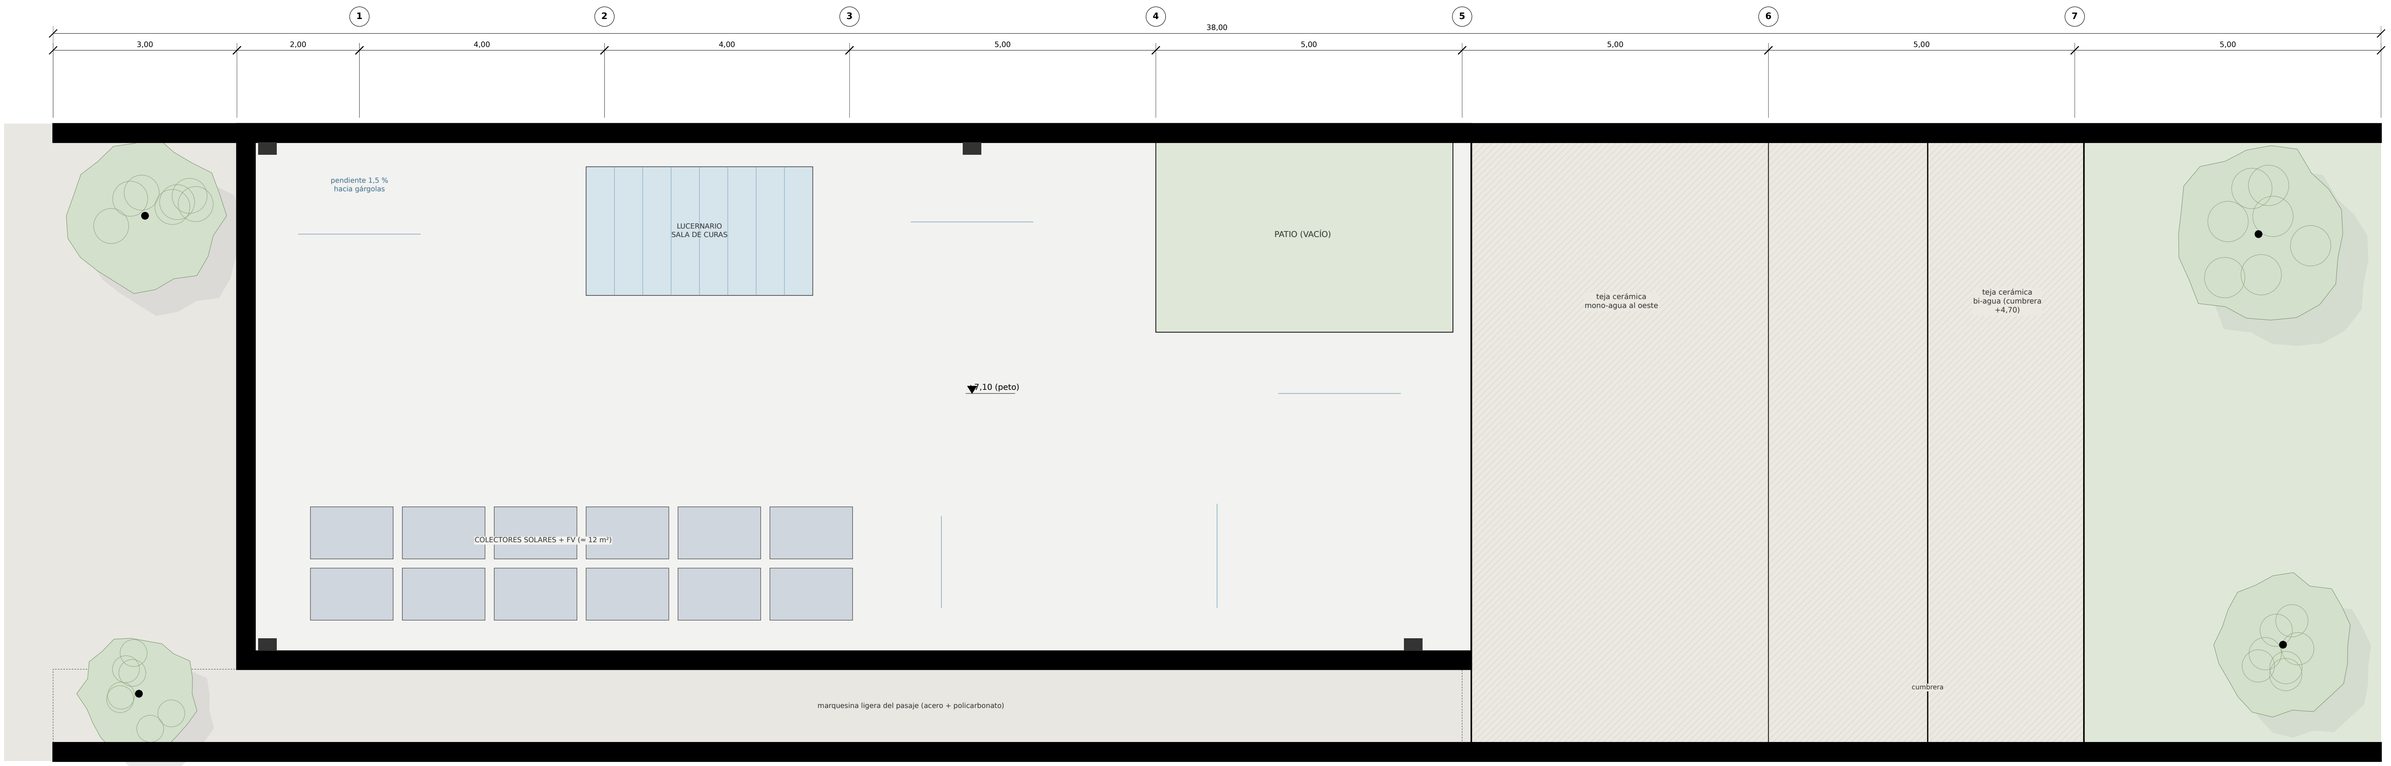

PLANTA DE CUBIERTAS

E 1:50

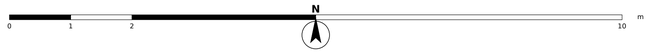

CUBIERTA PLANA INVERTIDA (caja nueva)

1 Grava lavada 50 mm (protección y lastre)
2 Geotextil + aislante XPS 80 mm (cubierta invertida)
3 Impermeabilización: lámina bituminosa doble (SBS) con solape en peto
4 Formación de pendientes 1,5 % (hormigón celular)
5 Forjado nervado de hormigón armado h = 25 cm
6 Falso techo registrable (pladur) con instalaciones
Remate: peto h = 50 cm con albardilla de aluminio y goterón.

CUBIERTA EXISTENTE (vivienda conservada)

Se conserva la estructura de cubierta inclinada y se repasa la teja.
Se añade aislante bajo teja (lana mineral 80 mm) y sub-cubierta ventilada.
Canalón y bajante nuevos hacia el patio trasero (infiltración).
Cota de cumbrera del tramo alto: +4,70.

AGUAS Y ENERGÍA

Pluviales: gárgolas y 4 bajantes a depósito de retención (4 m³) para riego y descarga de inodoros; rebose a infiltración.
Colectores solares térmicos para ACS y paneles FV.
Flechas azules: sentido de la pendiente.

CASO_008 · PROPUESTA B	**PLANTA DE CUBIERTAS**
Anteproyecto · Clínica ambulatoria y vivienda	Escala 1:50 · Lámina P03