
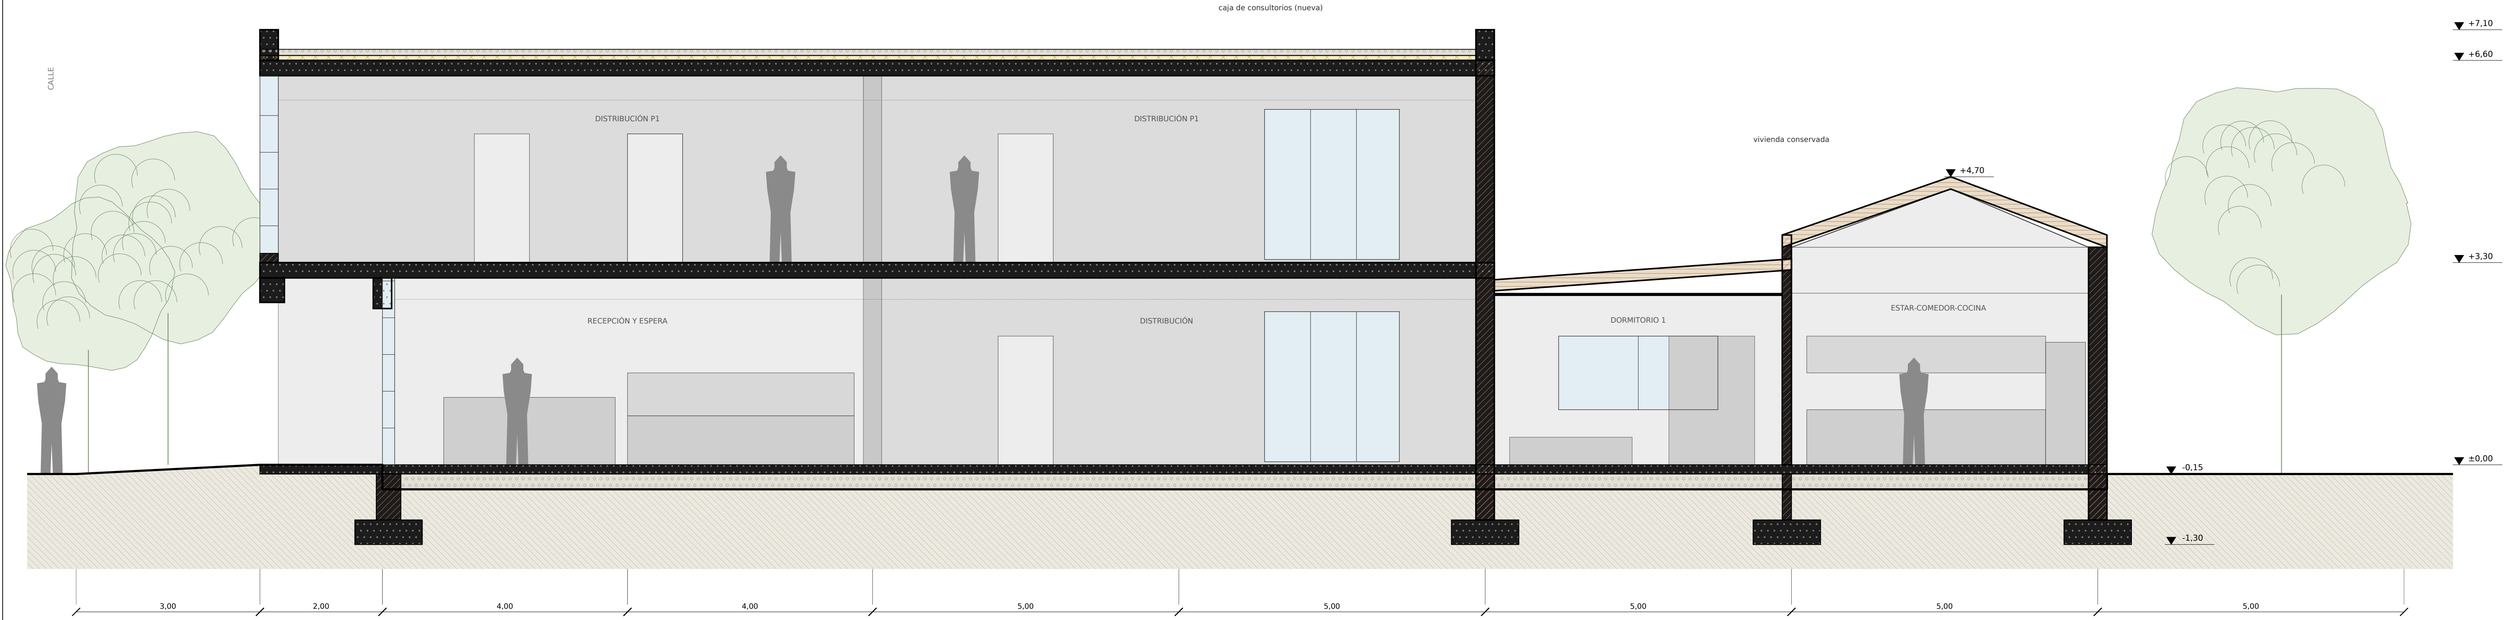


SECCIÓN LONGITUDINAL A-A'

E 1:50

0 1 2 5 10 m

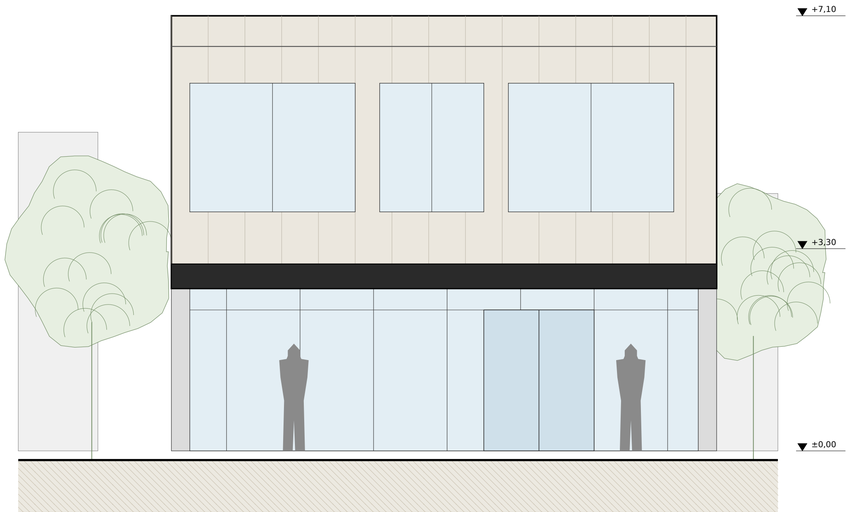


ALZADO OESTE

E 1:50

MATERIALES Y NOTAS

Forjados de hormigón armado y muros: poché con trama de hormigón.
Muros existentes de ladrillo cerámico: trama de fábrica (se conservan y consolidan).
Nuevo: pórtico de hormigón armado en ejes 1-3 y forjado nervado h = 25 cm.
Voladizo de 2,00 m con viga de borde 40 × 40 cm; cimentación por zapatas
corridas bajo muros y zapatas aisladas 1,40 × 1,40 m bajo pilares.
Muro cortina de aluminio con vidrio DVH bajo emisivo en planta baja retranqueada.
Fachada de la caja: panel ventilado de fibrocemento claro con lamas verticales cada 60 cm
y cinta de ventanas con protección solar (voladizo + lamas).
Cubierta plana invertida (aislante XPS, grava). Vivienda: cubierta de teja existente.

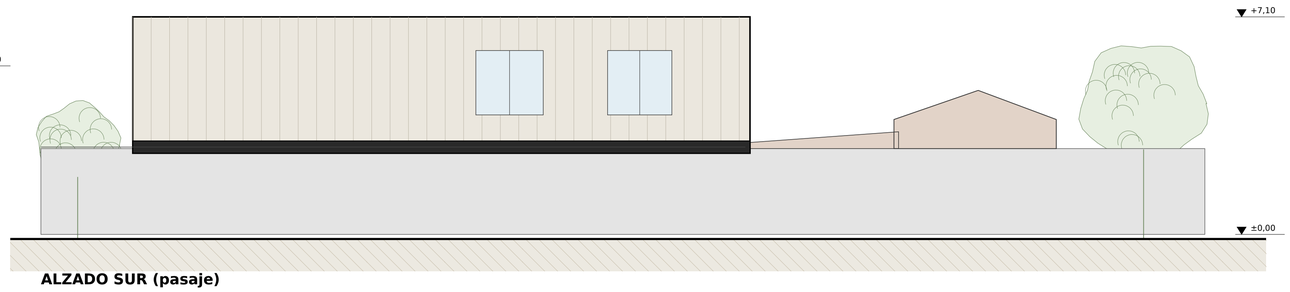

ALZADO SUR (pasaje)

E 1:100

CASO_008 · PROPUESTA B	SECCIÓN LONG. Y ALZADOS
Anteproyecto · Clínica ambulatoria y vivienda	Escala 1:50 · Lámina S01