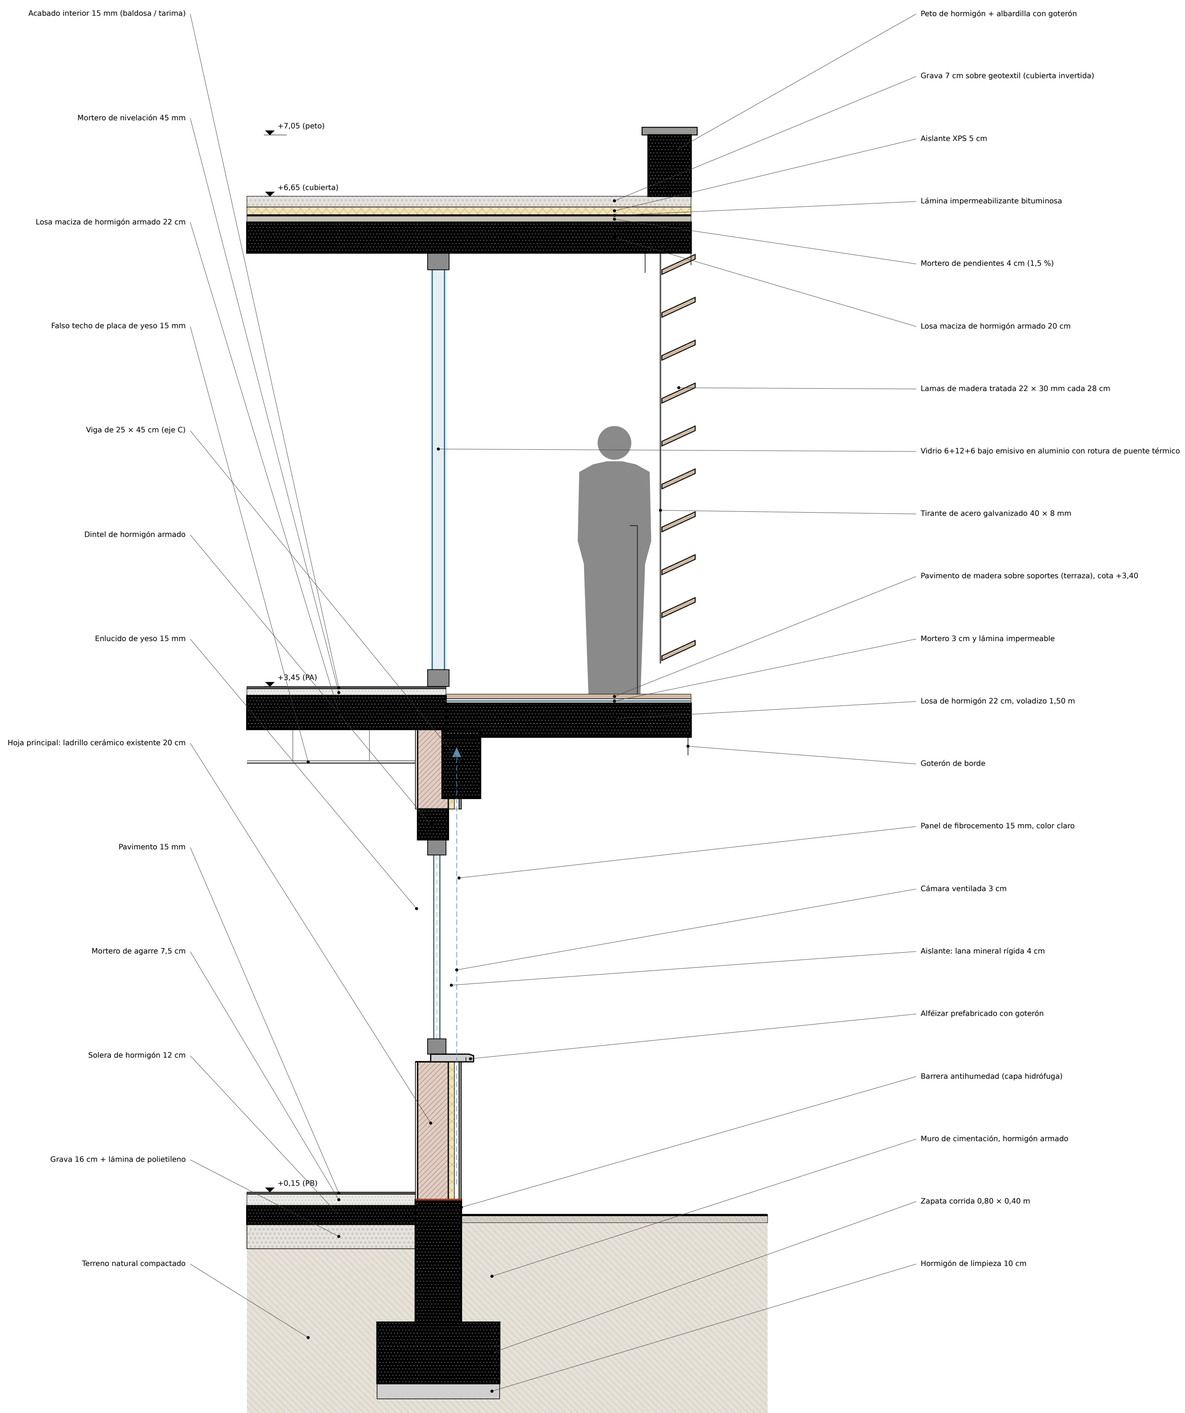


DETALLE: FACHADA NORTE · CIMENTACIÓN A CUBIERTA

E 1:20

0 0,5 1 1,5 2 m

CASO_008 · PROPUESTA C Sección constructiva de fachada norte Anteproyecto	Escala **E 1:20** Lámina **D01**