




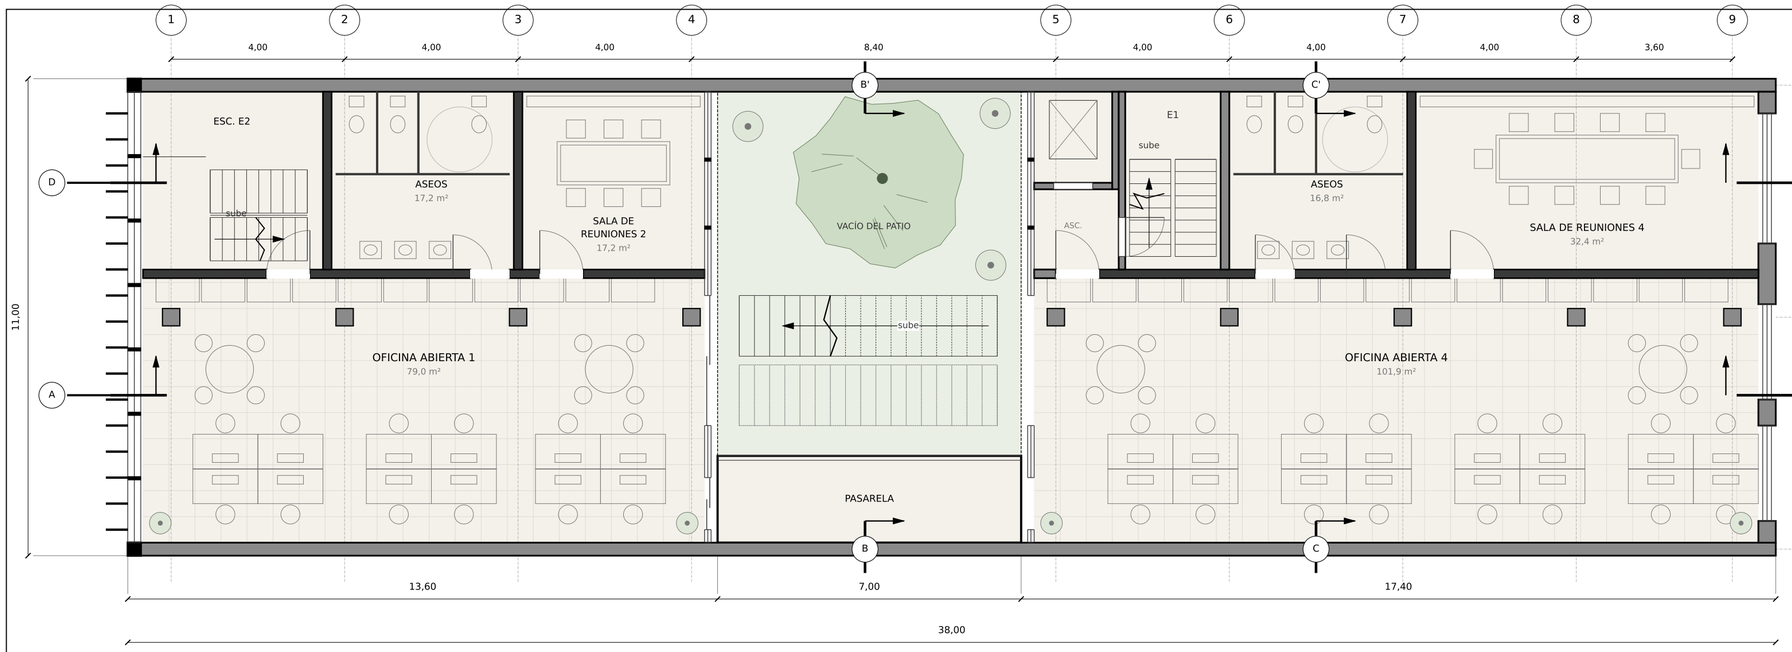

PLANTA PRIMERA +3,60


E 1:100

Fachada a la calle al norte (izquierda).

LEYENDA


- Muro existente que se conserva
- Obra nueva (muro / fachada / forjado)
- Tabique nuevo
- Existente a demoler (contorno)
- Carpintería / muro cortina

Nivel de corte de planta: +1,20 m sobre el suelo terminado.

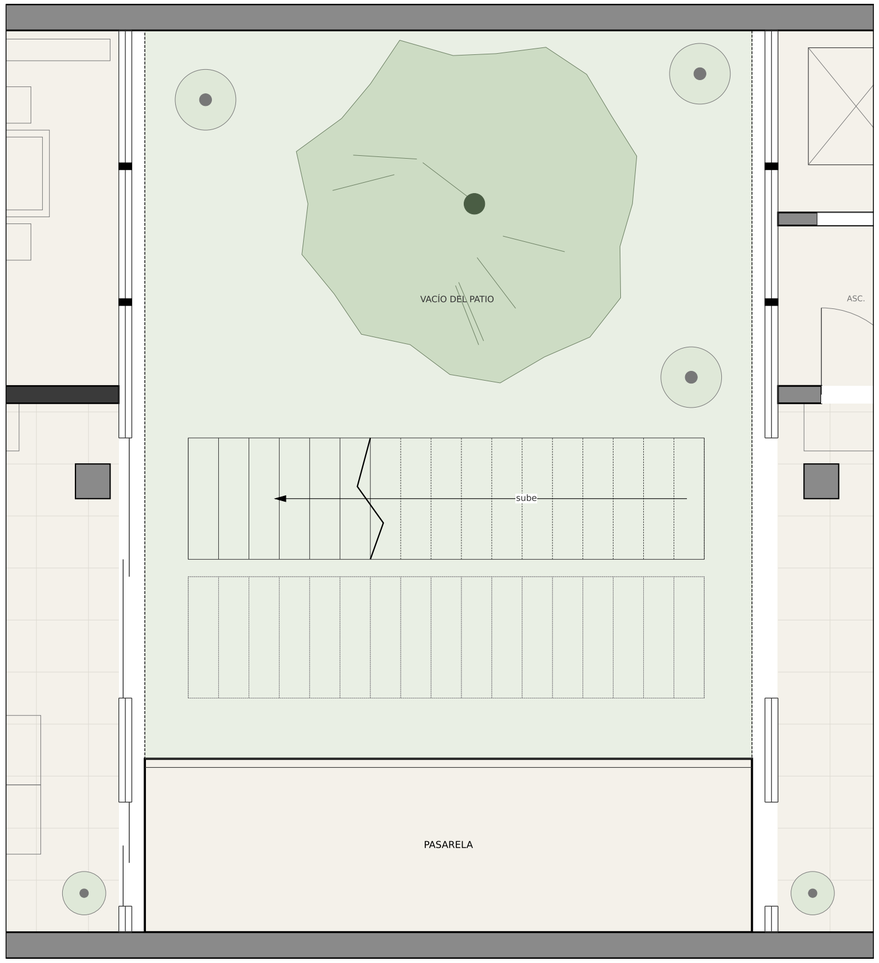

AMPLIACIÓN PATIO, PASARELA Y ESCALERA

E 1:50

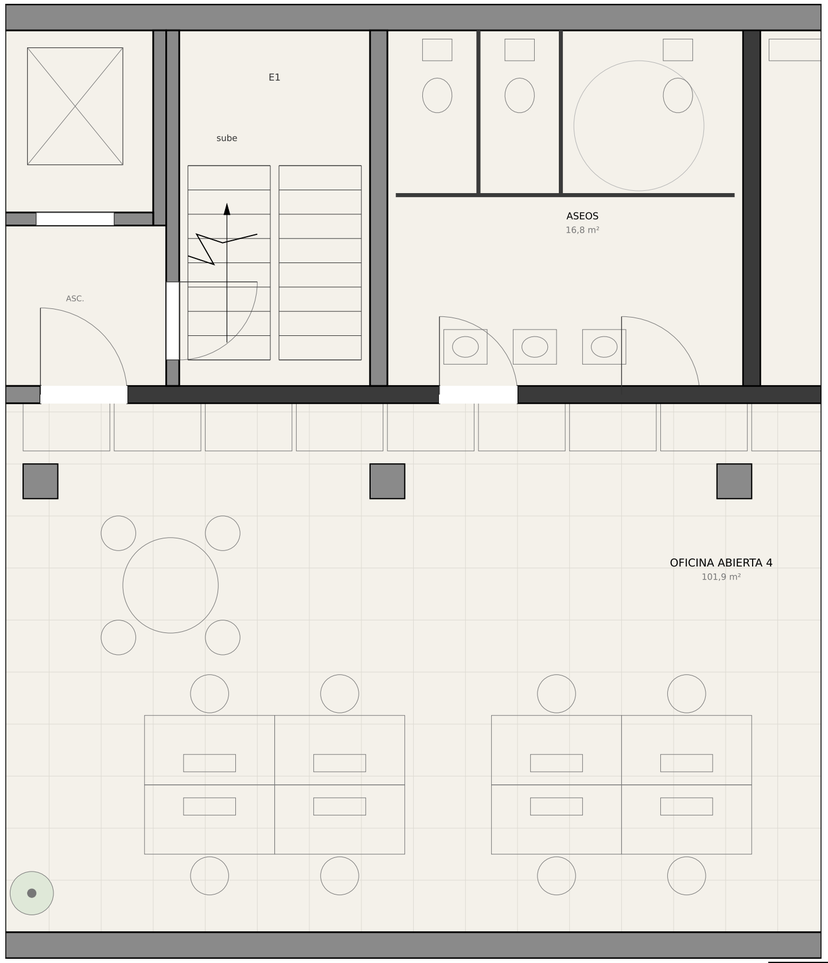

AMPLIACIÓN NÚCLEO Y ASEOS

E 1:50

CUADRO DE SUPERFICIES ÚTILES (aprox.)

ASEOS 1	17,2 m²
OFICINA ABIERTA 1	79,0 m²
SALA DE REUNIONES 2	17,2 m²
NÚCLEO E1 + ASCENSOR	17,6 m²
ASEOS 2	16,8 m²
OFICINA ABIERTA 4	101,9 m²
SALA DE REUNIONES 4	32,4 m²
PASARELA	14,0 m²
Superficie útil interior del nivel	**296,1 m²**

CASO_009 · PROPUESTA A

Planta primera

Anteproyecto · Renovación integral de edificio de oficinas

Lámina

P02

Escala

1:100

Anteproyecto