

PLANTA TERCERA Y TERRAZA +10,80


E 1:100

Fachada a la calle al norte (izquierda).

LEYENDA


- Muro existente que se conserva
- Obra nueva (muro / fachada / forjado)
- Tabique nuevo
- Existente a demoler (contorno)
- Carpintería / muro cortina

Nivel de corte de planta: +1,20 m sobre el suelo terminado.

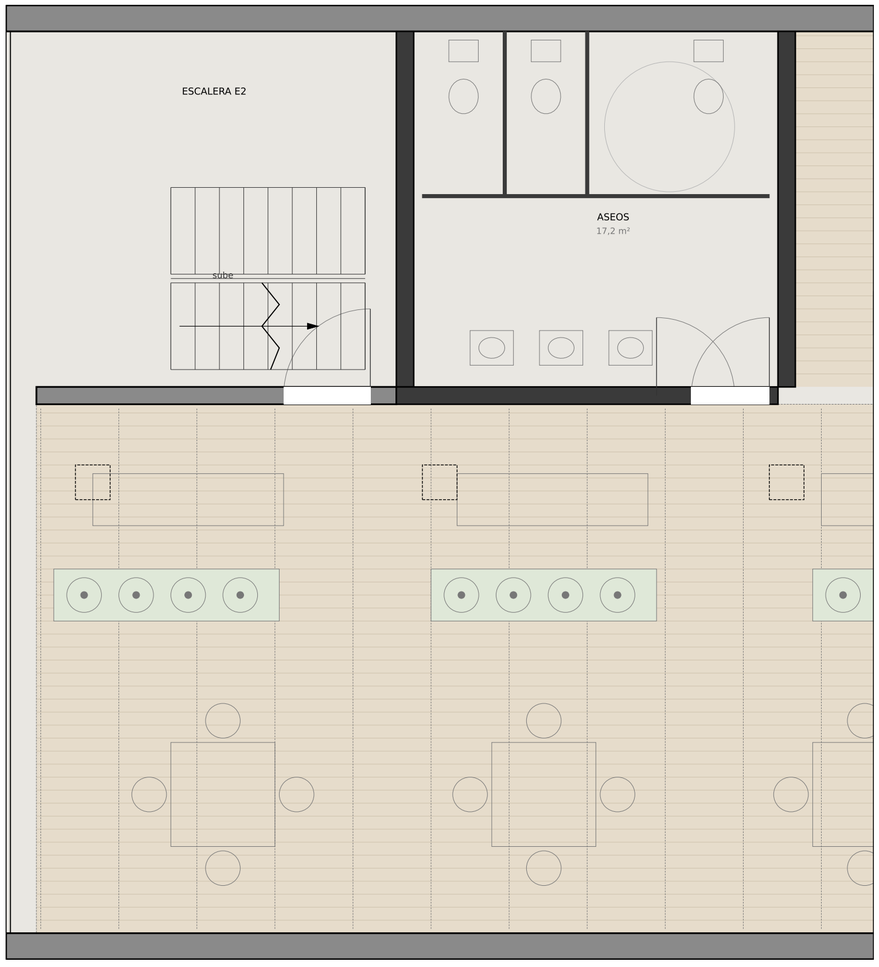

AMPLIACIÓN TERRAZA

E 1:50

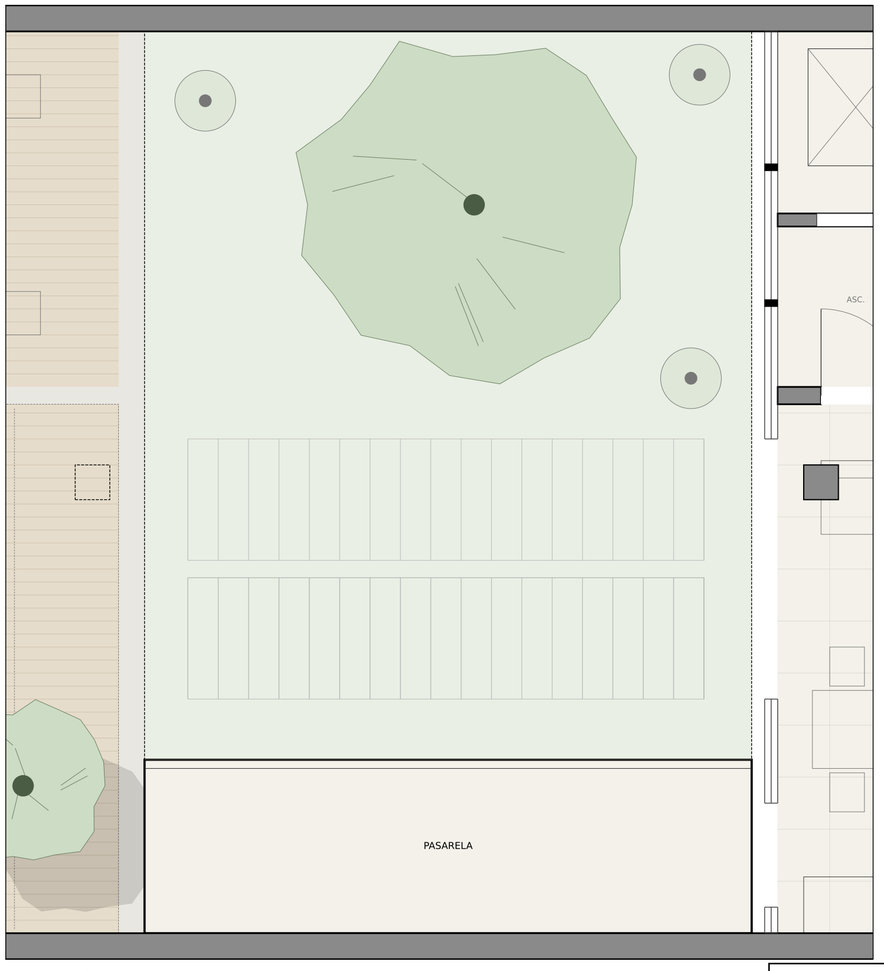

AMPLIACIÓN PATIO, PASARELA Y ESCALERA

E 1:50

CUADRO DE SUPERFICIES ÚTILES (aprox.)

ASEOS 1	17,2 m²
NÚCLEO E1 + ASCENSOR	17,6 m²
ASEOS 2	16,8 m²
ZONA DE DESCANSO Y COMEDOR	52,5 m²
OFICINA ABIERTA 6	48,2 m²
SALA DE REUNIONES 6	32,4 m²
PASARELA	14,0 m²
TERRAZA EXTERIOR (exterior)	96,2 m²
Superficie útil interior del nivel	**198,7 m²**

CASO_009 · PROPUESTA A

Planta tercera y terraza

Anteproyecto · Renovación integral de edificio de oficinas

Lámina

P04

Escala

1:100

Anteproyecto