
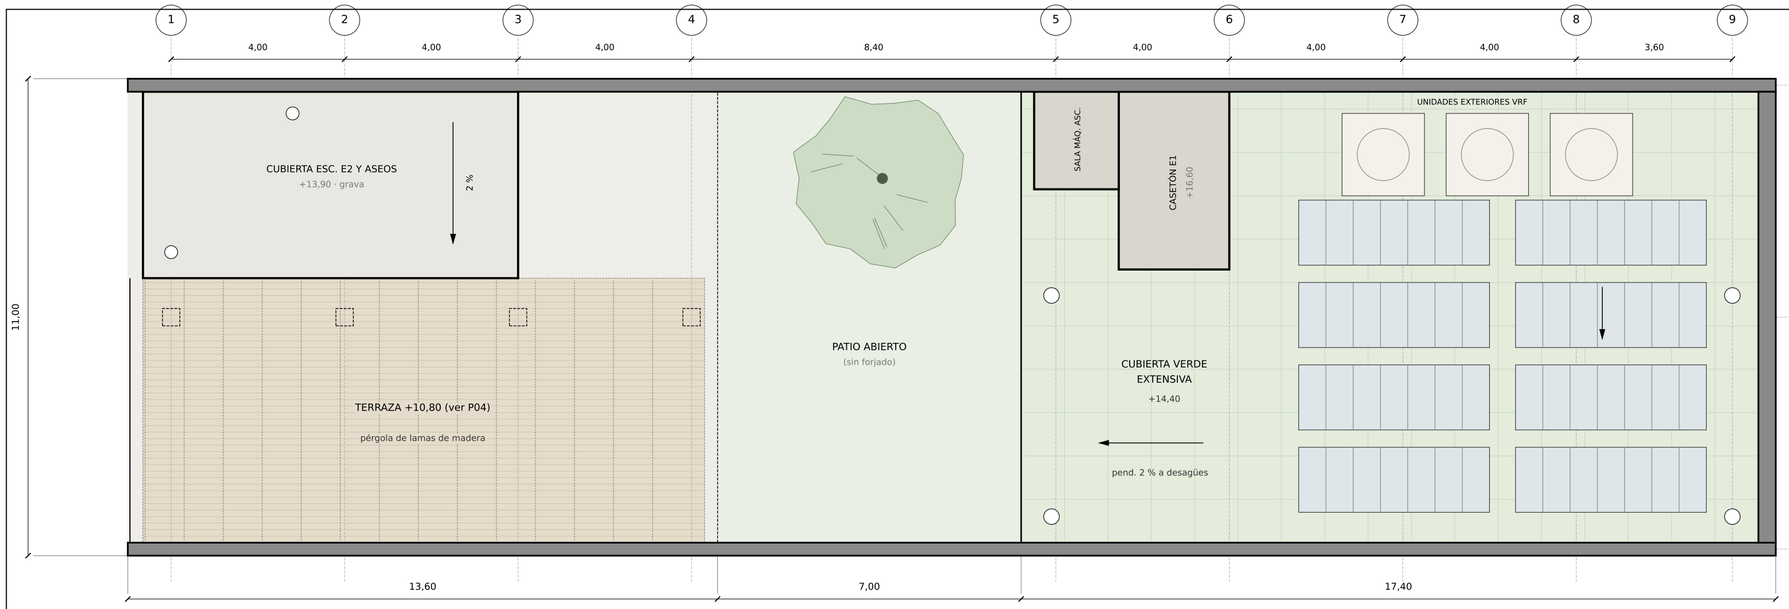


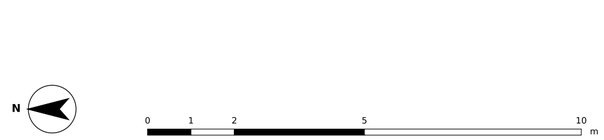

PLANTA DE CUBIERTAS +14,40

E 1:100

Fachada a la calle al norte (izquierda).

LEYENDA

- Muro existente que se conserva
- Obra nueva (muro / fachada / forjado)
- Tabique nuevo
- Existente a demoler (contorno)
- Carpintería / muro cortina

Nivel de corte de planta: +1,20 m sobre el suelo terminado.

CUADRO DE CUBIERTAS (aprox.)

Cubierta verde extensiva del cuerpo posterior (+14,40)	191,4 m²
Paneles fotovoltaicos (32 uds)	≈ 60 m²
Cubierta del bloque E2 + aseos (+13,90)	36,6 m²
Terraza de descanso con pérgola (+10,80)	96,2 m²
Patio abierto (sin forjado)	72,8 m²

AMPLIACIÓN TERRAZA Y CUBIERTA E2
E 1:50

AMPLIACIÓN CASETONES Y CUBIERTA VERDE
E 1:50

CASO_009 · PROPUESTA A

Planta de cubiertas

Anteproyecto · Renovación integral de edificio de oficinas

Lámina
P05

Escala
1:100

Anteproyecto