

SECCIÓN LONGITUDINAL A–A'

E 1:100 por patio y escaleras (y = 3,70)

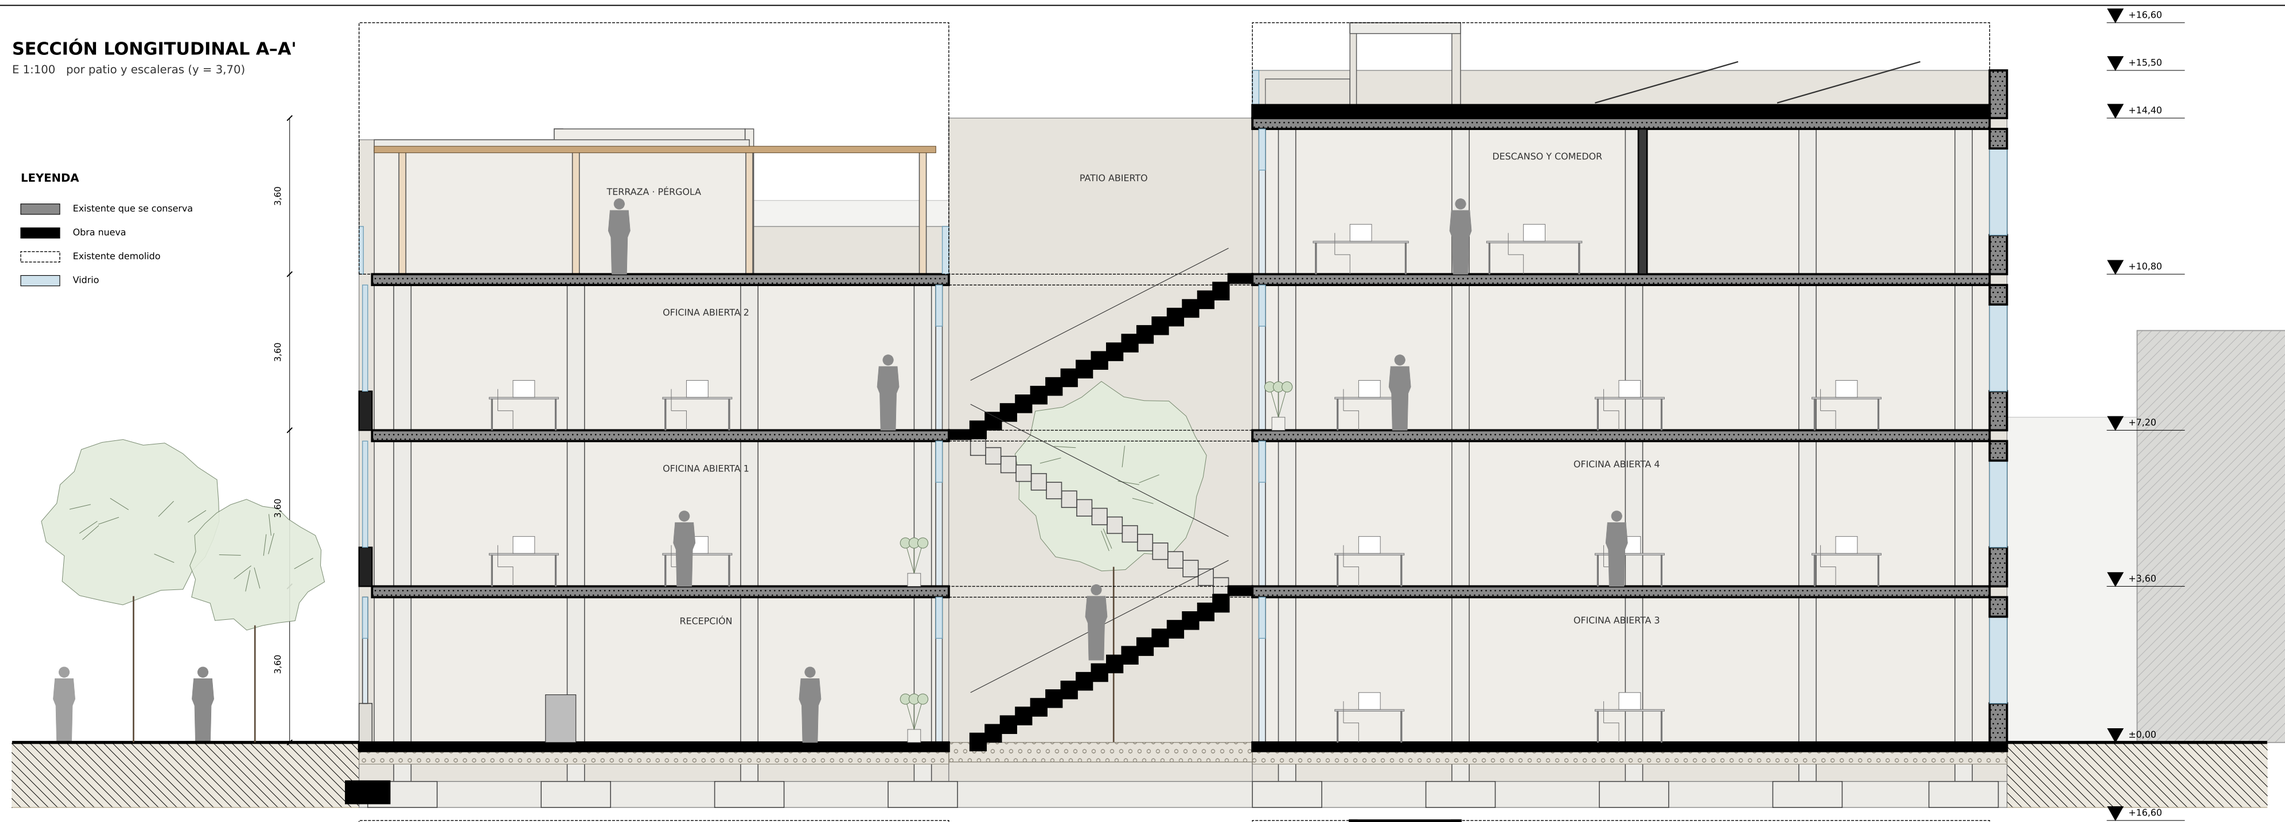

SECCIÓN LONGITUDINAL D–D'

E 1:100 por núcleo, aseos y salas (y = 9,00)

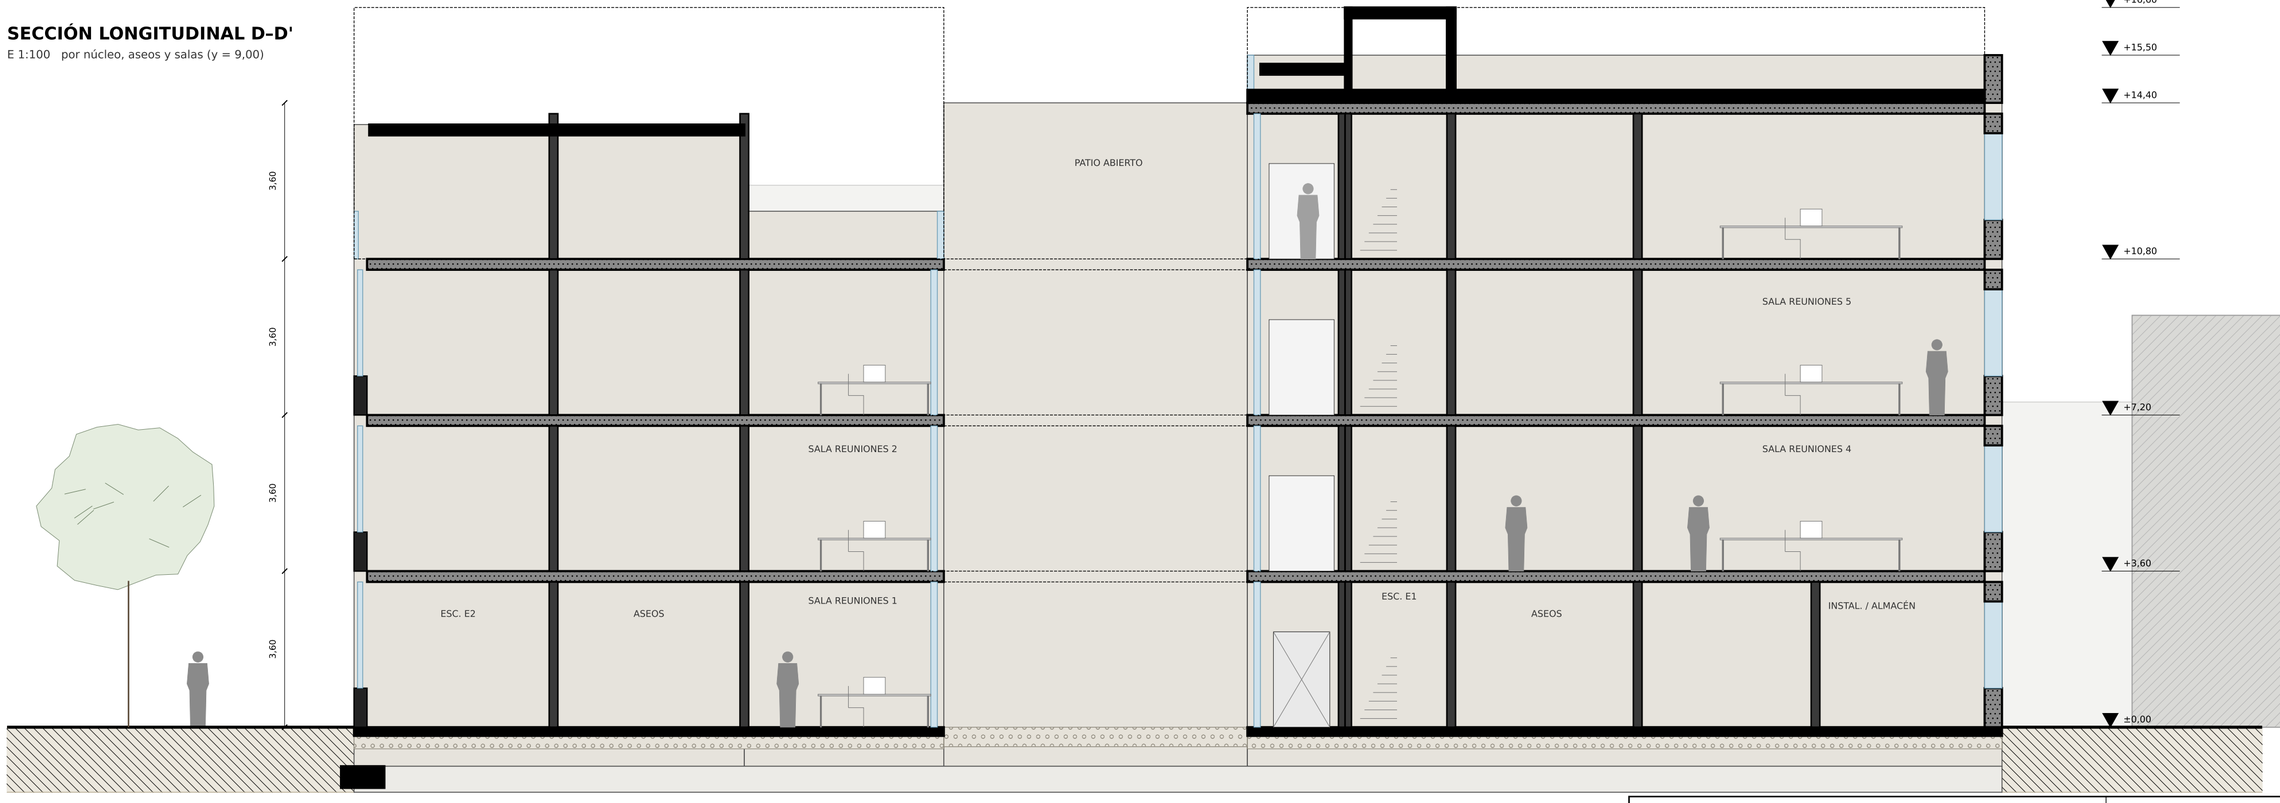

CASO_009 · PROPUESTA A

Secciones longitudinales A-A' y D-D'

Anteproyecto · Renovación integral de edificio de oficinas

Lámina

S01

Escala

1:100

Anteproyecto