

1 · CIMENTACIÓN Y ARRANQUE DE FACHADA

E 1:20

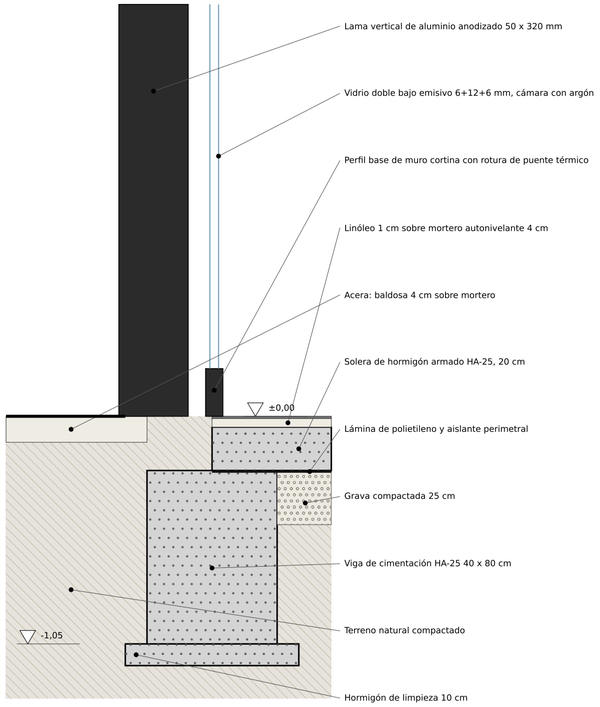


2 · FORJADO TIPO Y MURO CORTINA

E 1:20

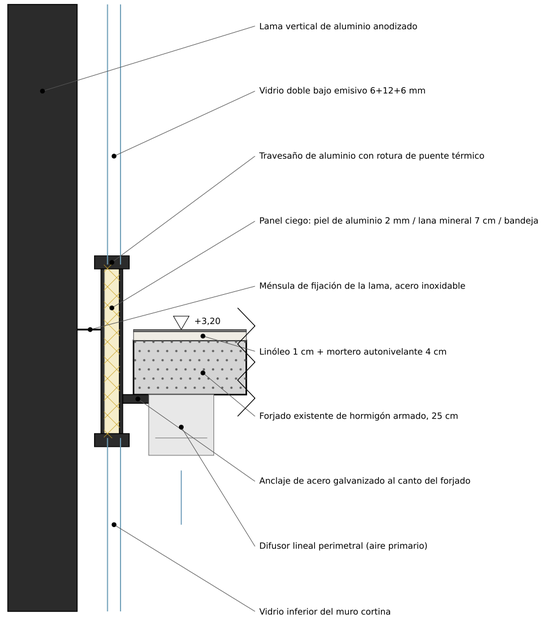


3 · CUBIERTA FRONTAL Y PETO

E 1:20

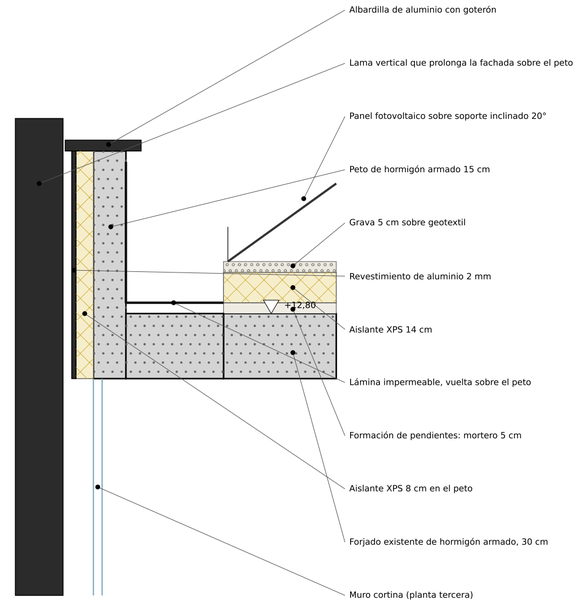


4 · FACHADA POSTERIOR Y VOLADIZO

E 1:20

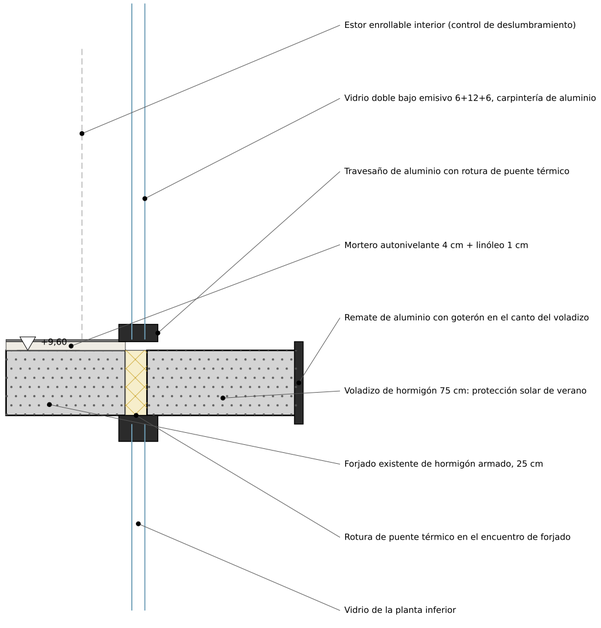


5 · ENCUENTRO CON LA MEDIANERA EXISTENTE

E 1:20

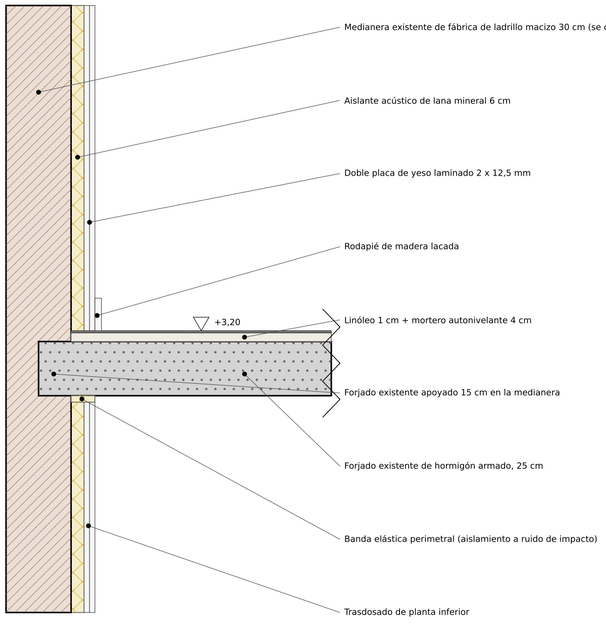

6 · BORDE DE LA LINTERNA ZENITAL

E 1:20

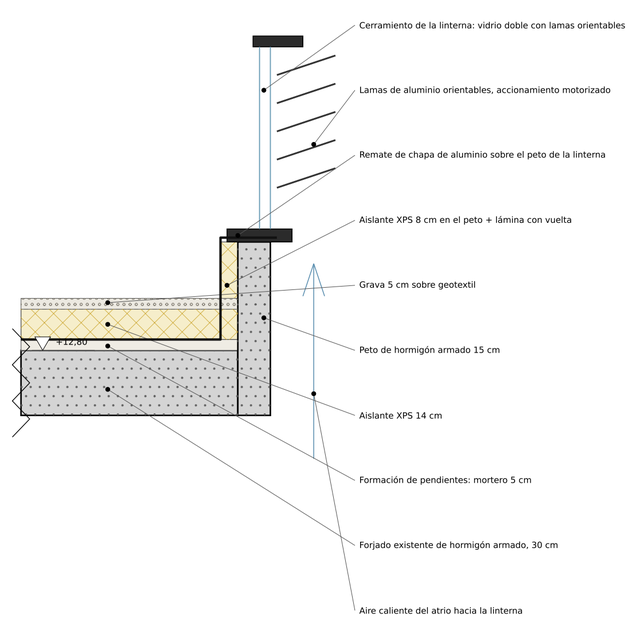

CASO_009 · PROPUESTA B

Anteproyecto

Detalle constructivo de fachada (seis fragmentos)

Escala 1:20

Cotas de nivel en metros; espesores en cm

Lámina D01