
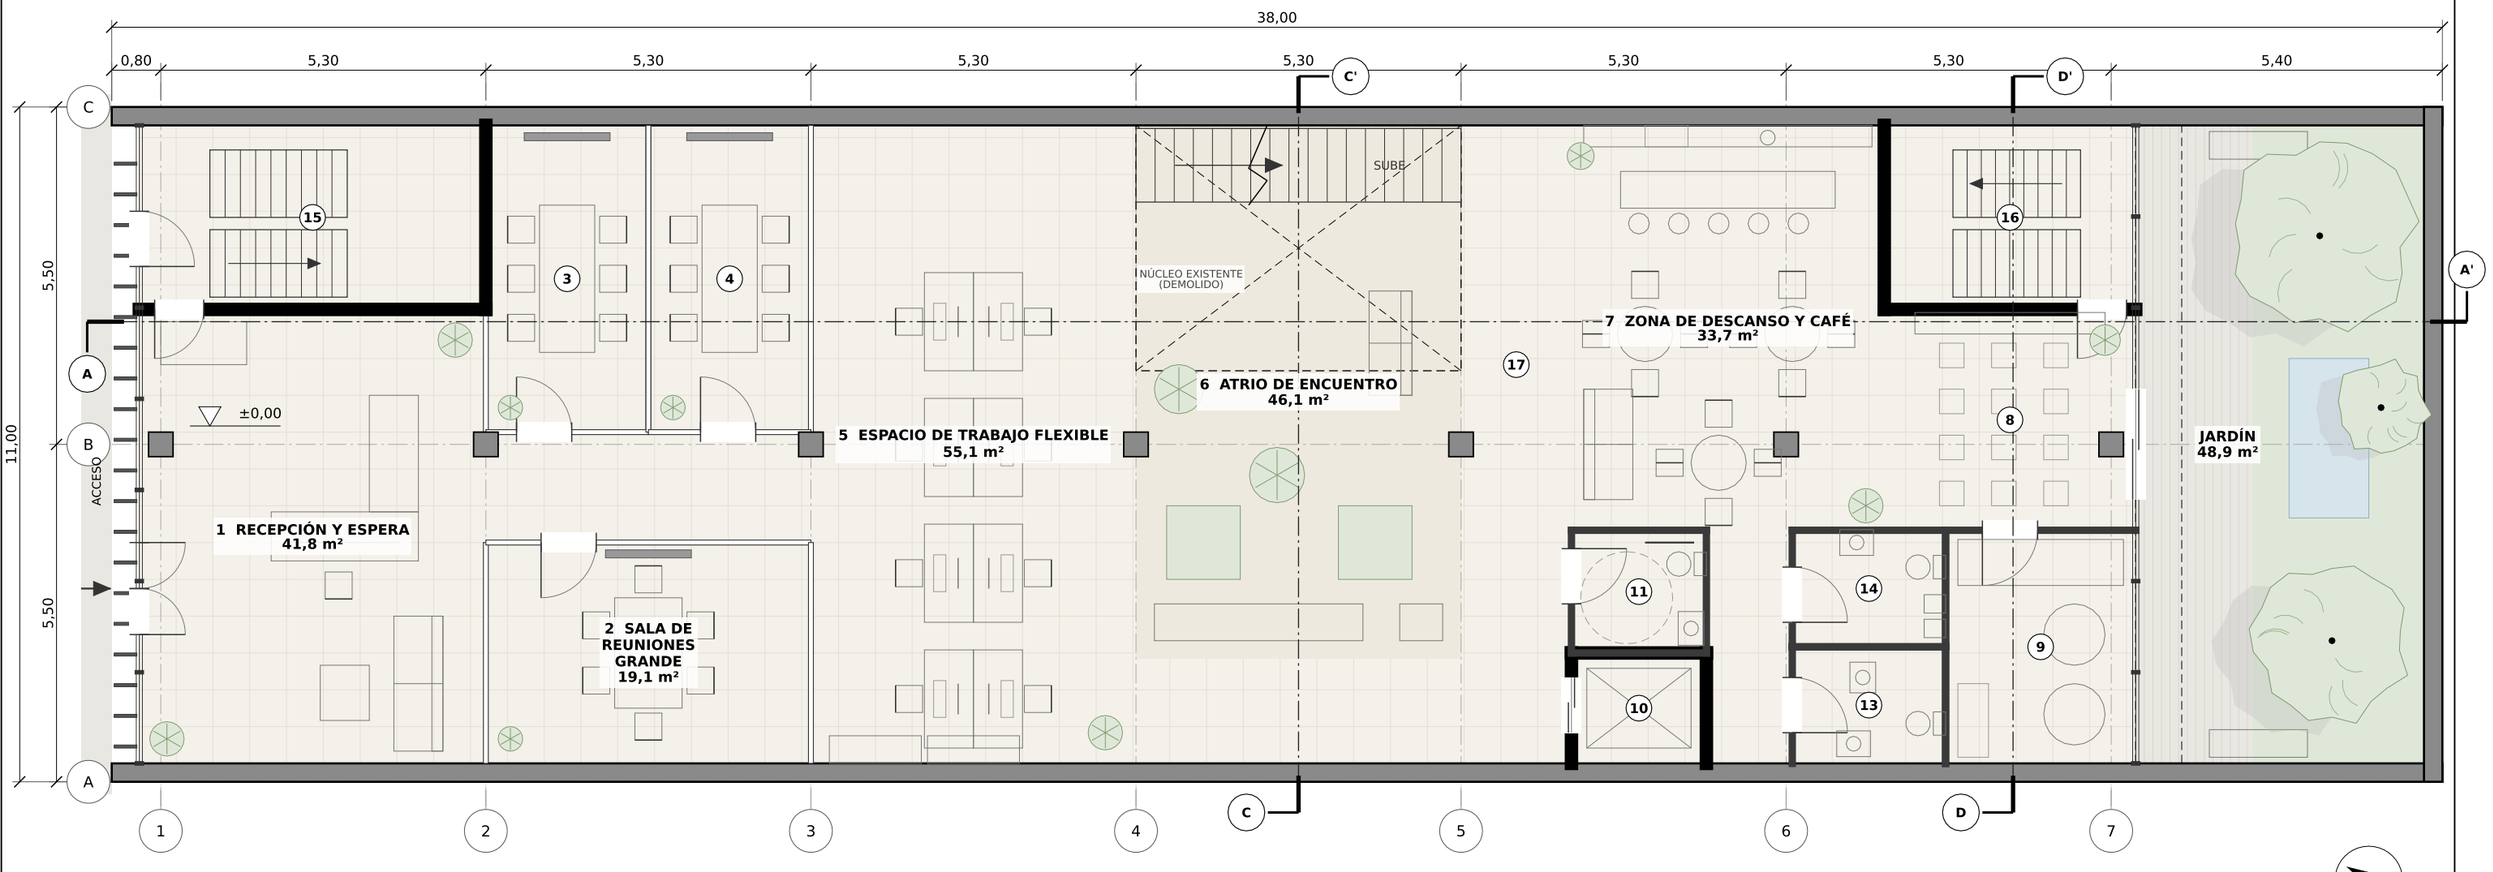


PLANTA BAJA

E 1:100

ESQUEMA DE ACCESIBILIDAD Y EVACUACIÓN · E 1:200

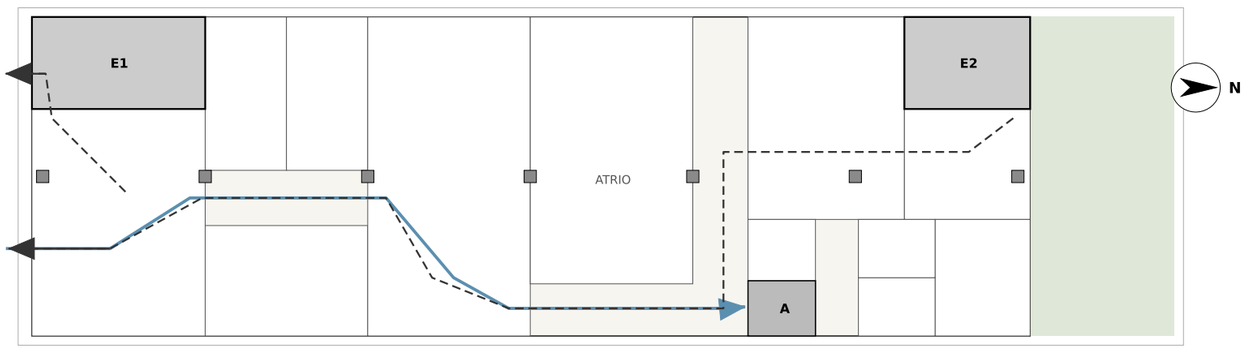

LEYENDA

- Existente que se conserva (medianeras, pilares y forjados)
- Obra nueva: muros de hormigón de núcleos y escaleras
- Tabique nuevo / vidrio de salas (línea fina doble)
- Existente que se demuele (trazo discontinuo)
- Itinerario accesible (ascensor y plano a nivel)
- Recorrido de evacuación hacia escalera protegida

CUADRO DE SUPERFICIES ÚTILES

1	Recepción y espera	41,8 m²	10	Ascensor accesible	4,0 m²
2	Sala de reuniones grande	19,1 m²	11	Aseo adaptado	4,4 m²
3	Sala de reuniones pequeña I	13,2 m²	12	Vestíbulo de aseos	5,3 m²
4	Sala de reuniones pequeña II	13,2 m²	13	Aseo mujeres	4,8 m²
5	Espacio de trabajo flexible	55,1 m²	14	Aseo hombres	4,7 m²
6	Atrio de encuentro	46,1 m²	15	Escalera de emergencia 1	16,9 m²
7	Zona de descanso y café	33,7 m²	16	Escalera de emergencia 2	12,3 m²
8	Sala polivalente	14,8 m²	17	Circulación y distribución	37,3 m²
9	Instalaciones y almacén	11,8 m²			

Superficie útil del nivel: 338,5 m²

Superficie construida del nivel: 363,0 m²

CASO_009 · PROPUESTA B

Anteproyecto

Planta baja

Escala 1:100

Medidas en metros

Lámina P01